


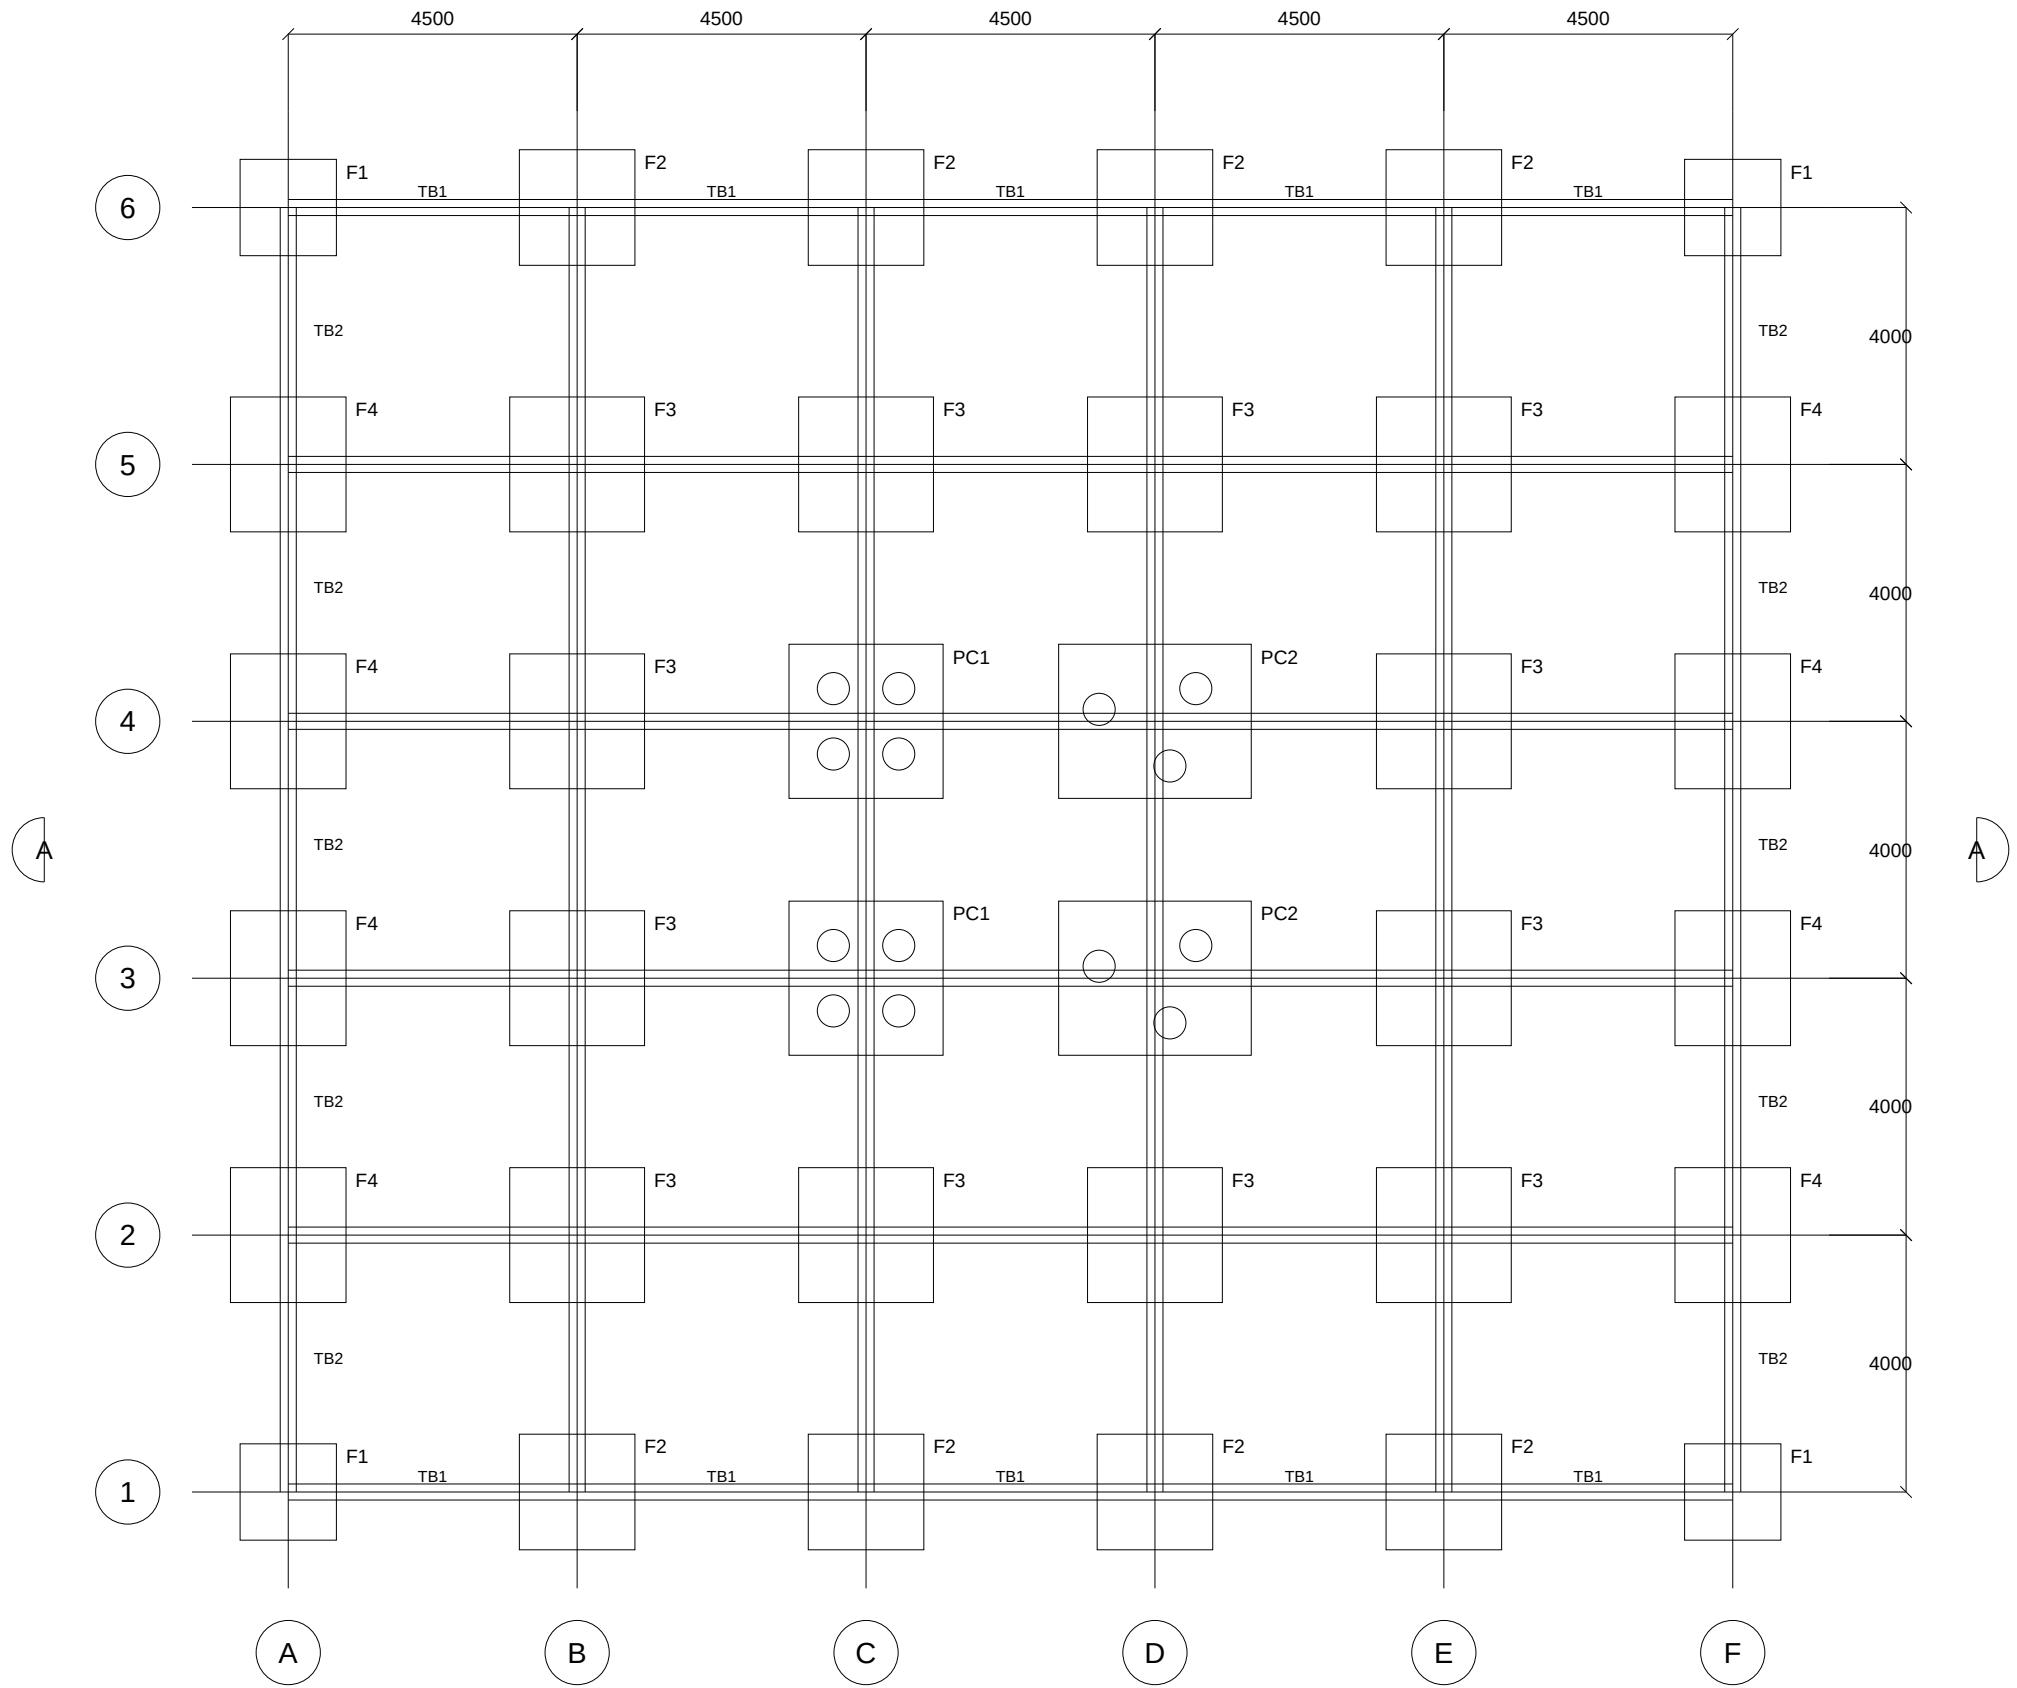


FOUNDATION PLAN

FOOTING TOP AT -1.500 | TIE BEAMS TB1 / TB2 AT FDN

FOUNDATION PLAN

F-RCC6 SAMPLE SIX-STOREY RCC RESIDENTIAL BUILDING

SHEET 1 OF 8 | A3 | ALL DIMENSIONS IN mm

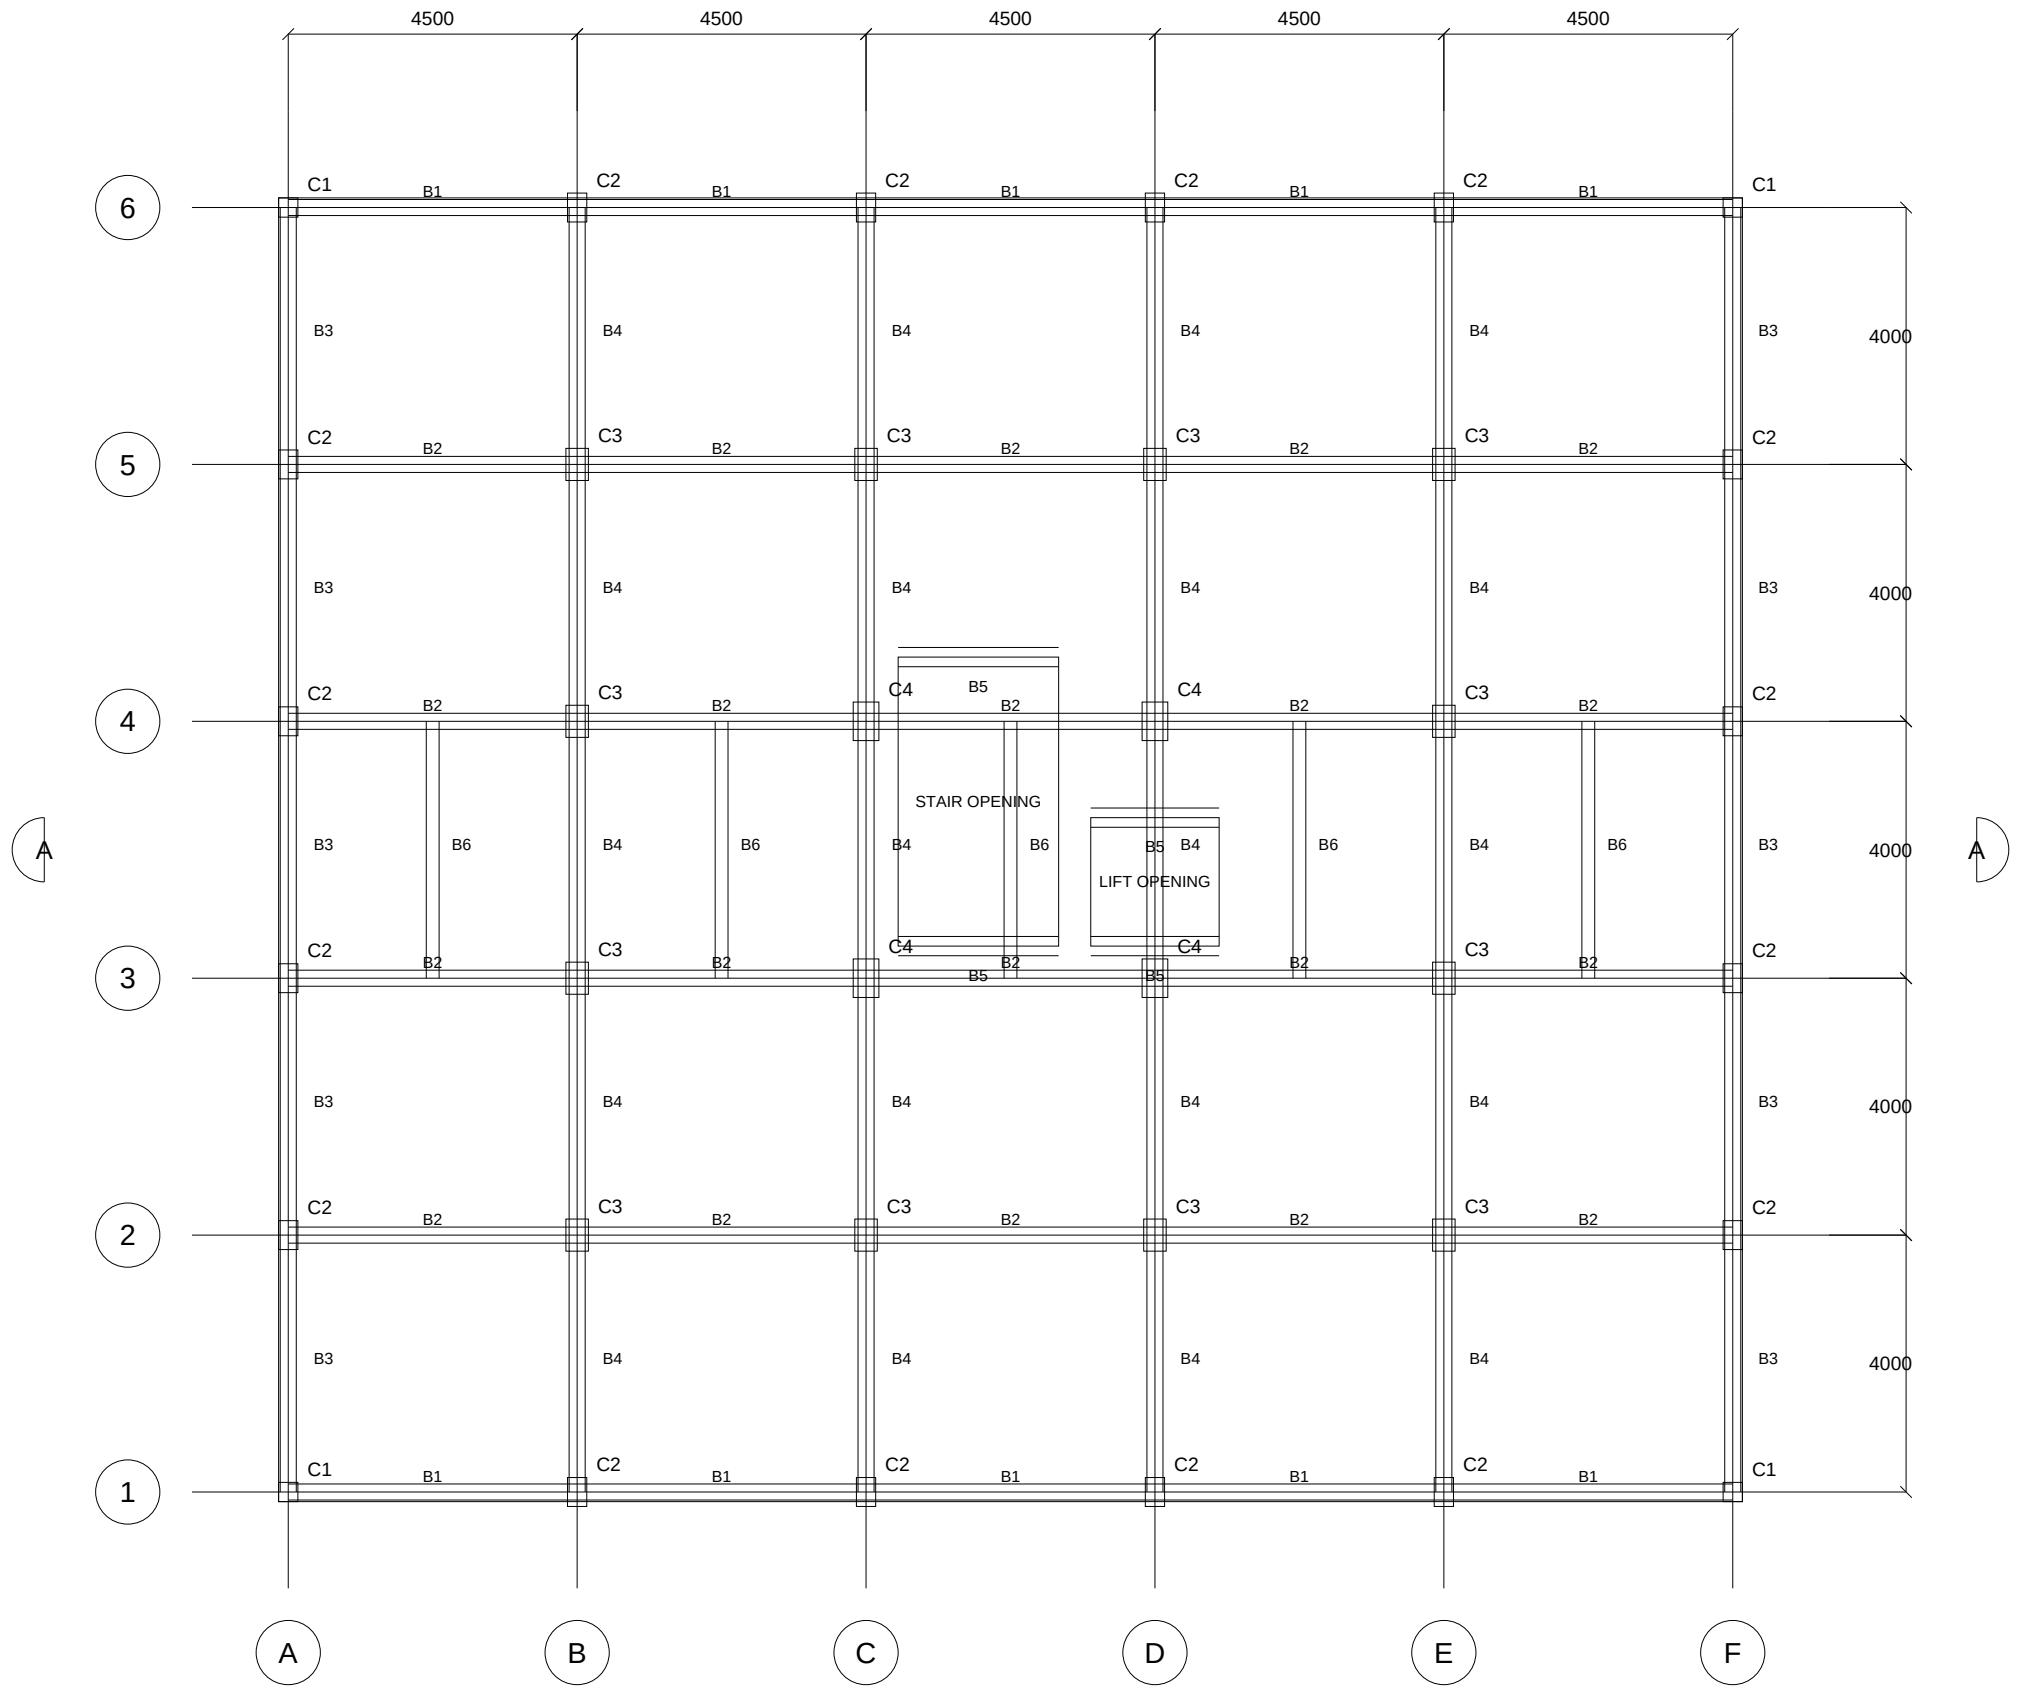


TYPICAL FLOOR PLAN

1F TO 5F | SLAB 150 THK | SEE COLUMN AND BEAM SCHEDULES

TYPICAL FLOOR PLAN

F-RCC6 SAMPLE SIX-STOREY RCC RESIDENTIAL BUILDING

SHEET 2 OF 8 | A3 | ALL DIMENSIONS IN mm

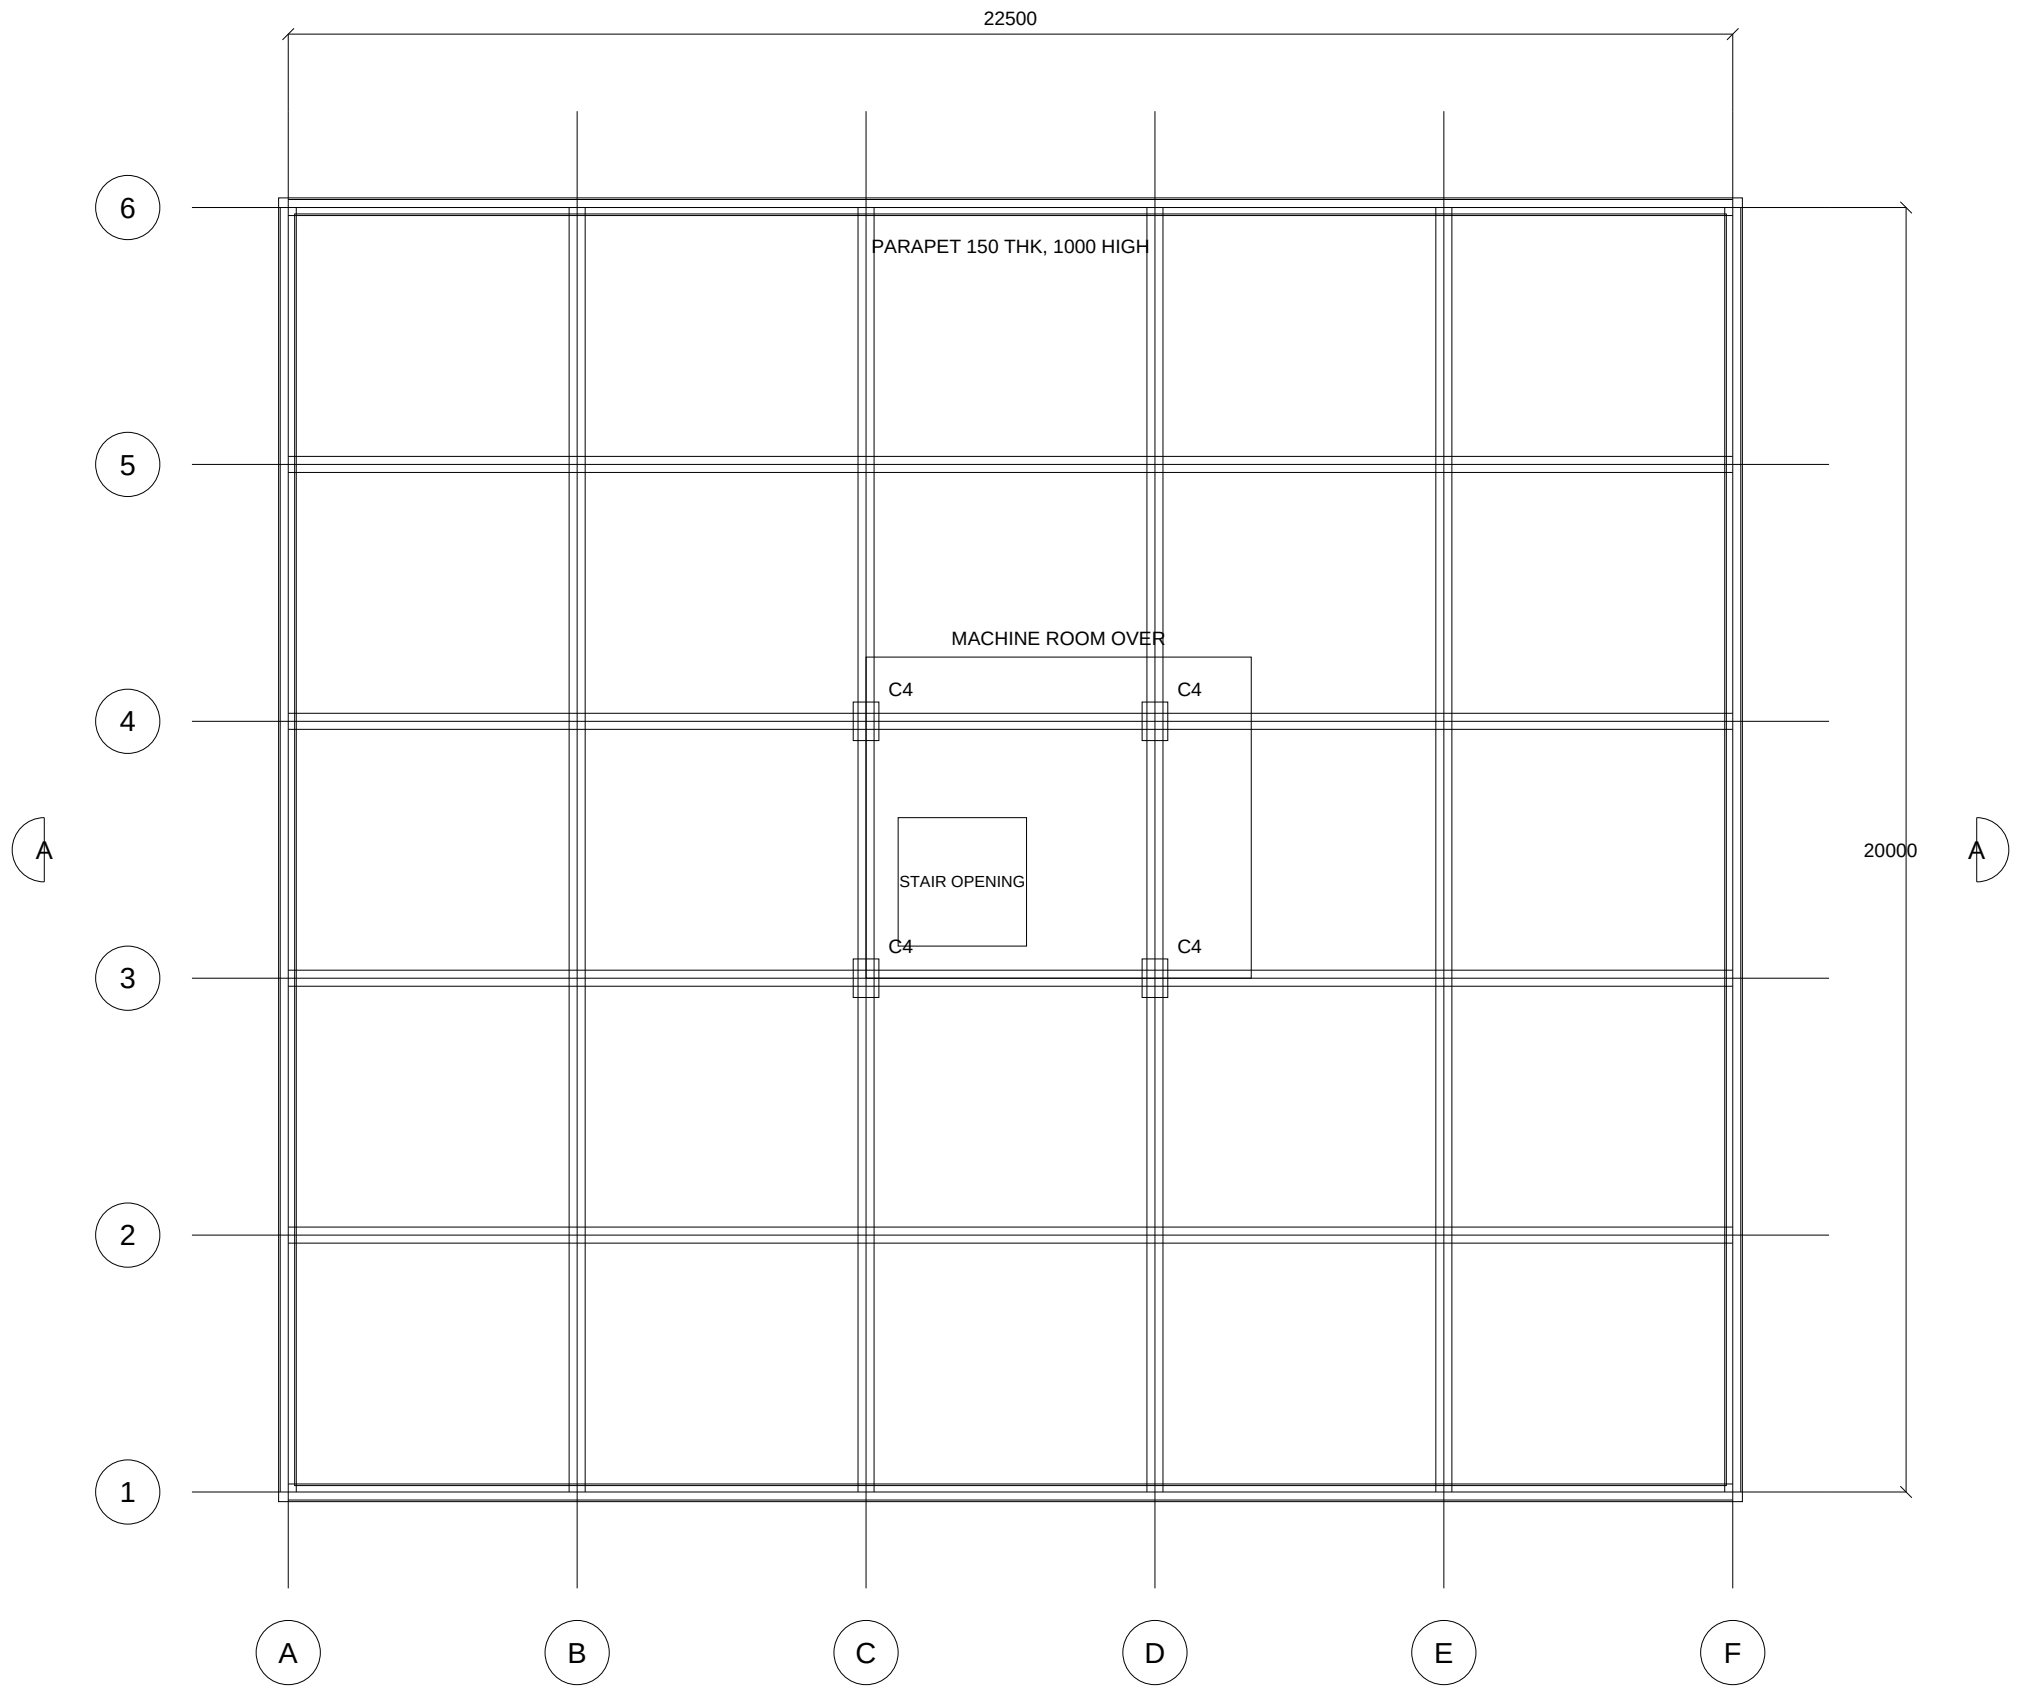

ROOF PLAN

ROOF SLAB 150 THK AT +18.000 | B1 TO B4 AT ROOF

ROOF PLAN

F-RCC6 SAMPLE SIX-STOREY RCC RESIDENTIAL BUILDING

SHEET 3 OF 8 | A3 | ALL DIMENSIONS IN mm

COLUMN SCHEDULE

MARK	SIZE b x d (mm)	LEVELS	MAIN BARS	LINKS	NOS
C1	300 x 300	GF TO 5F	8-T16	T8 @ 150	4
C2	300 x 450	GF TO 5F	8-T20	T8 @ 150	16
C3	350 x 500	GF TO 5F	10-T20	T8 @ 125	12
C4	400 x 600	GF TO ROOF	12-T25	T10 @ 100	4

ALL COLUMNS M25 CONCRETE, Fe500 BARS, 40 mm CLEAR COVER

COLUMN SCHEDULE

F-RCC6 SAMPLE SIX-STOREY RCC RESIDENTIAL BUILDING

SHEET 4 OF 8 | A3 | ALL DIMENSIONS IN mm

BEAM SCHEDULE

MARK	SIZE b x d (mm)	SPAN	LEVELS	BARS	STIRRUPS	NOS PER LEVEL
B1	250 x 450	4.5 m	1F TO ROOF	3-T16 T / 3-T16 B	T8 @ 150	10
B2	250 x 500	4.5 m	1F TO ROOF	3-T16 T / 4-T16 B	T8 @ 150	20
B3	250 x 450	4.0 m	1F TO ROOF	3-T16 T / 3-T16 B	T8 @ 150	10
B4	250 x 500	4.0 m	1F TO ROOF	3-T16 T / 4-T16 B	T8 @ 150	20
B5	300 x 600	4.5 m	1F TO 5F	4-T20 T / 4-T20 B	T8 @ 150	4
B6	200 x 400	4.0 m	1F TO 5F	2-T12 T / 3-T12 B	T8 @ 150	5
TB1	250 x 400	4.5 m	FDN	2-T16 T / 2-T16 B	T8 @ 200	30
TB2	250 x 400	4.0 m	FDN	2-T16 T / 2-T16 B	T8 @ 200	30

BEAM DEPTHS INCLUDE THE SLAB; SPANS ARE GRID TO GRID

BEAM SCHEDULE

F-RCC6 SAMPLE SIX-STOREY RCC RESIDENTIAL BUILDING

SHEET 5 OF 8 | A3 | ALL DIMENSIONS IN mm

FOOTING SCHEDULE

MARK	L x B (mm)	DEPTH (mm)	BARS	NOS
F1	1500 x 1500	450	T12 @ 150 B/W	4
F2	1800 x 1800	500	T12 @ 150 B/W	8
F3	2100 x 2100	550	T12 @ 150 B/W	12
F4	1800 x 2100	500	T12 @ 150 B/W	8
PC1	2400 x 2400	900	T16 @ 125 B/W ON 4 PILES	2
PC2	3000 x 2400	900	T16 @ 125 B/W ON 3 PILES	2

FOOTING TOP AT -1.500, 50 mm CLEAR COVER, 75 mm BLINDING BELOW

FOOTING SCHEDULE

F-RCC6 SAMPLE SIX-STOREY RCC RESIDENTIAL BUILDING

SHEET 6 OF 8 | A3 | ALL DIMENSIONS IN mm



SECTION A-A

SECTIONS | STOREY HEIGHTS PER LEVEL STACK, SEE GENERAL NOTES

SECTIONS

F-RCC6 SAMPLE SIX-STOREY RCC RESIDENTIAL BUILDING

SHEET 7 OF 8 | A3 | ALL DIMENSIONS IN mm

GENERAL NOTES

1. CONCRETE

M25 FOR ALL RCC WORK ($f_{ck} = 25 \text{ N/mm}^2$). CEMENT OPC 43 GRADE.

MAXIMUM AGGREGATE 20 mm, SLUMP 75 TO 100 mm.
2. REINFORCEMENT

Fe500 HIGH YIELD DEFORMED BARS, $f_y = 500 \text{ N/mm}^2$.

BAR MARKS: T = Fe500.
3. CLEAR COVER

FOOTINGS AND PILE CAPS 50 mm, COLUMNS 40 mm, BEAMS 25 mm, SLABS 20 mm.
4. LAPS

LAP LENGTH 50d FOR BARS IN TENSION, STAGGERED, NOT MORE THAN 50% OF BARS LAPPED AT ONE SECTION. NO LAPS AT BEAM-COLUMN JOINTS.
5. LEVELS

GF AT +0.000. FOOTING TOP AT -1.500. TYPICAL STOREY 3.000 m, ROOF MACHINE ROOM 2.400 m.
6. DIMENSIONS

ALL DIMENSIONS IN mm UNLESS NOTED. LEVELS IN m. DO NOT SCALE.

GRID A TO F AND 1 TO 6 AS PLANS.

SIX-STOREY RCC RESIDENTIAL BUILDING

GENERAL NOTES

F-RCC6 SAMPLE SIX-STOREY RCC RESIDENTIAL BUILDING

SHEET 8 OF 8 | A3 | ALL DIMENSIONS IN mm