



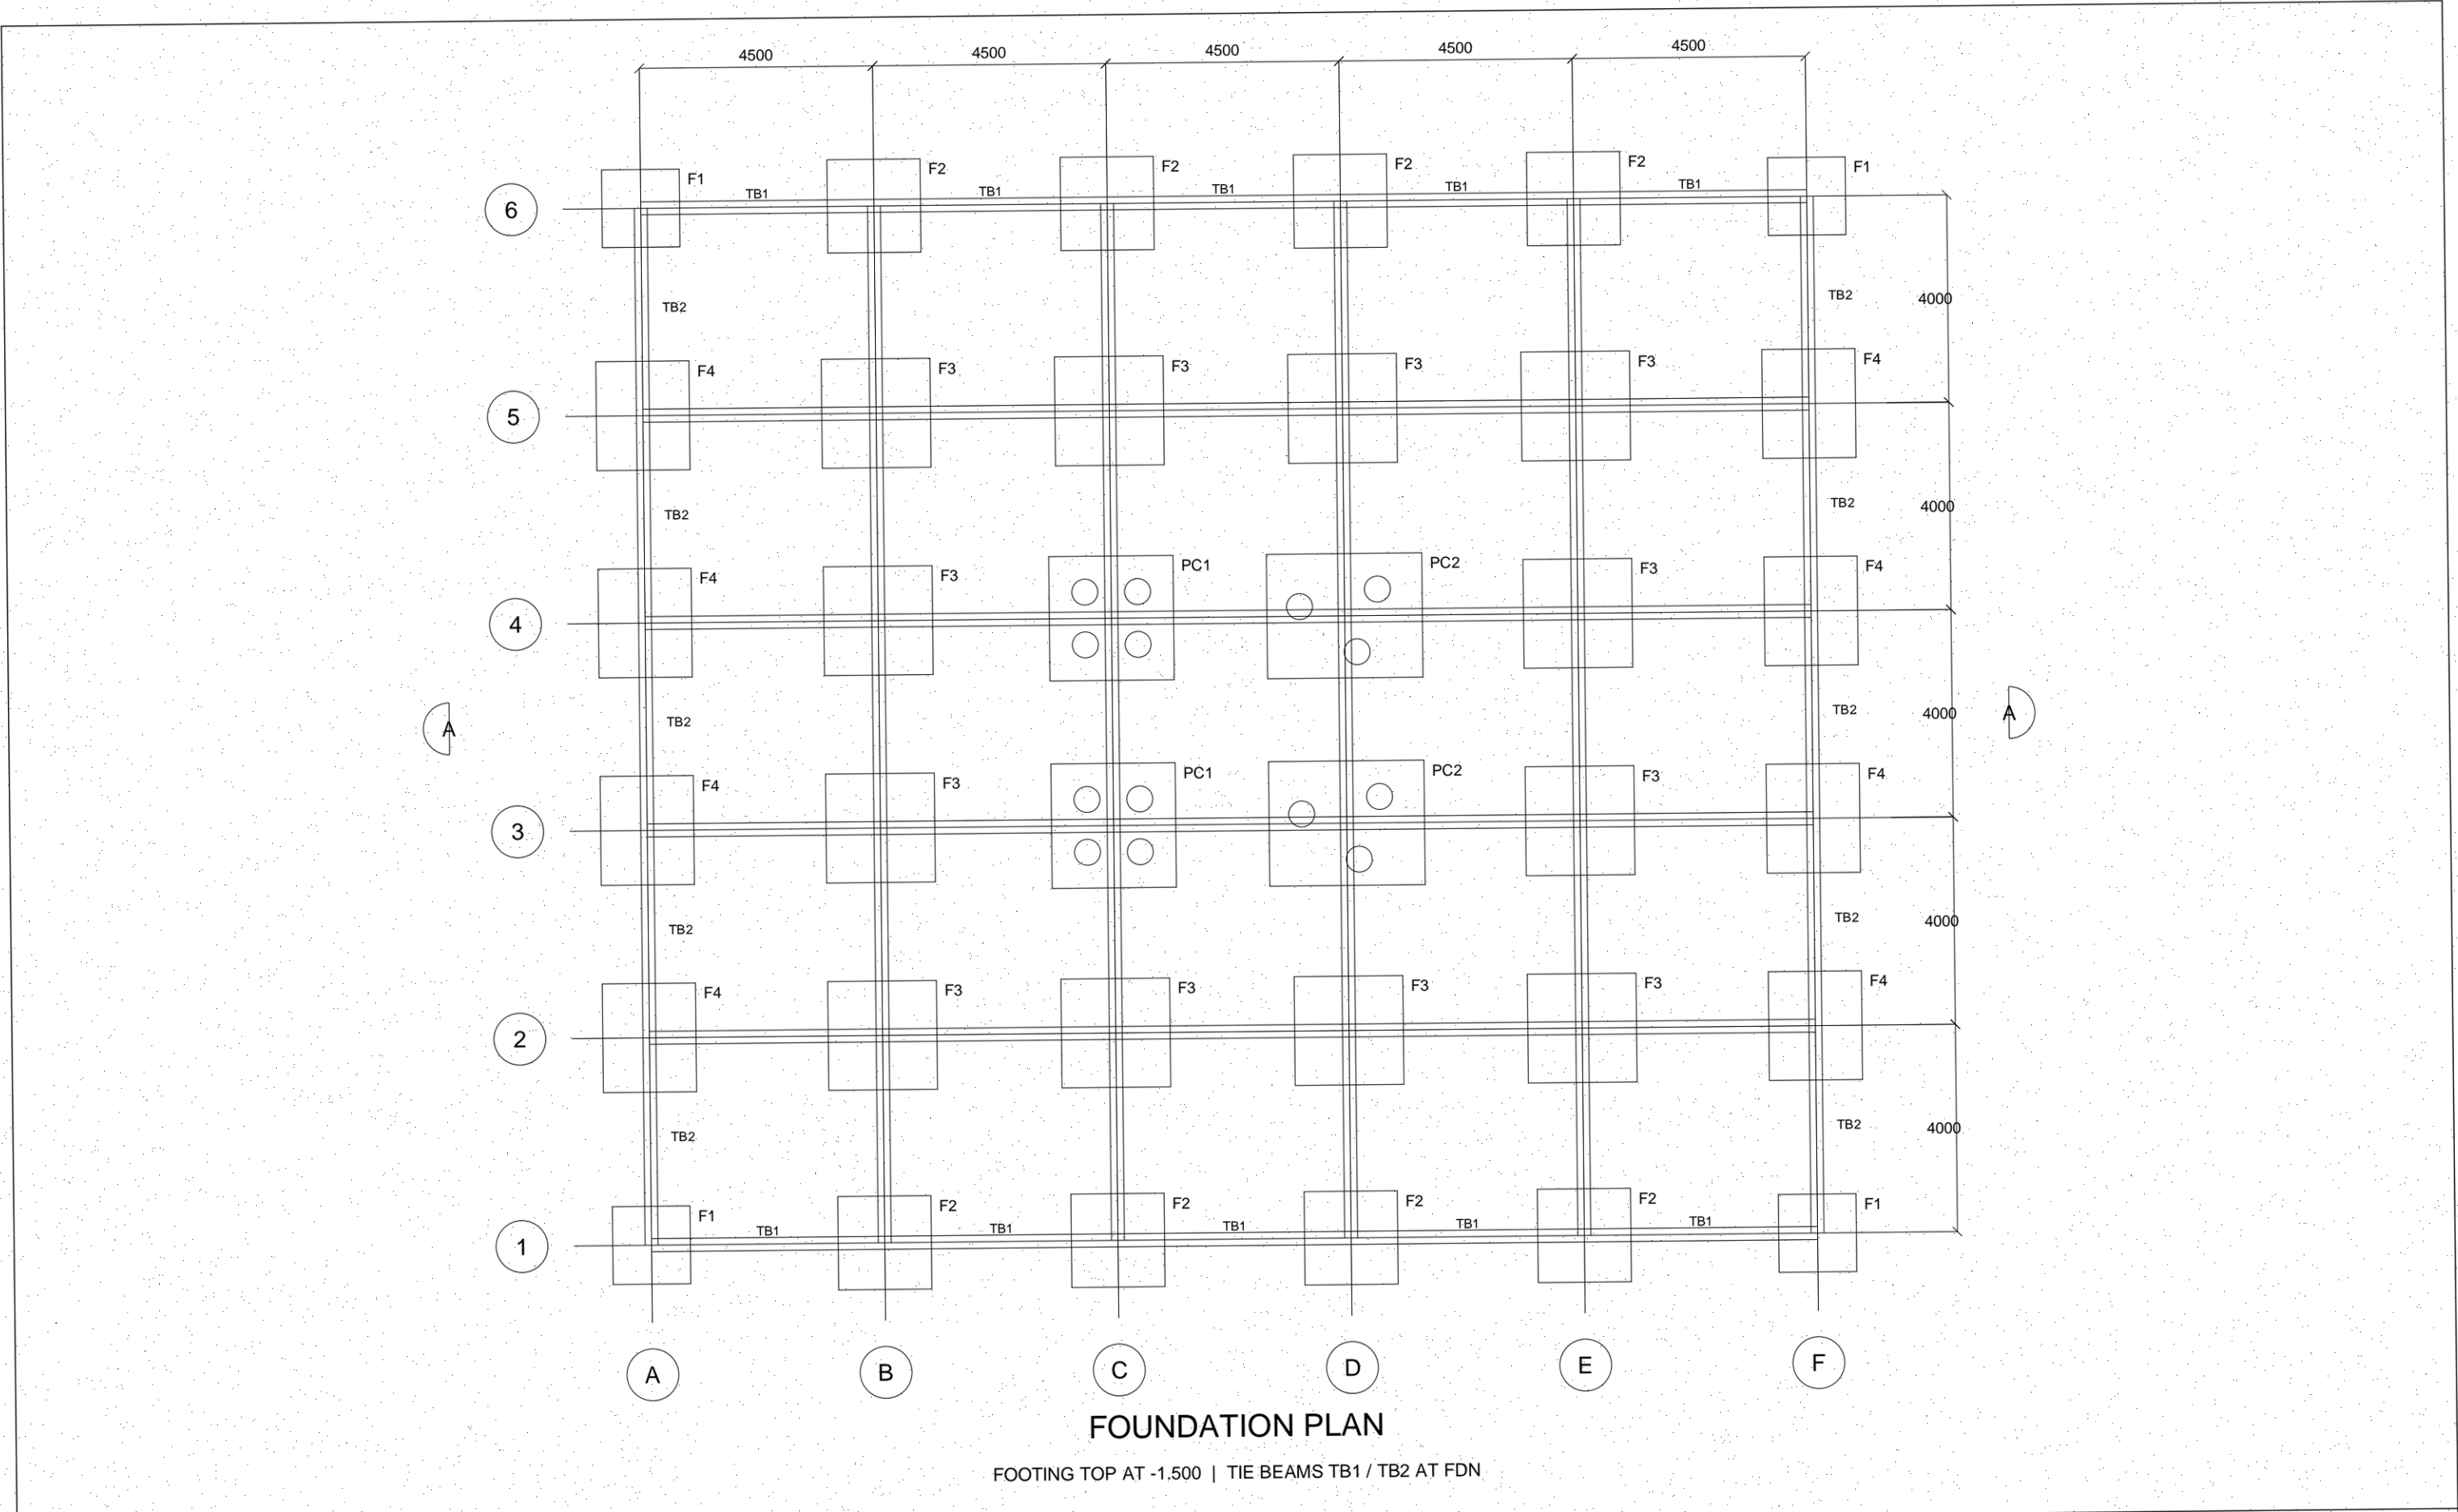

FOUNDATION PLAN

F-RCC6 SAMPLE SIX-STOREY RCC RESIDENTIAL BUILDING

SHEET 1 OF 8 | A3 | ALL DIMENSIONS IN mm

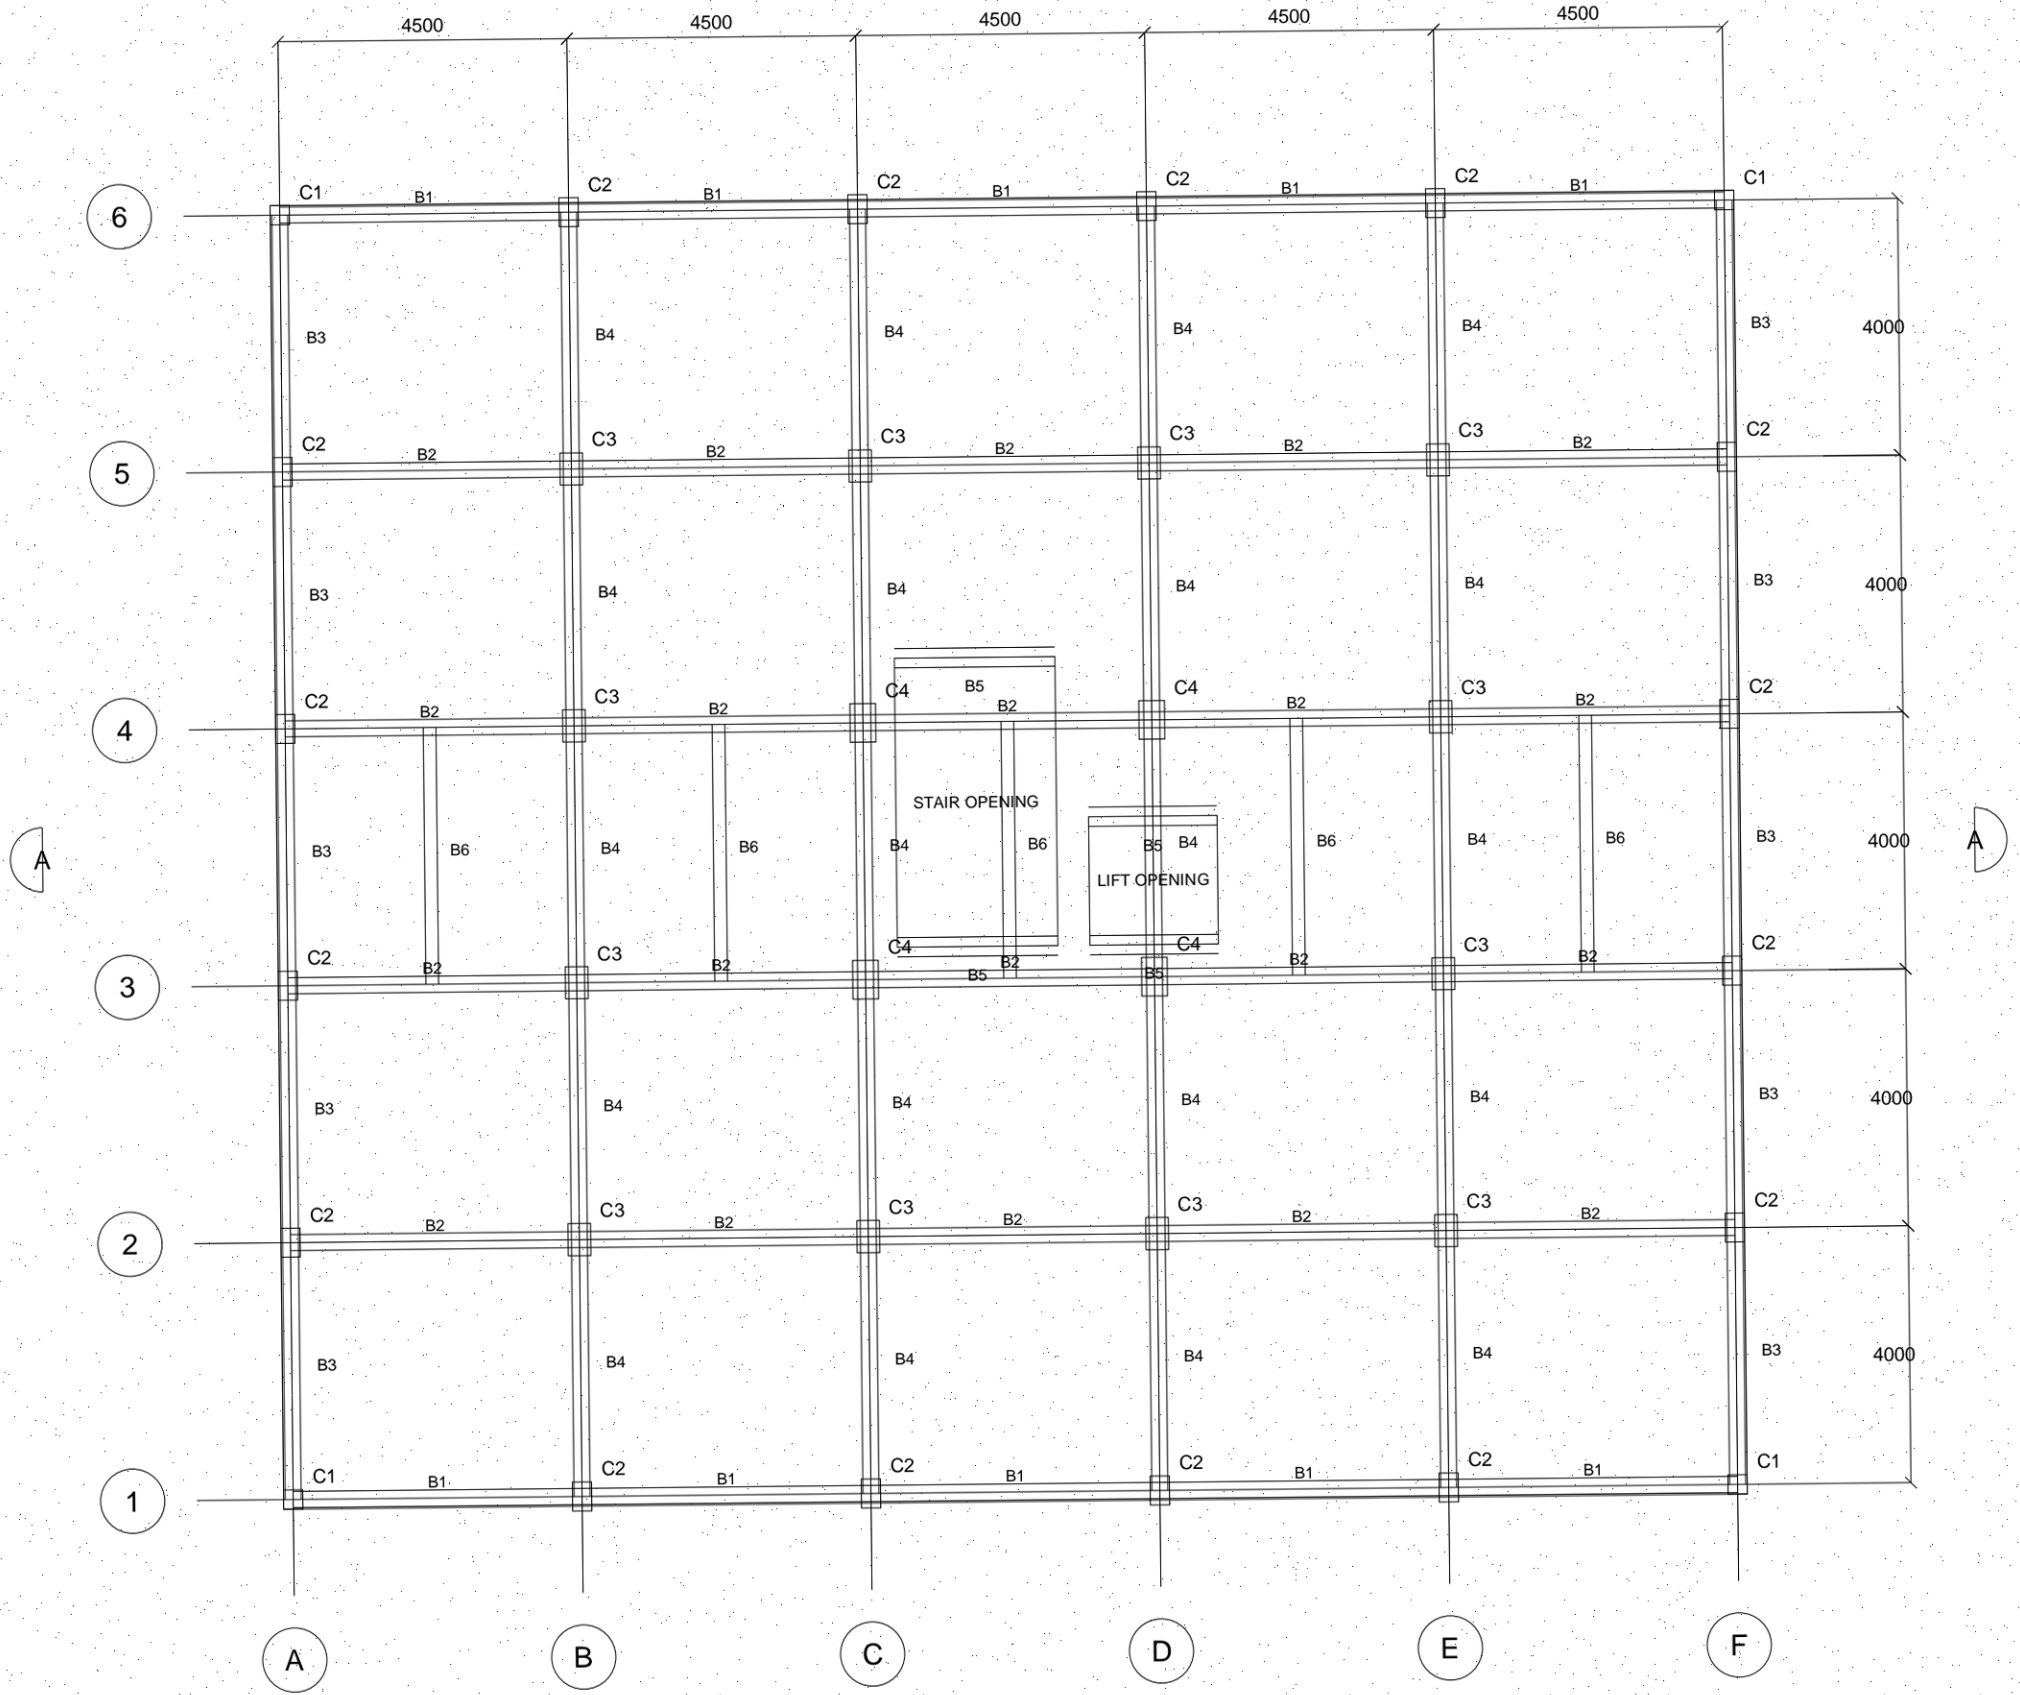


TYPICAL FLOOR PLAN

1F TO 5F | SLAB 150 THK | SEE COLUMN AND BEAM SCHEDULES

TYPICAL FLOOR PLAN

F-RCC6 SAMPLE SIX-STOREY RCC RESIDENTIAL BUILDING

SHEET 2 OF 8 | A3 | ALL DIMENSIONS IN mm

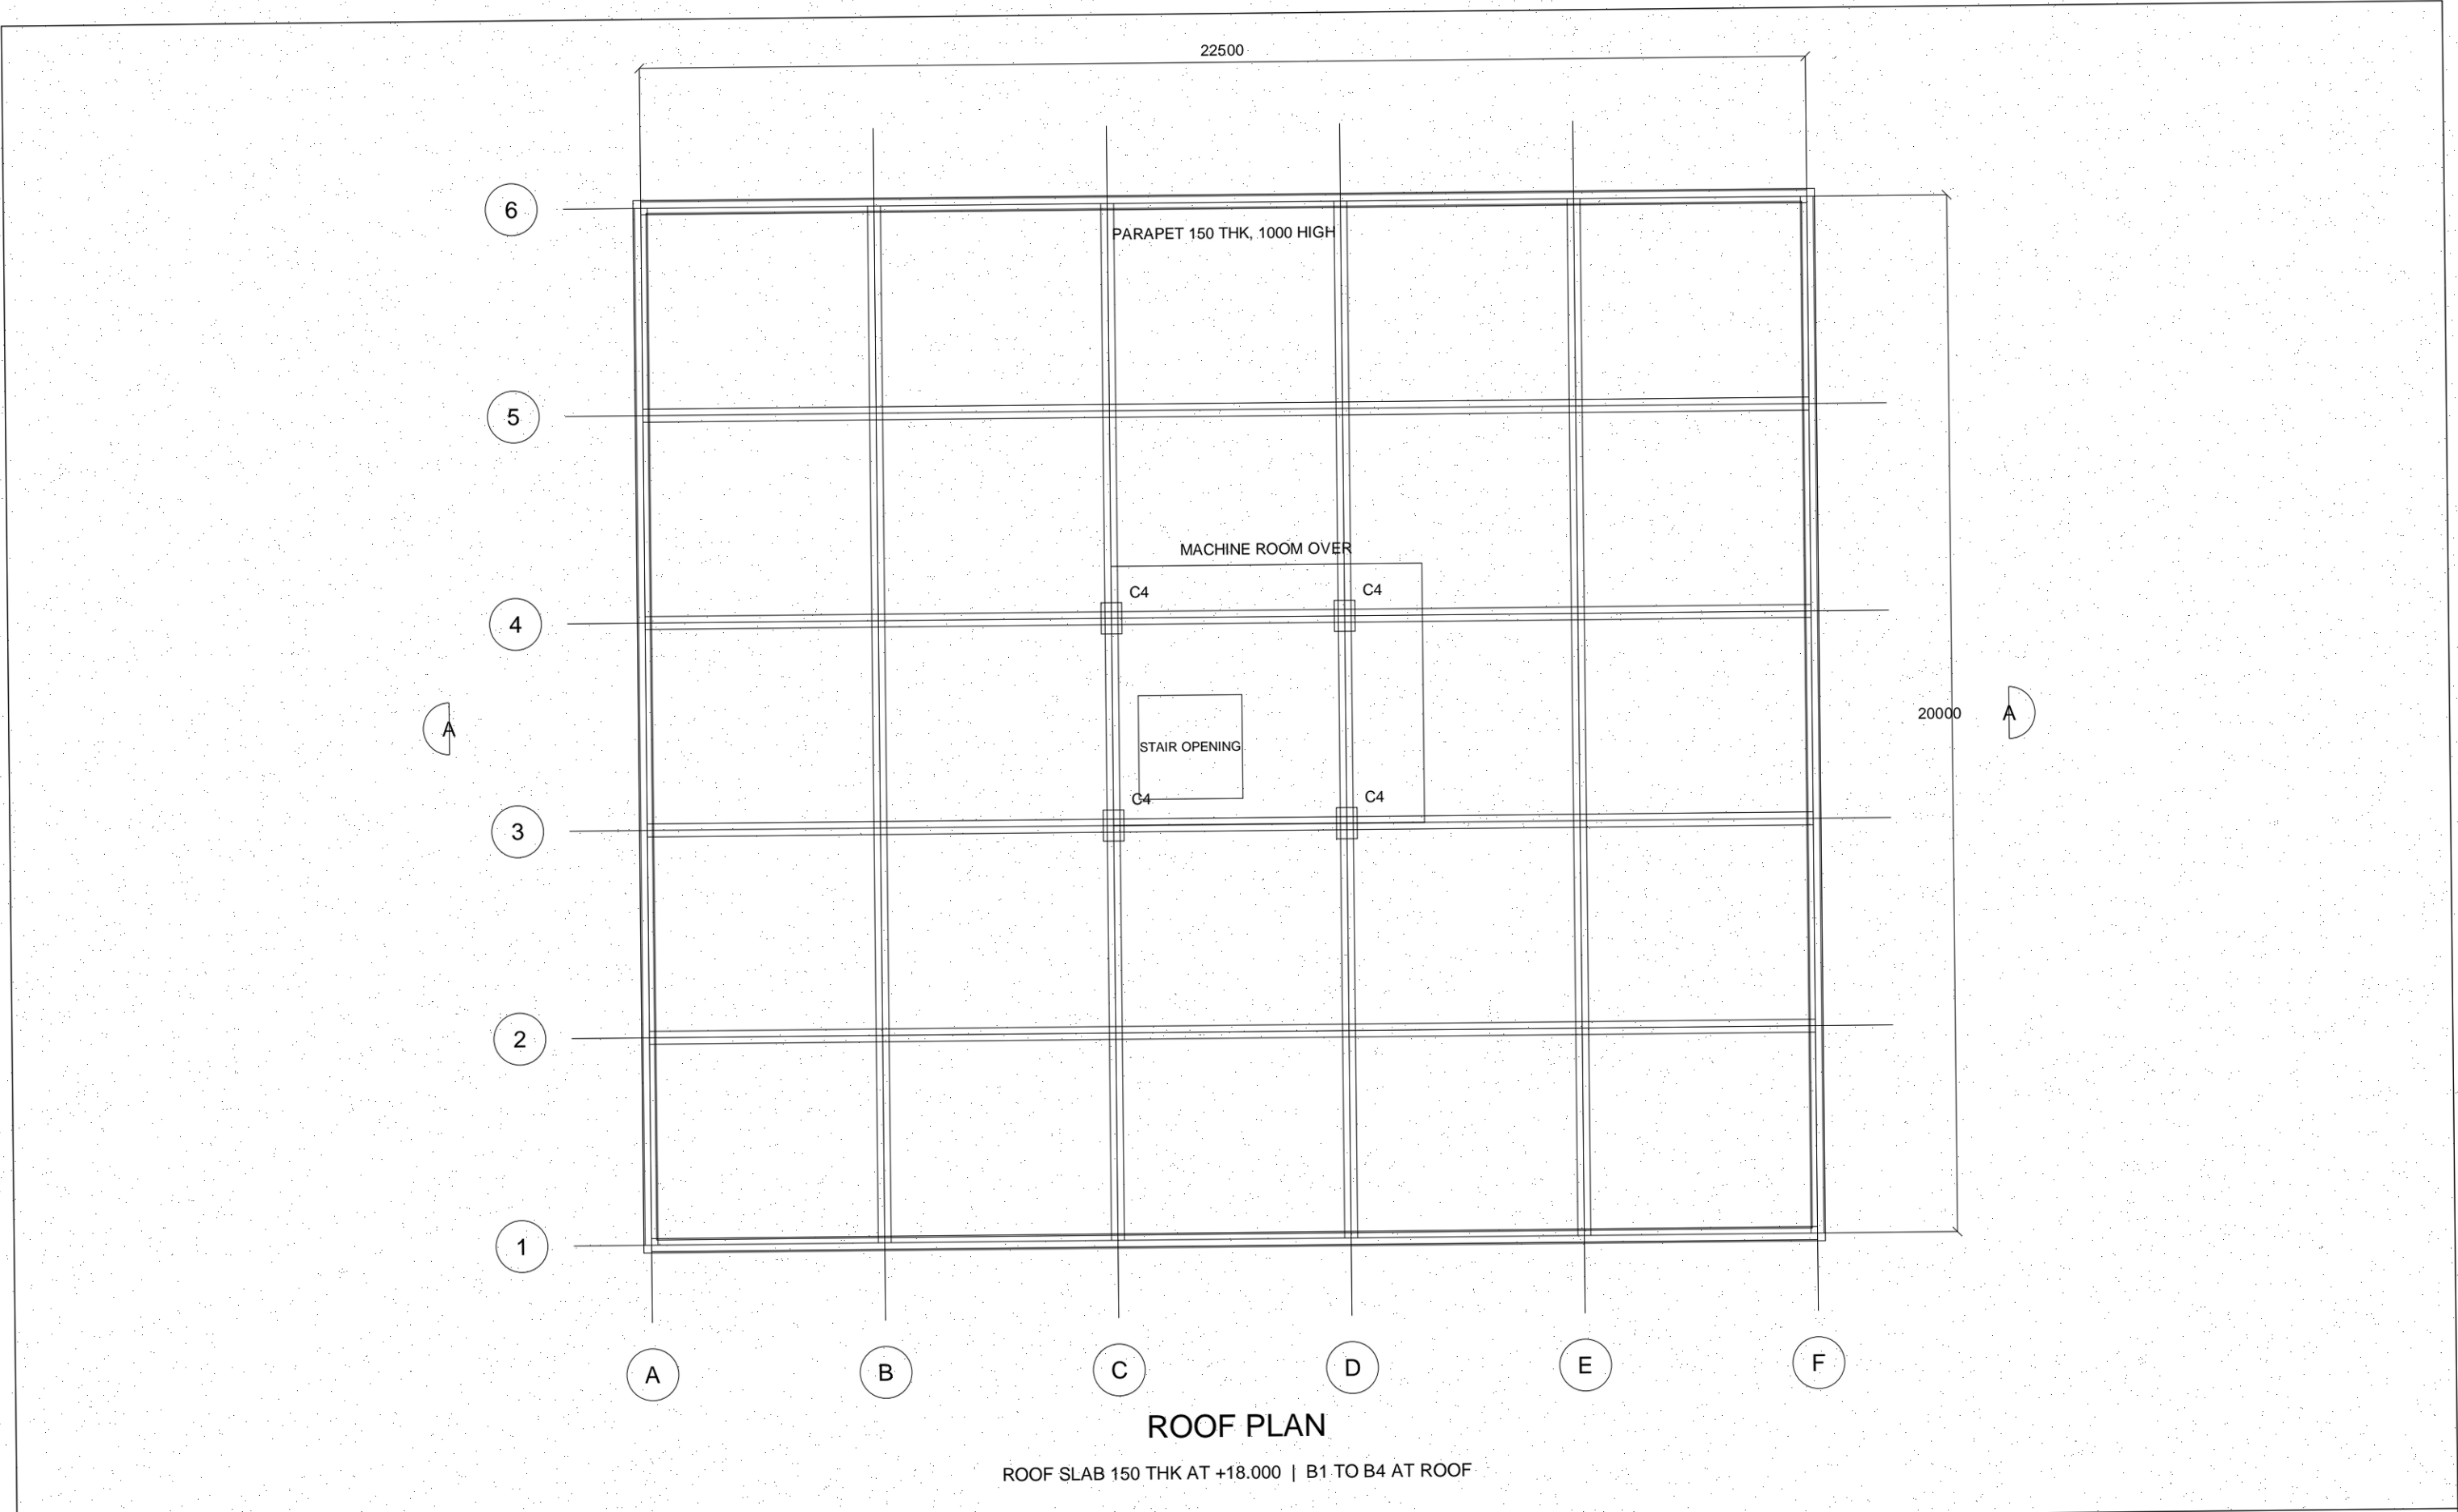

ROOF PLAN

F-RCC6 SAMPLE SIX-STOREY RCC RESIDENTIAL BUILDING

SHEET 3 OF 8 | A3 | ALL DIMENSIONS IN mm

COLUMN SCHEDULE

MARK	SIZE b x d (mm)	LEVELS	MAIN BARS	LINKS	NOS
C1	300 x 300	GF TO 5F	8-T16	T8 @ 150	4
C2	300 x 450	GF TO 5F	8-T20	T8 @ 150	16
C3	350 x 500	GF TO 5F	10-T20	T8 @ 125	12
C4	400 x 600	GF TO ROOF	12-T25	T10 @ 100	4

ALL COLUMNS M25 CONCRETE, Fe500 BARS, 40 mm CLEAR COVER

COLUMN SCHEDULE

F-RCC6 SAMPLE SIX-STOREY RCC RESIDENTIAL BUILDING

SHEET 4 OF 8 | A3 | ALL DIMENSIONS IN mm

BEAM SCHEDULE

MARK	SIZE b x d (mm)	SPAN	LEVELS	BARS	STIRRUPS	NOS PER LEVEL
B1	250 x 450	4.5 m	1F TO ROOF	3-T16 T / 3-T16 B	T8 @ 150	10
B2	250 x 500	4.5 m	1F TO ROOF	3-T16 T / 4-T16 B	T8 @ 150	20
B3	250 x 450	4.0 m	1F TO ROOF	3-T16 T / 3-T16 B	T8 @ 150	10
B4	250 x 500	4.0 m	1F TO ROOF	3-T16 T / 4-T16 B	T8 @ 150	20
B5	300 x 600	4.5 m	1F TO 5F	4-T20 T / 4-T20 B	T8 @ 150	4
B6	200 x 400	4.0 m	1F TO 5F	2-T12 T / 3-T12 B	T8 @ 150	5
TB1	250 x 400	4.5 m	FDN	2-T16 T / 2-T16 B	T8 @ 200	30
TB2	250 x 400	4.0 m	FDN	2-T16 T / 2-T16 B	T8 @ 200	30

BEAM DEPTHS INCLUDE THE SLAB; SPANS ARE GRID TO GRID

BEAM SCHEDULE

F-RCC6 SAMPLE SIX-STOREY RCC RESIDENTIAL BUILDING
SHEET 5 OF 8 | A3 | ALL DIMENSIONS IN mm


FOOTING SCHEDULE

MARK	L x B (mm)	DEPTH (mm)	BARS	NOS
F1	1500 x 1500	450	T12 @ 150 B/W	4
F2	1800 x 1800	500	T12 @ 150 B/W	8
F3	2100 x 2100	550	T12 @ 150 B/W	12
F4	1800 x 2100	500	T12 @ 150 B/W	8
PC1	2400 x 2400	900	T16 @ 125 B/W ON 4 PILES	2
PC2	3000 x 2400	900	T16 @ 125 B/W ON 3 PILES	2

FOOTING TOP AT -1.500, 50 mm CLEAR COVER, 75 mm BLINDING BELOW

FOOTING SCHEDULE

F-RCC6 SAMPLE SIX-STOREY RCC RESIDENTIAL BUILDING
SHEET 6 OF 8 | A3 | ALL DIMENSIONS IN mm

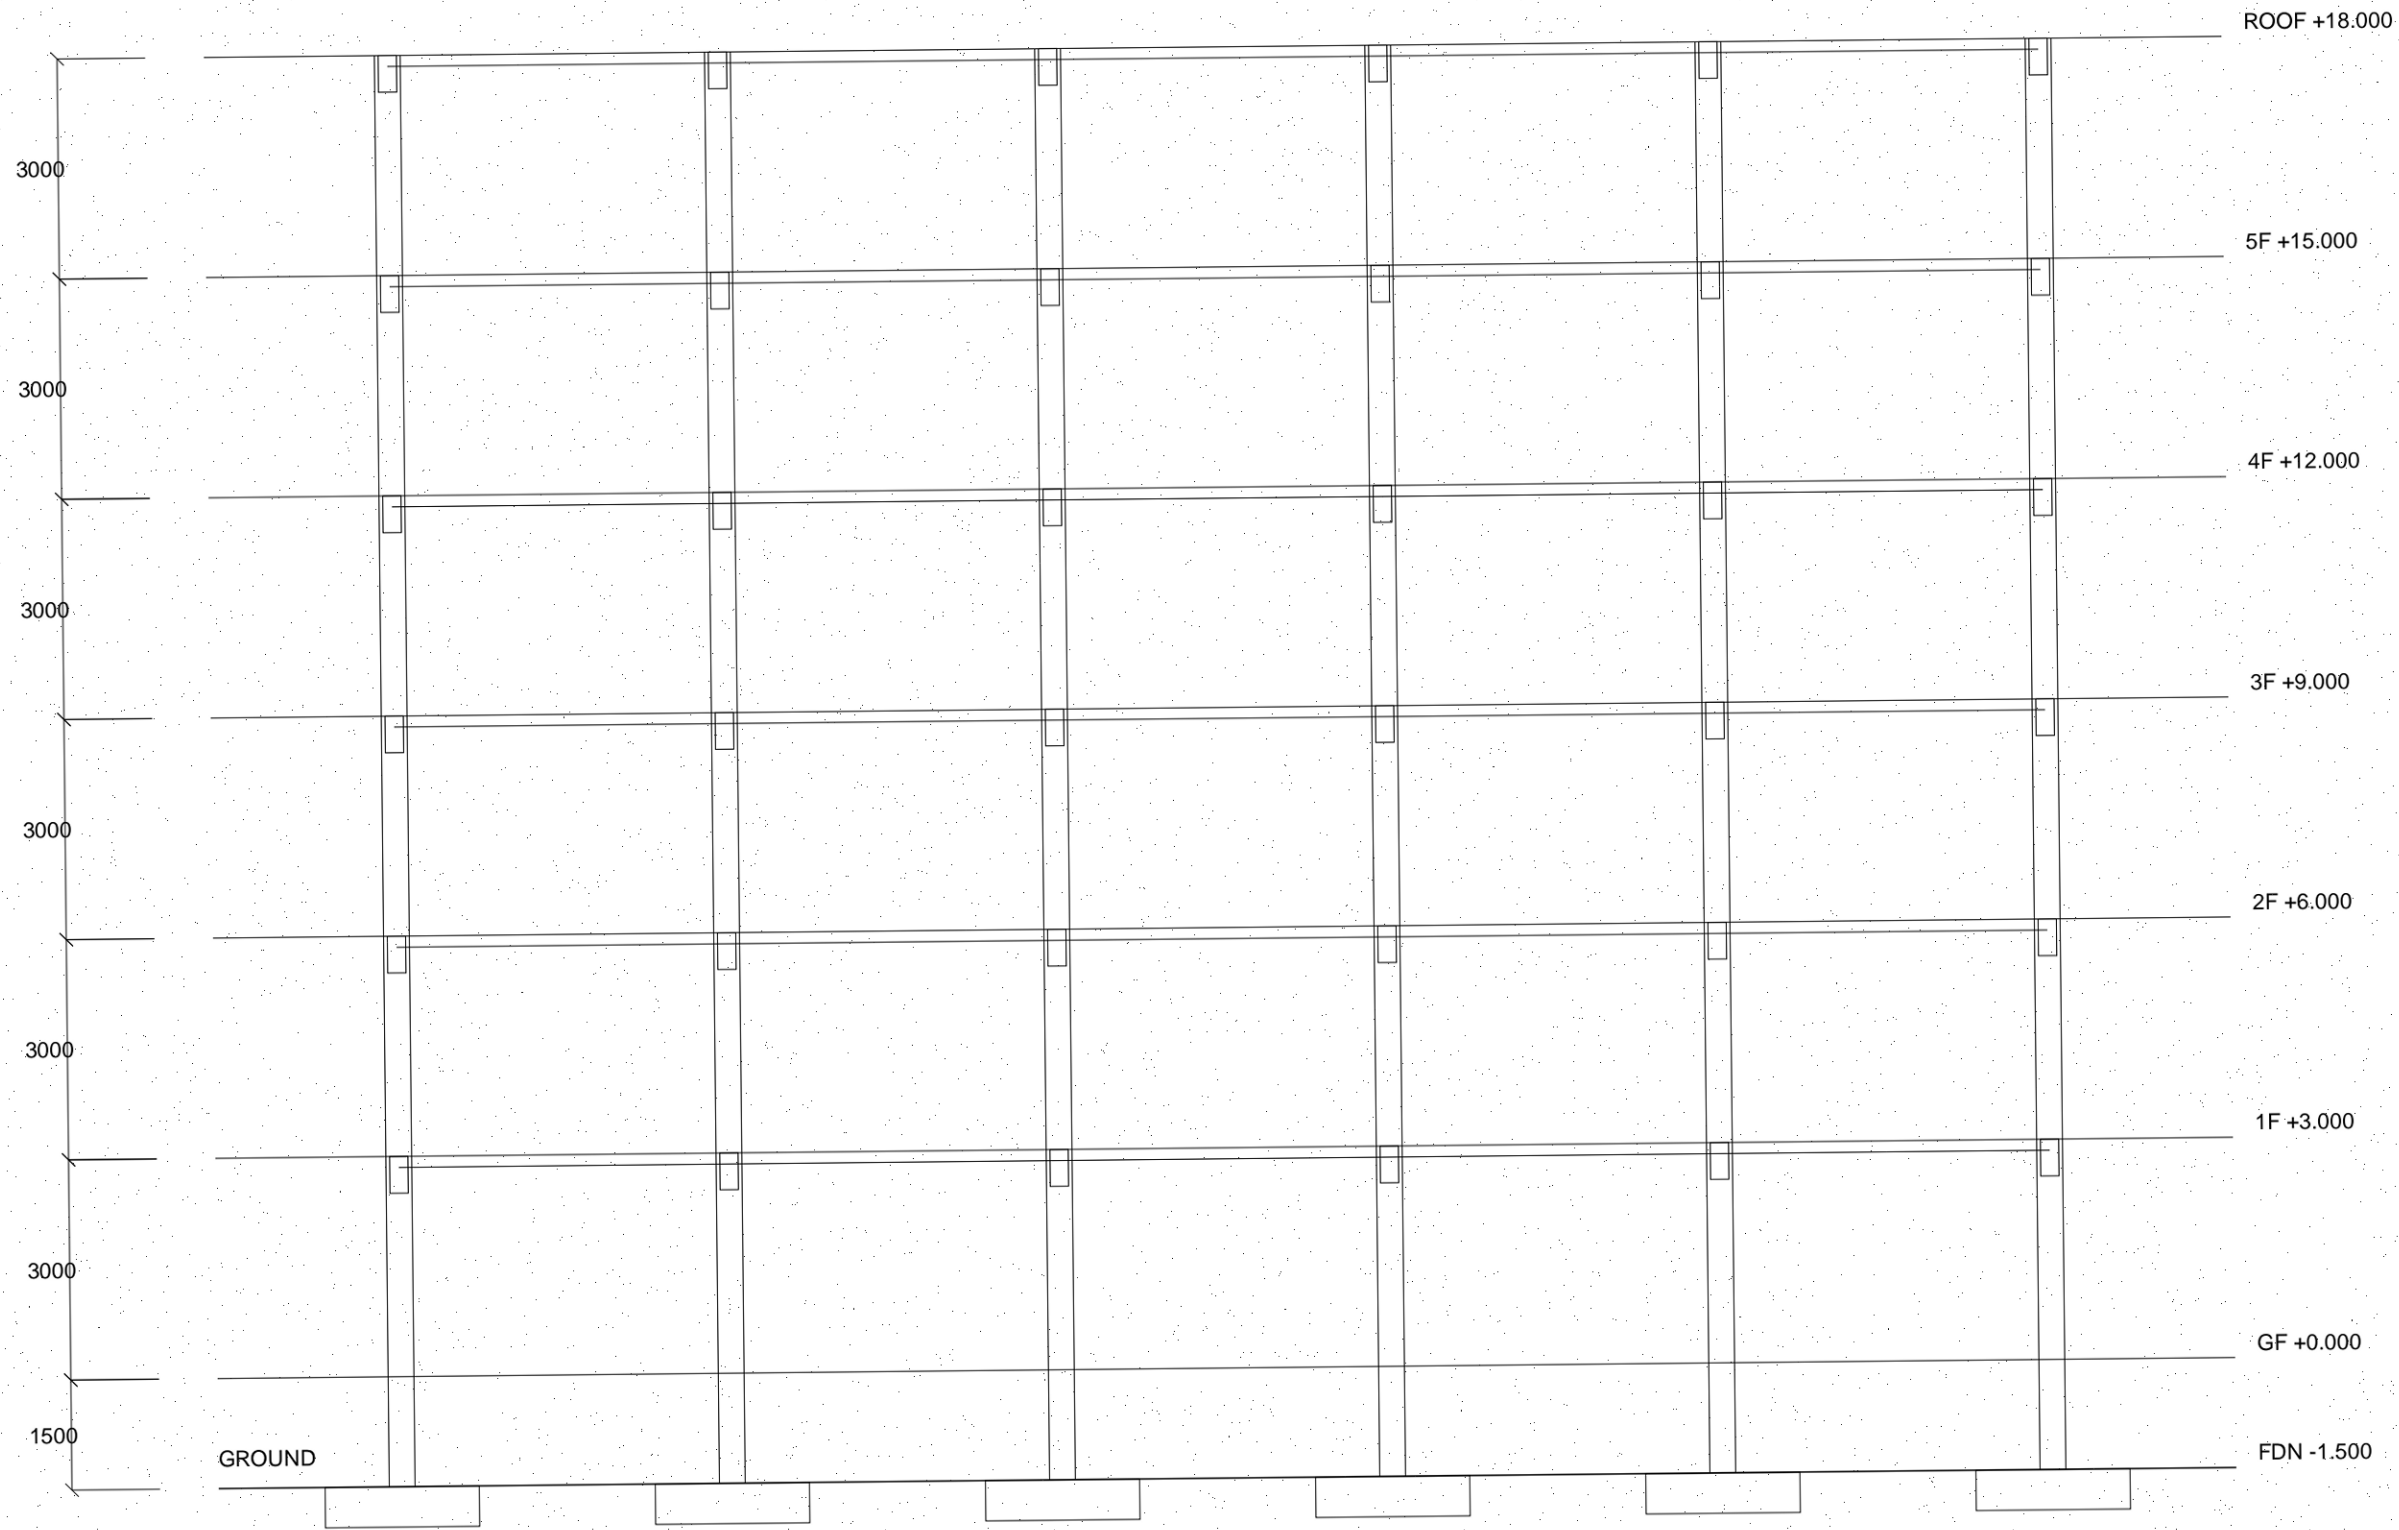

SECTION A-A

SECTIONS | STOREY HEIGHTS PER LEVEL STACK, SEE GENERAL NOTES

SECTIONS

F-RCC6 SAMPLE SIX-STOREY RCC RESIDENTIAL BUILDING

SHEET 7 OF 8 | A3 | ALL DIMENSIONS IN mm

GENERAL NOTES

1. CONCRETE
M25 FOR ALL RCC WORK ($f_{ck} = 25 \text{ N/mm}^2$). CEMENT OPC 43 GRADE.
MAXIMUM AGGREGATE 20 mm, SLUMP 75 TO 100 mm.
2. REINFORCEMENT
Fe500 HIGH YIELD DEFORMED BARS, $f_y = 500 \text{ N/mm}^2$.
BAR MARKS: T = Fe500.
3. CLEAR COVER
FOOTINGS AND PILE CAPS 50 mm, COLUMNS 40 mm, BEAMS 25 mm,
SLABS 20 mm.
4. LAPS
LAP LENGTH $50d$ FOR BARS IN TENSION, STAGGERED, NOT MORE THAN
50% OF BARS LAPPED AT ONE SECTION. NO LAPS AT BEAM-COLUMN JOINTS.
5. LEVELS
GF AT +0.000. FOOTING TOP AT -1.500. TYPICAL STOREY 3.000 m,
ROOF MACHINE ROOM 2.400 m.
6. DIMENSIONS
ALL DIMENSIONS IN mm UNLESS NOTED. LEVELS IN m. DO NOT SCALE.
GRID A TO F AND 1 TO 6 AS PLANS.

SIX-STOREY RCC RESIDENTIAL BUILDING

GENERAL NOTES

F-RCC6 SAMPLE SIX-STOREY RCC RESIDENTIAL BUILDING
SHEET 8 OF 8 | A3 | ALL DIMENSIONS IN mm