





# PROPOSED G+6 STORIED RESIDENTIAL BUILDING

PLOT 23, ROAD 7, BLOCK C, BASHUNDHARA R/A, DHAKA  
FOR M/S. PADMA HOMES LTD.  
RAJUK REF. RAJUK/BAP/2026/0417

## DRAWING INDEX

| SHEET | TITLE                                          | SIZE | SCALE       | REV |
|-------|------------------------------------------------|------|-------------|-----|
| S-00  | COVER, DRAWING INDEX & KEY PLAN                | A2   | N.T.S.      | B   |
| S-01  | GENERAL NOTES (1 OF 2)                         | A2   | N.T.S.      | B   |
| S-02  | GENERAL NOTES (2 OF 2) & LAP/DEVELOPMENT TABLE | A2   | N.T.S.      | B   |
| S-03  | TYPICAL REINFORCEMENT DETAILS                  | A2   | N.T.S.      | B   |
| S-04  | PILE LAYOUT PLAN                               | A1   | 1:100       | B   |
| S-05  | PILE DETAILS & PILE SCHEDULE                   | A2   | 1:20, 1:50  | B   |
| S-06  | PILE CAP LAYOUT & SCHEDULE                     | A1   | 1:100       | B   |
| S-07  | PILE CAP DETAILS                               | A2   | 1:25        | B   |
| S-08  | GRADE BEAM LAYOUT & GF SLAB-ON-GRADE           | A1   | 1:100       | B   |
| S-09  | GRADE BEAM DETAILS (LONG SECTIONS)             | A1   | 1:50        | B   |
| S-10  | COLUMN LAYOUT PLAN                             | A1   | 1:100       | B   |
| S-11  | COLUMN SCHEDULE                                | A1   | N.T.S.      | B   |
| S-12  | COLUMN DETAILS                                 | A2   | 1:20        | B   |
| S-13  | 1ST FLOOR BEAM LAYOUT                          | A1   | 1:100       | B   |
| S-14  | TYPICAL FLOOR BEAM LAYOUT (2ND TO 6TH FLOOR)   | A1   | 1:100       | B   |
| S-15  | ROOF & STAIR ROOF BEAM LAYOUT                  | A1   | 1:100       | B   |
| S-16  | BEAM DETAILS (1 OF 3) – 1ST FLOOR              | A1   | 1:50        | B   |
| S-17  | BEAM DETAILS (2 OF 3) – TYPICAL                | A1   | 1:50        | B   |
| S-18  | BEAM DETAILS (3 OF 3) – ROOF & SCHEDULE        | A1   | 1:50        | B   |
| S-19  | 1ST FLOOR SLAB REINFORCEMENT PLAN              | A1   | 1:100       | B   |
| S-20  | TYPICAL SLAB REINFORCEMENT PLAN                | A1   | 1:100       | B   |
| S-21  | ROOF, STAIR ROOF & PARAPET                     | A1   | 1:100, 1:20 | B   |
| S-22  | STAIR DETAILS                                  | A1   | 1:50, 1:20  | B   |
| S-23  | LIFT CORE & SHEAR WALL DETAILS                 | A1   | 1:50        | B   |
| S-24  | OVERHEAD WATER TANK & UGWR / SEPTIC TANK       | A1   | 1:50        | B   |
| S-25  | LINTEL & SUNSHADE SCHEDULE, BUILDING SECTION   | A1   | 1:100       | B   |
| S-26  | BAR BENDING SCHEDULE (SAMPLE: PC3, 2B7, SLAB S | A3   | N.T.S.      | B   |

## LOCATION MAP (N.T.S.)

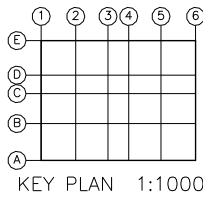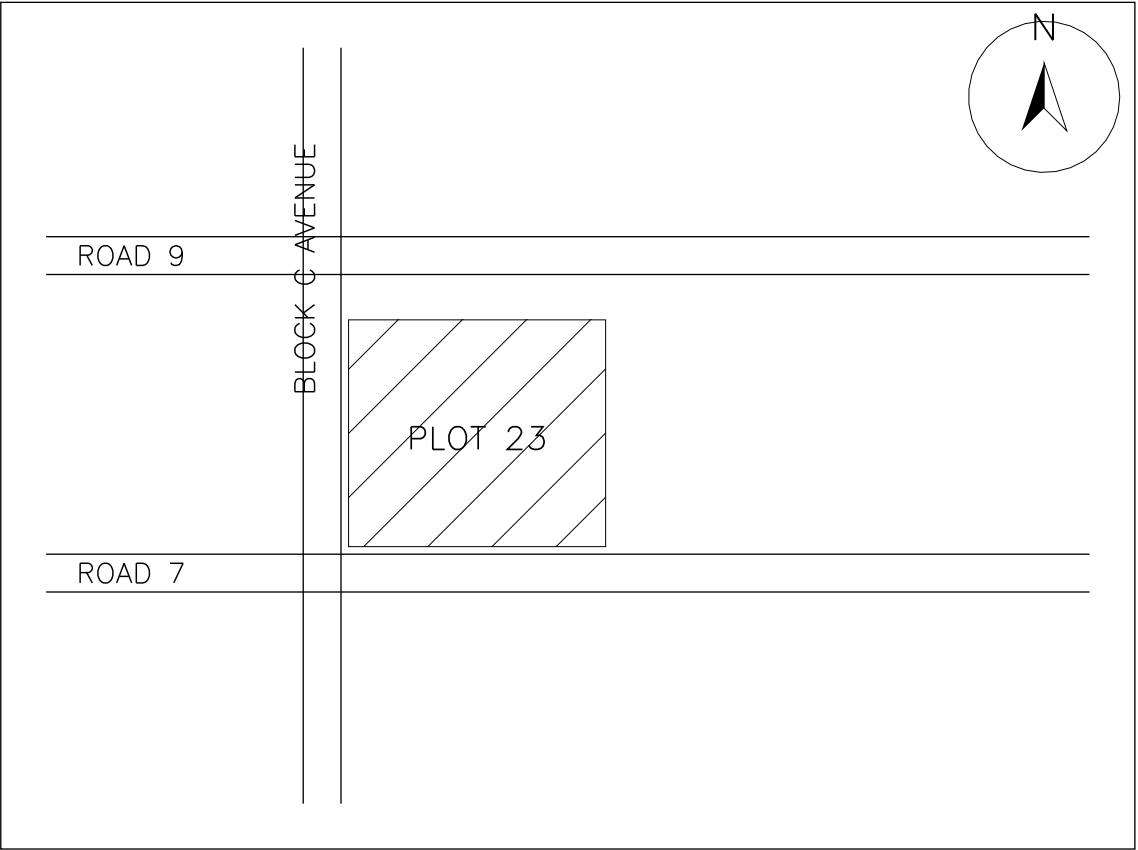

KEY PLAN 1:1000

MEGHNA STRUCTURAL CONSULTANTS LTD.  
FLAT 4B, HOUSE 27, ROAD 9, SECTOR 6, UTTARA MODEL TOWN, DHAKA  
TEL +880 1XXX 000 000 / +880 2 4890 0000

CLIENT  
M/S. PADMA HOMES LTD.

PROJECT  
PROPOSED G+6 STORIED RESIDENTIAL BUILDING

SITE  
PLOT 23, ROAD 7, BLOCK C, BASHUNDHARA R/A, DHAKA

SHEET TITLE  
COVER, DRAWING INDEX & KEY PLAN

DESIGNED  
S.R.

DRAWN  
M.H.

CHECKED  
A.K.

APPROVED  
T.I.

RAJUK REF. RAJUK/BAP/2026/0417

JOB NO. MSC-2026-041

DATE 12-08-2026

SCALE N.T.S.

SHEET NO.  
S-00

REV.  
B

REVISIONS

| REV | DATE       | DESCRIPTION                          |
|-----|------------|--------------------------------------|
| A   | 05-07-2026 | ISSUED FOR RAJUK APPROVAL            |
| B   | 12-08-2026 | EC4 3RD-4TH BARS REVISED; ISSUED FOR |

ALL DIMENSIONS IN mm U.N.O.  
DO NOT SCALE THIS DRAWING

GENERAL NOTES  
1. THESE DRAWINGS SHALL BE READ WITH THE ARCHITECTURAL AND MEP DRAWINGS. ANY DISCREPANCY SHALL BE REFERRED TO THE ENGINEER BEFORE WORK PROCEEDS.  
2. DESIGN CODE: BNBC 2020, ACI 318–19 WHERE THE CODE IS SILENT.  
3. IMPOSED LOAD 2.0 kN/m² (RESIDENTIAL), PARTITION 1.5 kN/m², FINISH 1.2 kN/m². BASIC WIND SPEED 65.7 m/s, SEISMIC ZONE 2 (Z=0.20).  
4. ALL DIMENSIONS ARE IN MILLIMETRES UNLESS FIGURED IN FEET AND INCHES. LEVELS ARE IN METRES ABOVE P.L.  
5. DO NOT SCALE THIS DRAWING – FIGURED DIMENSIONS GOVERN.

CONCRETE AND REINFORCEMENT  
6. CONCRETE: CYLINDER STRENGTH AT 28 DAYS AS NOTED BELOW. CEMENT CEM–I 52.5N. MAXIMUM AGGREGATE 20 mm, SLUMP 100 ± 25 mm.  
7. REINFORCEMENT: DEFORMED BARS TO BDS ISO 6935–2.  
8. BAR LETTERS: T AND Y BOTH MEAN A DEFORMED BAR OF THE DIAMETER THAT FOLLOWS (T16 = Y16 = 16Ø). A SECOND DRAUGHTSMAN'S SHEET MAY MIX THEM ON ONE LINE.  
9. LEGACY IMPERIAL BAR CALLS: #3 = 10Ø, #4 = 12Ø, #5 = 16Ø, #6 = 20Ø, #8 = 25Ø.  
10. WELDED HOOKS ARE NOT PERMITTED. ALL HOOKS 135° WHERE SHOWN ON S–03.

MATERIALS

f'c = 3500 psi (24 MPa) cylinder  
f'c = 3000 psi (BORED PILES)  
fy = 72,500 psi (500 MPa) BDS ISO 6935–2 B500DWR  
B500DWR  
CLEAR COVER

2" clear cover (pile caps) 25mm clear cover (beams) 40mm clear cover (columns) 20mm clear cover (slabs)

MEASUREMENT CONVENTIONS (AM–02 / AM–03)

COUNTING: L(distance + 0.5 mm)/spacingJ + 1  
CURVED BALCONY: the R 1524 curved balcony corner is measured as the true quarter–circle, not as the drawn polygon's corner point  
CUTTING LENGTH: BS 8666 per L–FRM–05 (bend radius 2d ≤16 mm else 3.5d; generic Σlegs – bends·(0.5r + d)); IS–additive printed beside, never billed  
HOOKS: 90° = 12d; stirrup/tie 135° = 10d, min 75 mm (S–03)

JUNCTION OWNERSHIP: pile > pile cap > column/shear wall (full floor–to–floor, through joints) > beam (clear between support faces, depth below the slab soffit) > slab (runs through; outline – column/wall plan areas – openings > 0.1 m²)  
JUNCTION OWNERSHIP: grade beams clear between cap faces; stair flights sloped length × width × waist + step triangles; landings AREA\_THICK  
JUNCTION OWNERSHIP: formwork: column 2(b+d) × (floor–to–floor – slab t) – beam–end contacts > 500 cm²; beam sides (D – t each side) + soffit b, × clear; slab soffit net of beam soffits and columns, free edges × t as EDGE; caps/GB/footing sides only; piles none; stair soffit + risers + strings  
JUNCTION OWNERSHIP: a junction deduction may defer only where the published figure is then under, never over (AM–02)

LAPS: tension 50d / compression 40d (S–02 general note overrides the BNBC table, J–032); columns and walls one lap per storey

MEMBER END NO DEDUCT CM2: 500

OPENING THRESHOLD M2: 0.1

RAMP: sloped area × thickness (plan × √(run² + rise²)/run)

REBAR UNIT: kg = cutting length (raw, unrounded) × table kg/m

ROUNDED CUTTING LENGTH MM: 25

STOCK MM: 12000

STOCK SPLIT: n = ⌈(L – lap)/(stock – lap)⌈, billable L + (n – 1)·lap; laps are the LAP component

SUNKEN SLAB: drop 300: slab 125 + drop walls 125 × 175 on the cut–out perimeter; formwork soffit + both drop faces

UNIT WEIGHTS: L–FRM–05 table (8→0.395, 10→0.616, 12→0.888, 16→1.579, 20→2.466, 25→3.854 kg/m); d²/162 is a check only

WASTAGE: imperial quantities 3% on binding wire 8 kg/t belong to resource summaries only (AM–03a)

MEGHNA STRUCTURAL CONSULTANTS LTD.  
FLAT 4B, HOUSE 27, ROAD 9, SECTOR 6, UTTARA MODEL TOWN, DHAKA 1215, BANGLADESH  
TEL +880 1XXX 000 000 / +880 2 4890 0000

CLIENT  
M/S. PADMA HOMES LTD.

PROJECT  
PROPOSED G+6 STORIED RESIDENTIAL BUILDING

SITE  
PLOT 23, ROAD 7, BLOCK C, BASHUNDHARA R/A, DHAKA

SHEET TITLE  
GENERAL NOTES (1 OF 2)

|          |       |         |          |
|----------|-------|---------|----------|
| DESIGNED | DRAWN | CHECKED | APPROVED |
| S.R.     | M.H.  | A.K.    | T.I.     |

RAJUK REF. RAJUK/BAP/2026/0417

JOB NO. MSC–2026–041

DATE 12–08–2026

SCALE N.T.S.

|           |      |
|-----------|------|
| SHEET NO. | REV. |
| S–01      | B    |

REVISIONS

| REV | DATE       | DESCRIPTION                         |
|-----|------------|-------------------------------------|
| A   | 05–07–2026 | ISSUED FOR RAJUK APPROVAL           |
| B   | 12–08–2026 | C4 3RD–4TH BARS REVISED; ISSUED FOR |

ALL DIMENSIONS IN mm U.N.O.  
DO NOT SCALE THIS DRAWING

DO NOT SCALE

DETAILING NOTES  
11. LAPS SHALL BE STAGGERED; NOT MORE THAN 50% OF BARS MAY BE LAPPED AT ONE SECTION. NO LAP WITHIN A BEAM–COLUMN JOINT.  
12. TOP BARS OVER SUPPORTS SHALL EXTEND L/4 EACH SIDE OF THE SUPPORT FACE, BOTTOM BARS L/5, UNLESS THE LONG SECTION SHOWS OTHERWISE.  
13. STIRRUP ZONES: 2D FROM EACH SUPPORT FACE AT THE CLOSE SPACING, THE MIDDLE AT THE WIDE SPACING.  
14. CHAIRS AT 1.0 m c/c BOTH WAYS IN EVERY DOUBLE–LAYER SLAB AND RAFT.

LAP 50d TENSION / 40d COMPRESSION U.N.O.  
(THIS NOTE GOVERNS OVER THE CODE TABLE)

DEVELOPMENT LENGTH  $l_d$  –  $f_y$  500 MPa,  $f'_c$  3500 psi

| BAR | $l_d$ BOTTOM (mm) | $l_d$ TOP (mm) | LAP TENSION (mm) | LAP COMPRESSION (mm) |
|-----|-------------------|----------------|------------------|----------------------|
| 8Ø  | 400               | 520            | 400              | 320                  |
| 10Ø | 500               | 650            | 500              | 400                  |
| 12Ø | 600               | 780            | 600              | 480                  |
| 16Ø | 800               | 1040           | 800              | 640                  |
| 20Ø | 1000              | 1300           | 1000             | 800                  |
| 25Ø | 1250              | 1625           | 1250             | 1000                 |

BAR BENDING TO BS 8666; THE IS ADDITIVE FIGURE IS PRINTED BESIDE IT ON S–26.

MEGHNA STRUCTURAL CONSULTANTS LTD.  
FLAT 4B, HOUSE 27, ROAD 9, SECTOR 6, UTTARA MODEL TOWN, DHAKA 1215  
TEL +880 1XXX 000 000 / +880 2 4890 0000

CLIENT  
M/S. PADMA HOMES LTD.

PROJECT  
PROPOSED G+6 STORIED RESIDENTIAL BUILDING

SITE  
PLOT 23, ROAD 7, BLOCK C, BASHUNDHARA R/A, DHAKA

SHEET TITLE  
GENERAL NOTES (2 OF 2) & LAP/DEVELOPMENT TABLE

DESIGNED  
S.R.

DRAWN  
M.H.

CHECKED  
A.K.

APPROVED  
T.I.

RAJUK REF. RAJUK/BAP/2026/0417

JOB NO. MSC–2026–041

DATE 12–08–2026

SCALE N.T.S.

SHEET NO.  
S–02


REV.  
B

REVISIONS


| REV | DATE       | DESCRIPTION                         |
|-----|------------|-------------------------------------|
| A   | 05–07–2026 | ISSUED FOR RAJUK APPROVAL           |
| B   | 12–08–2026 | C4 3RD–4TH BARS REVISED; ISSUED FOR |

ALL DIMENSIONS IN mm U.N.O.  
DO NOT SCALE THIS DRAWING



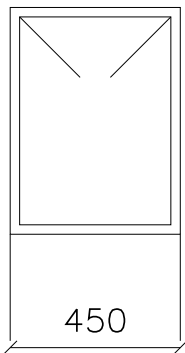

135° HOOK, 10d  
TYPICAL STIRRUP  
10Ø @ 100 c/c

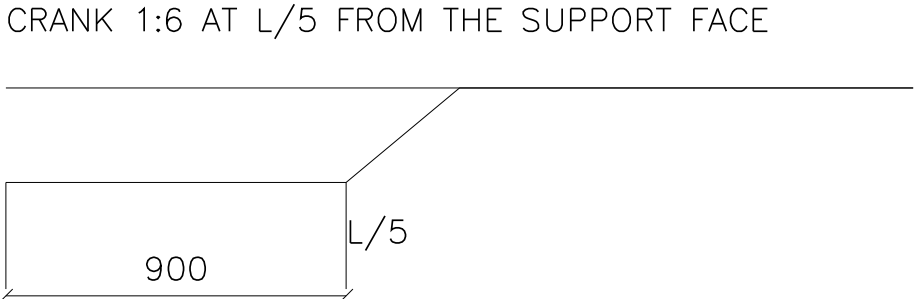


CRANK 1:6 AT L/5 FROM THE SUPPORT FACE

BS 8006 SHAPE CODES US



SHAPE 21  
A + B + C

 

SHAPE 51  
2(A+B) + 2C - 2



SHAPE 11  
A + (B) hook




SHAPE 00  
A straight


TYPICAL STIRRUP HOOK DETAIL SCALE 1:20TYPICAL SLAB BAR CRANK SCALE 1:20

BAR SHAPE CODES SCALE 1:25


|   |               |                                      |                  |
|---|---------------|--------------------------------------|------------------|
| MEGHNA STRUCTURAL CONSULTANTS LTD.<br>FLAT 4B, HOUSE 27, ROAD 9, SECTOR 6, UTTARA MODEL TOWN, DHAKA<br>TEL +880 1XXX 000 000 / +880 2 4890 0000 |               |                                      |                  |
| CLIENT<br>M/S. PADMA HOMES LTD.   |               |                                      |                  |
| PROJECT<br>PROPOSED G+6 STORIED RESIDENTIAL BUILDING                                                                                            |               |                                      |                  |
| SITE<br>PLOT 23, ROAD 7, BLOCK C, BASHUNDHARA R/A, DHAKA                                                                                        |               |                                      |                  |
| SHEET TITLE<br>TYPICAL REINFORCEMENT DETAILS   |               |                                      |                  |
| DESIGNED<br>S.R.   | DRAWN<br>M.H. | CHECKED<br>A.K.                      | APPROVED<br>T.I. |
| RAJUK REF.   |               | RAJUK/BAP/2026/0417                  |                  |
| JOB NO.   |               | MSC-2026-041                         |                  |
| DATE   |               | 12-08-2026                           |                  |
| SCALE   |               | N.T.S.                               |                  |
| SHEET NO.<br>S-03   |               | REV.<br>B                            |                  |
| REVISIONS   |               |                                      |                  |
| REV   | DATE          | DESCRIPTION                          |                  |
| A   | 05-07-2026    | ISSUED FOR RAJUK APPROVAL            |                  |
| B   | 12-08-2026    | EC4 3RD-4TH BARS REVISED; ISSUED FOR |                  |
| ALL DIMENSIONS IN mm U.N.O.<br>DO NOT SCALE THIS DRAWING                                                                                        |               |                                      |                  |

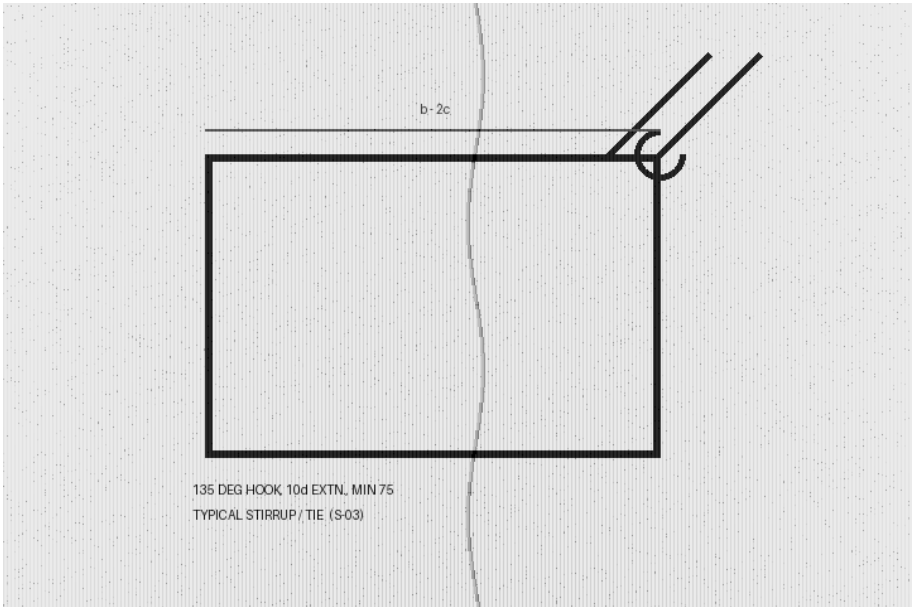

HOOK 135° = 10d, MIN 75 mm; 90° = 12d

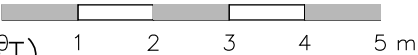

PASTED DETAIL – HOOK (SCANNED FROM THE STANDARD SHEET)

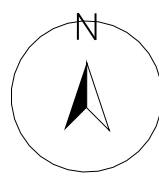

MEGHNA STRUCTURAL CONSULTANT  
S. LTD.  
FLAT 4B, HOUSE 27, ROAD 9, SECTOR 6, UTTARA MODEL TOWN, DHAKA  
TEL: +880 1XXXX 000 000 / +880 2 4890 0000


CLIENT  
M/S. PADMA HOMES LTD.

PROJECT  
PROPOSED G+6 STORIED RESIDENTIAL BUILDING

SITE  
PLOT 23, ROAD 7, BLOCK C, BASHUNDHARA R/A, DHAKA

SHEET TITLE  
PILE LAYOUT PLAN

|                                |            |                                     |          |
|--------------------------------|------------|-------------------------------------|----------|
| DESIGNED                       | DRAWN      | CHECKED                             | APPROVED |
| S.R.                           | M.H.       | A.K.                                | T.I.     |
| RAJUK REF. RAJUK/BAP/2026/0417 |            |                                     |          |
| JOB NO. MSC-2026-041           |            |                                     |          |
| DATE 12-08-2026                |            |                                     |          |
| SCALE 1:100                    |            |                                     |          |
| SHEET NO. S-04                 |            |                                     | REV. B   |
| REVISIONS                      |            |                                     |          |
| REV.                           | DATE       | DESCRIPTION                         |          |
| A                              | 05-07-2026 | ISSUED FOR RAJUK APPROVAL           |          |
| B                              | 12-08-2026 | C4 3RD-4TH BARS REVISED; ISSUED FOR |          |

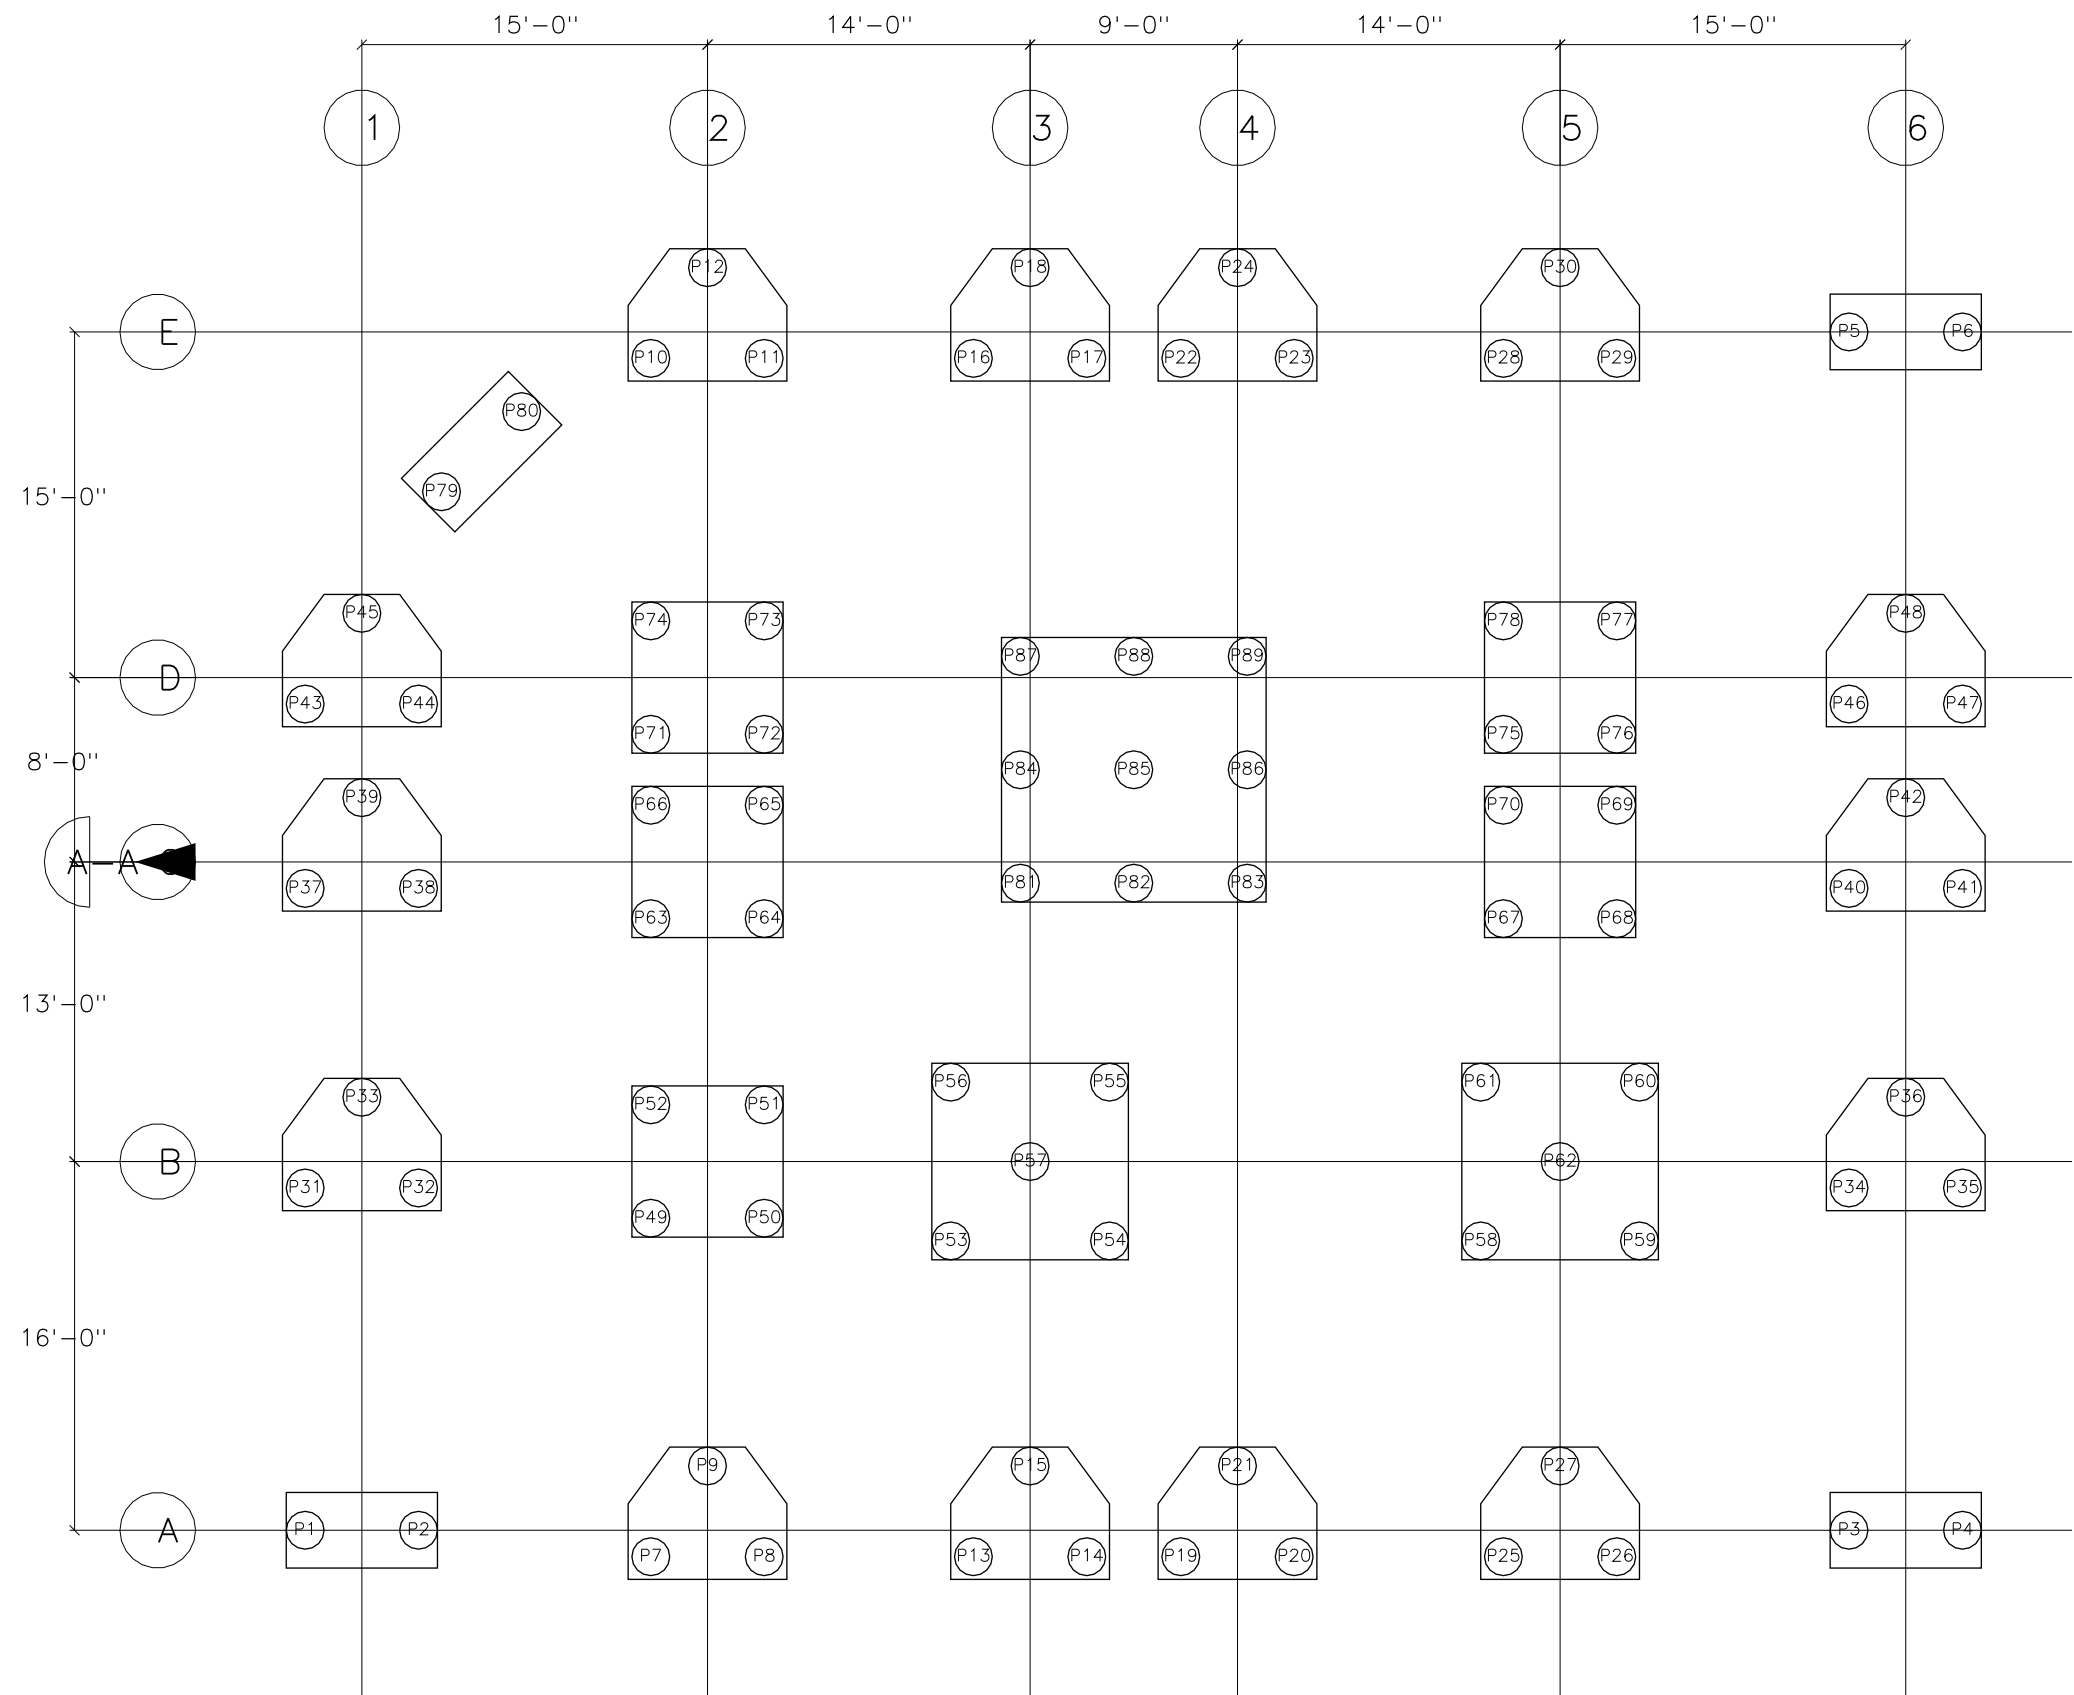


89 NOS. Ø500 BORED PILES, TOE AT EL -23.165

PILE LAYOUT PLAN SCALE 1:100


PILE SET-OUT TABLE - COORDINATES FROM GRID 1 / GRID A

| PILE | X (mm) | Y (mm) | PILE | X (mm) | Y (mm) | PILE | X (mm) | Y (mm) |
|------|--------|--------|------|--------|--------|------|--------|--------|
| P1   | -750   | 0      | P31  | -750   | 4527   | P61  | 14800  | 5927   |
| P2   | 750    | 0      | P32  | 750    | 4527   | P62  | 15850  | 4877   |
| P3   | 19672  | 0      | P33  | 0      | 5727   | P63  | 3822   | 8089   |
| P4   | 21172  | 0      | P34  | 19672  | 4527   | P64  | 5322   | 8089   |
| P5   | 19672  | 15850  | P35  | 21172  | 4527   | P65  | 5322   | 9589   |
| P6   | 21172  | 15850  | P36  | 20422  | 5727   | P66  | 3822   | 9589   |
| P7   | 3822   | -350   | P37  | -750   | 8489   | P67  | 15100  | 8089   |
| P8   | 5322   | -350   | P38  | 750    | 8489   | P68  | 16600  | 8089   |
| P9   | 4572   | 850    | P39  | 0      | 9689   | P69  | 16600  | 9589   |
| P10  | 3822   | 15500  | P40  | 19672  | 8489   | P70  | 15100  | 9589   |
| P11  | 5322   | 15500  | P41  | 21172  | 8489   | P71  | 3822   | 10528  |
| P12  | 4572   | 16700  | P42  | 20422  | 9689   | P72  | 5322   | 10528  |
| P13  | 8089   | -350   | P43  | -750   | 10928  | P73  | 5322   | 12028  |
| P14  | 9589   | -350   | P44  | 750    | 10928  | P74  | 3822   | 12028  |
| P15  | 8839   | 850    | P45  | 0      | 12128  | P75  | 15100  | 10528  |
| P16  | 8089   | 15500  | P46  | 19672  | 10928  | P76  | 16600  | 10528  |
| P17  | 9589   | 15500  | P47  | 21172  | 10928  | P77  | 16600  | 12028  |
| P18  | 8839   | 16700  | P48  | 20422  | 12128  | P78  | 15100  | 12028  |
| P19  | 10832  | -350   | P49  | 3822   | 4127   | P79  | 1053   | 13736  |
| P20  | 12332  | -350   | P50  | 5322   | 4127   | P80  | 2114   | 14796  |
| P21  | 11582  | 850    | P51  | 5322   | 5627   | P81  | 8711   | 8558   |
| P22  | 10832  | 15500  | P52  | 3822   | 5627   | P82  | 10211  | 8558   |
| P23  | 12332  | 15500  | P53  | 7789   | 3827   | P83  | 11711  | 8558   |
| P24  | 11582  | 16700  | P54  | 9889   | 3827   | P84  | 8711   | 10058  |
| P25  | 15100  | -350   | P55  | 9889   | 5927   | P85  | 10211  | 10058  |
| P26  | 16600  | -350   | P56  | 7789   | 5927   | P86  | 11711  | 10058  |
| P27  | 15850  | 850    | P57  | 8839   | 4877   | P87  | 8711   | 11558  |
| P28  | 15100  | 15500  | P58  | 14800  | 3827   | P88  | 10211  | 11558  |
| P29  | 16600  | 15500  | P59  | 16900  | 3827   | P89  | 11711  | 11558  |
| P30  | 15850  | 16700  | P60  | 16900  | 5927   |      |        |        |

PILE SET-OUT TABLE SCALE 1:100

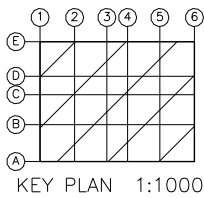



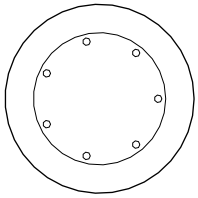

4-200 FUL  
3-200 CUI

500

PILE SECTION    SCALE 1:20

BORED CAST-IN-SITU PILES, f'c = 3000 psi

| MARK | DIA (mm) | LENGTH (mm) | MAIN BARS     | SPIRAL       | NOS |
|------|----------|-------------|---------------|--------------|-----|
| P    | 500      | 21336       | 4-200 + 3-200 | 100 @ 75/150 | 1   |

PILE SCHEDULE    SCALE 1:50


EL -1.829

100 spiral @ 75mm c/c

PILE LENGTH 21336

CURTAILED AT 12000 FRC

PILE CURTAILMENT & SPIRAL ZONES    SCALE 1:100

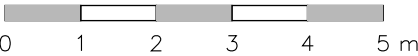

MEGHNA STRUCTURAL CONSULTANTS LTD.  
FLAT 4B, HOUSE 27, ROAD 9, SECTOR 6, UTTARA MODEL TOWN, DHAKA  
TEL +880 1XXX 000 000 / +880 2 4890 0000

CLIENT  
M/S. PADMA HOMES LTD.

PROJECT  
PROPOSED G+6 STORIED RESIDENTIAL BUILDING

SITE  
PLOT 23, ROAD 7, BLOCK C, BASHUNDHARA R/A, DHAKA

SHEET TITLE  
PILE DETAILS & PILE SCHEDULE

DESIGNED  
S.R.

DRAWN  
M.H.

CHECKED  
A.K.

APPROVED  
T.I.

RAJUK REF. RAJUK/BAP/2026/0417

JOB NO. MSC-2026-041

DATE 12-08-2026

SCALE 1:20, 1:50


SHEET NO.  
S-05

REV.  
B


REVISIONS

| REV | DATE       | DESCRIPTION                          |
|-----|------------|--------------------------------------|
| A   | 05-07-2026 | ISSUED FOR RAJUK APPROVAL            |
| B   | 12-08-2026 | EC4 3RD-4TH BARS REVISED; ISSUED FOR |

ALL DIMENSIONS IN mm U.N.O.  
DO NOT SCALE THIS DRAWING

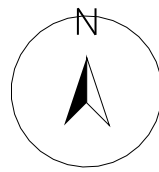

|   |               |                                      |                  |
|---|---------------|--------------------------------------|------------------|
| MEGHNA STRUCTURAL CONSULTANT<br>S. LTD.<br>FLAT 4B, HOUSE 27, ROAD 9, SECTOR 6, UTTARA MODEL TOWN<br>TEL: +880 1XXX 000 000 / +880 2 4890 0000 |               |                                      |                  |
| CLIENT<br>M/S. PADMA HOMES LTD.   |               |                                      |                  |
| PROJECT<br>PROPOSED G+6 STORIED RESIDENTIAL BUILDING                                                                                           |               |                                      |                  |
| SITE<br>PLOT 23, ROAD 7, BLOCK C, BASHUNDHARA R/A, DHAKA                                                                                       |               |                                      |                  |
| SHEET TITLE<br>PILE CAP LAYOUT & SCHEDULE   |               |                                      |                  |
| DESIGNED<br>S.R.   | DRAWN<br>M.H. | CHECKED<br>A.K.                      | APPROVED<br>T.I. |
| RAJUK REF. RAJUK/BAP/2026/0417   |               |                                      |                  |
| JOB NO. MSC-2026-041   |               |                                      |                  |
| DATE 12-08-2026   |               |                                      |                  |
| SCALE 1:100   |               |                                      |                  |
| SHEET NO.<br>S-06   |               | REV.<br>B                            |                  |
| REVISIONS   |               |                                      |                  |
| REV   | DATE          | DESCRIPTION                          |                  |
| A   | 05-07-2026    | ISSUED FOR RAJUK APPROVAL            |                  |
| B   | 12-08-2026    | PC4 3RD-4TH BARS REVISED; ISSUED FOR |                  |

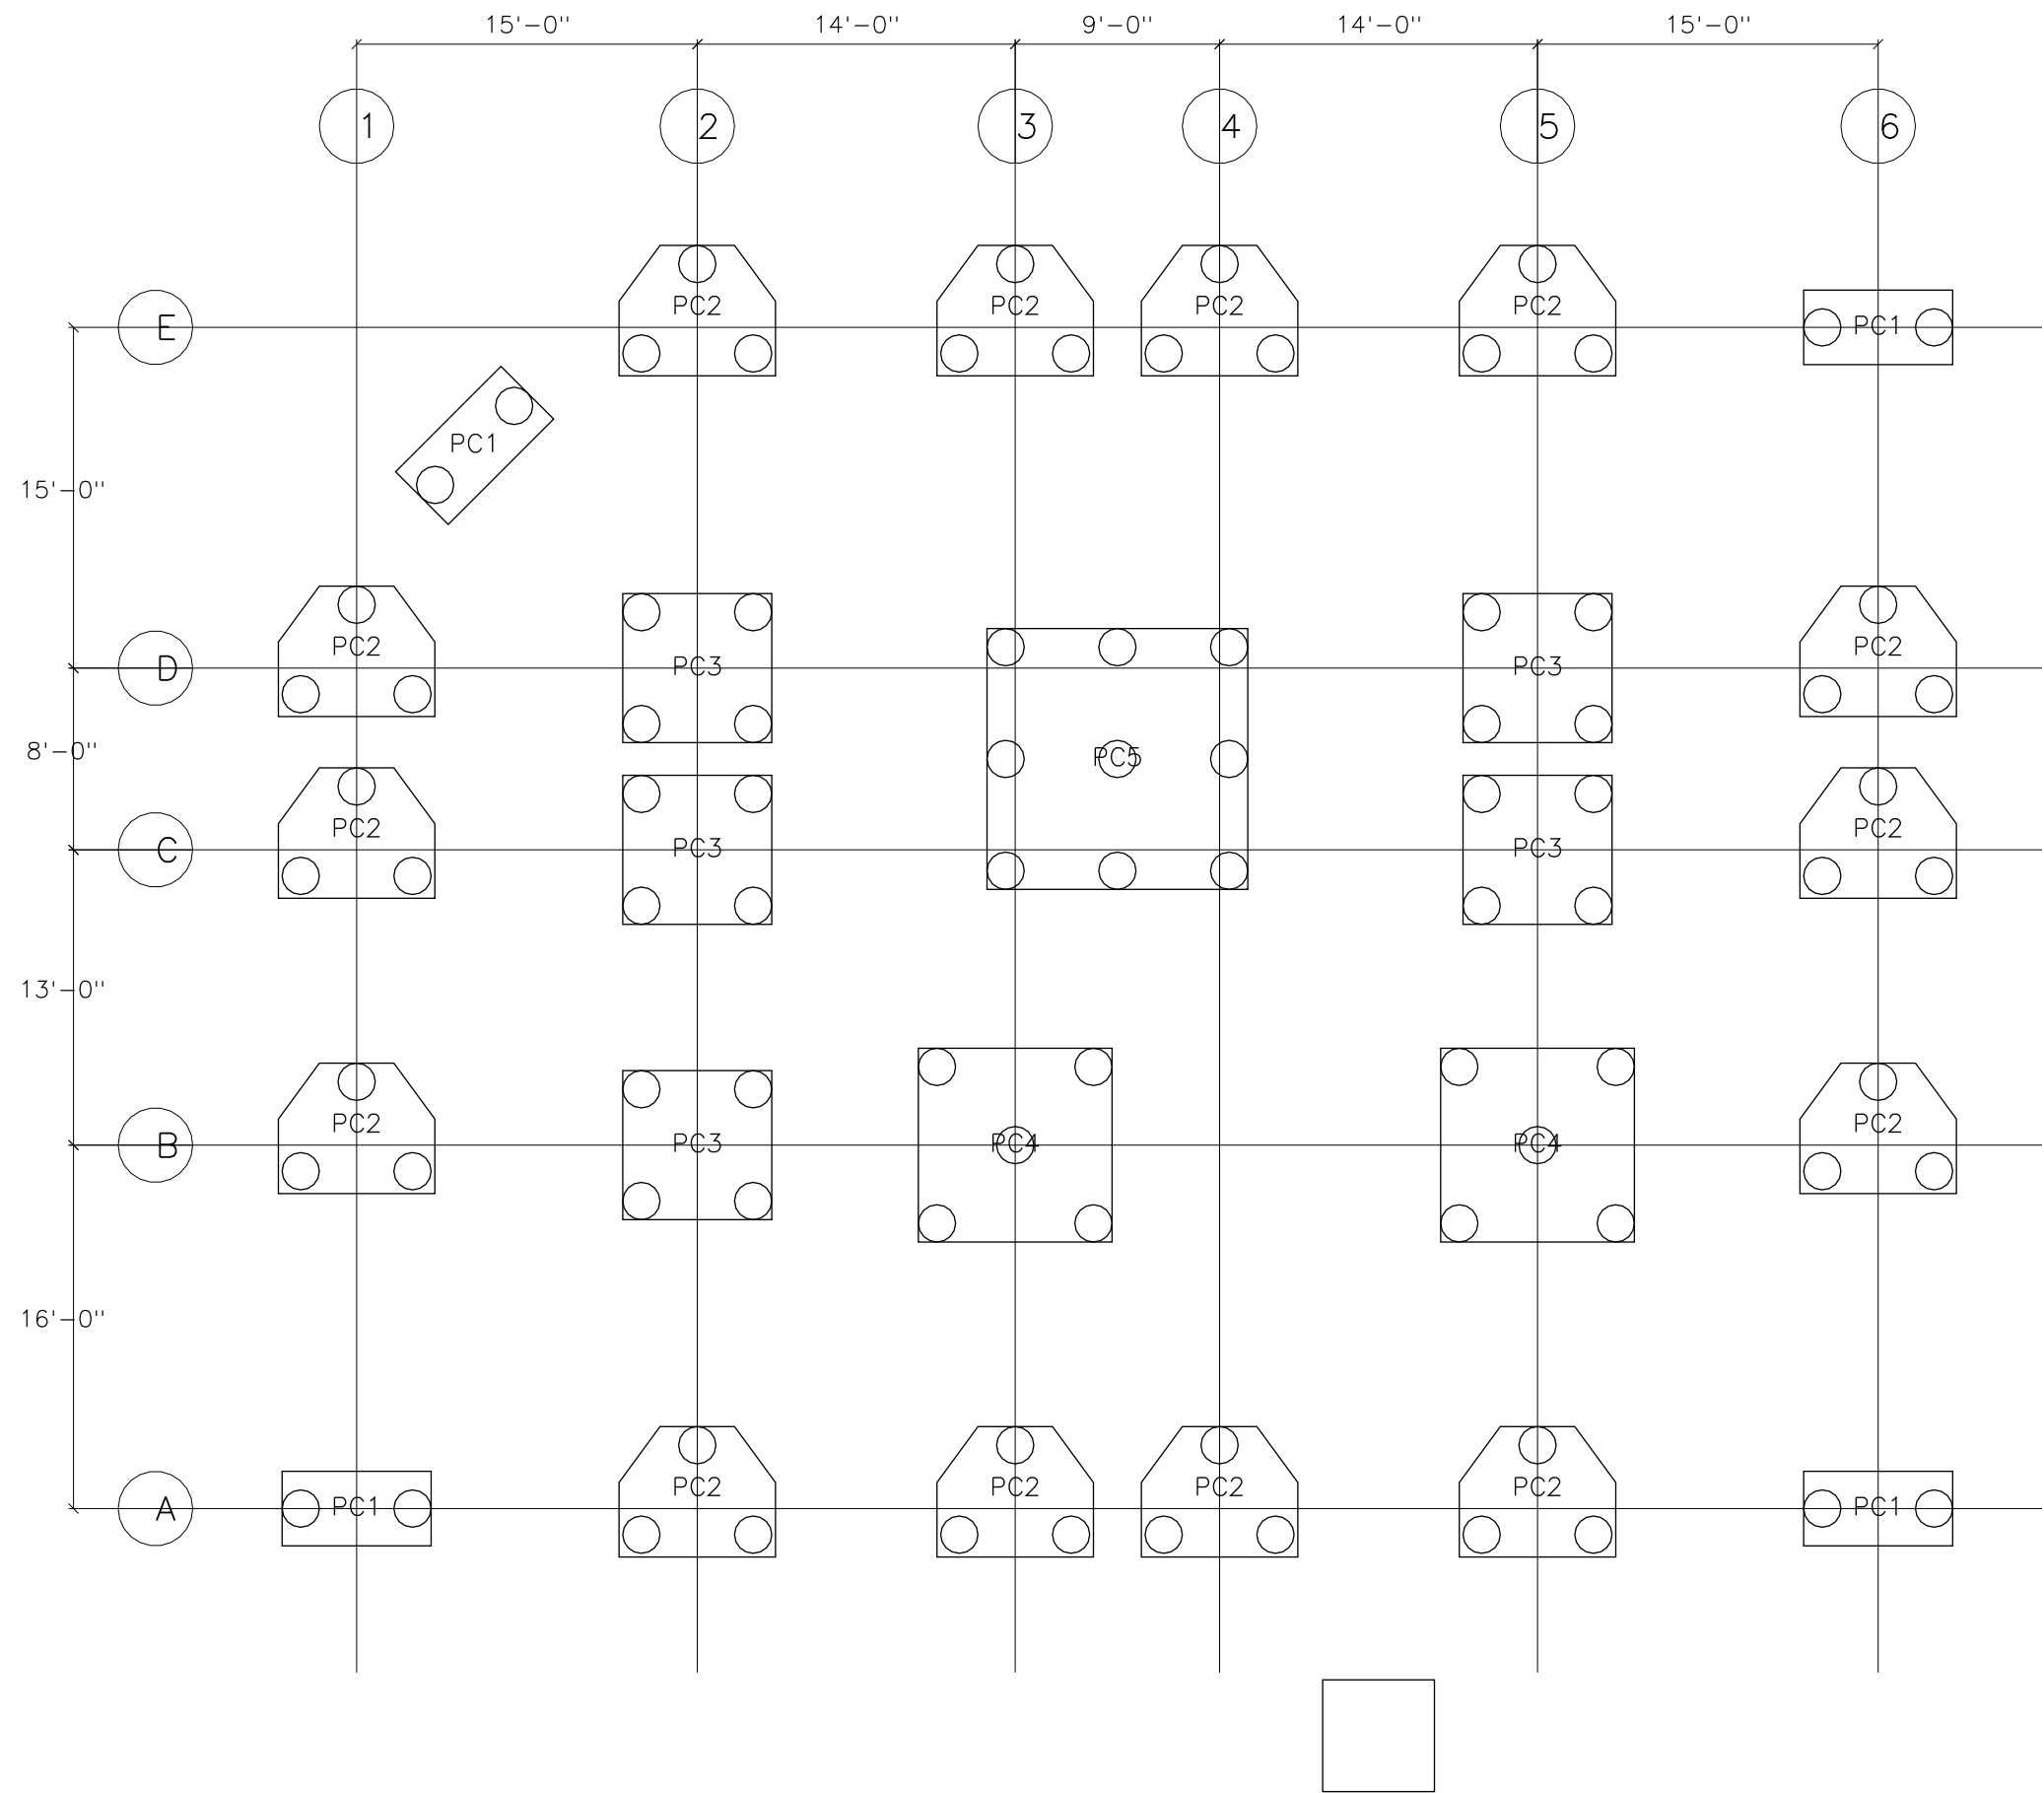



PILE CAP LAYOUT SCALE 1:100

PILE CAP SCHEDULE  
MARK SIZE DEPTH PILES BOTTOM MESH TOP MESH

|     |           |      |   |               |     |
|-----|-----------|------|---|---------------|-----|
| PC1 | 2000x1000 | 1295 | 2 | 16Ø @ 150 B/W | 12Ø |
| PC2 | 2100x1750 | 1295 | 3 | 16Ø @ 150 B/W | 12Ø |
| PC3 | 2000x2000 | 1295 | 4 | 16Ø @ 125 B/W | 12Ø |
| PC4 | 2600x2600 | 1295 | 5 | 20Ø @ 125 B/W | 12Ø |
| PC5 | 3500x3500 | 1295 | 9 | 20Ø @ 125 B/W | 16Ø |


COUNTS ARE TAKEN FROM THE LAYOUT ABOVE  
THIS OFFICE PRINTS NO NOS COLUMN

PILE CAP SCHEDULE SCALE 1:50

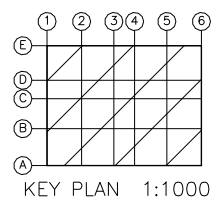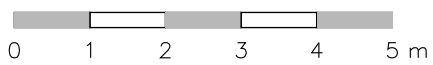




PC1

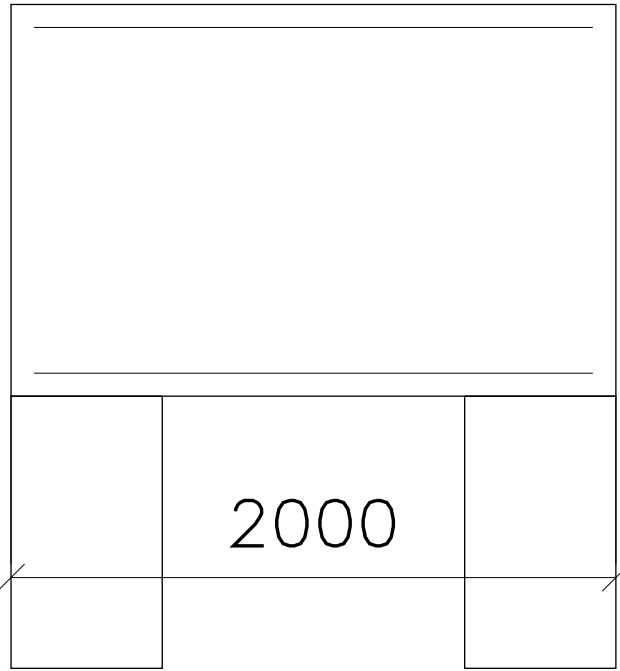

16Ø @ 150 B.W.


PC1 SECTION SCALE 1:25

PC2

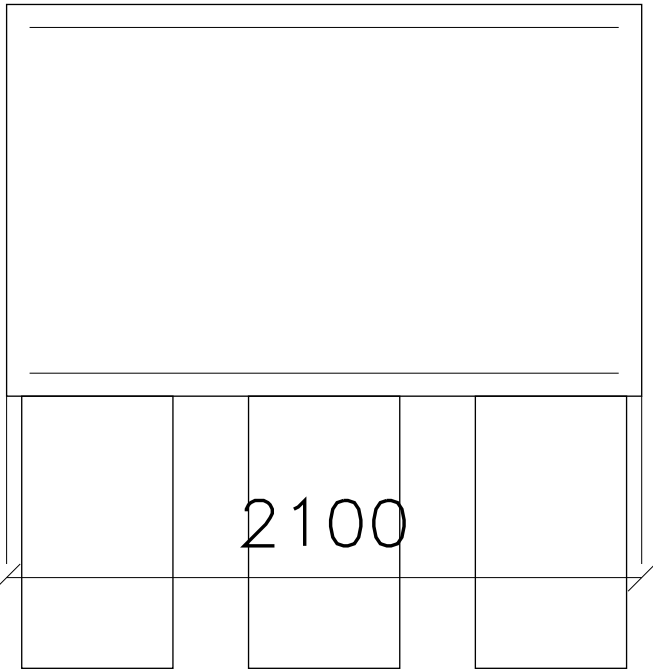

16Ø @ 150 B.W.


PC2 SECTION SCALE 1:25

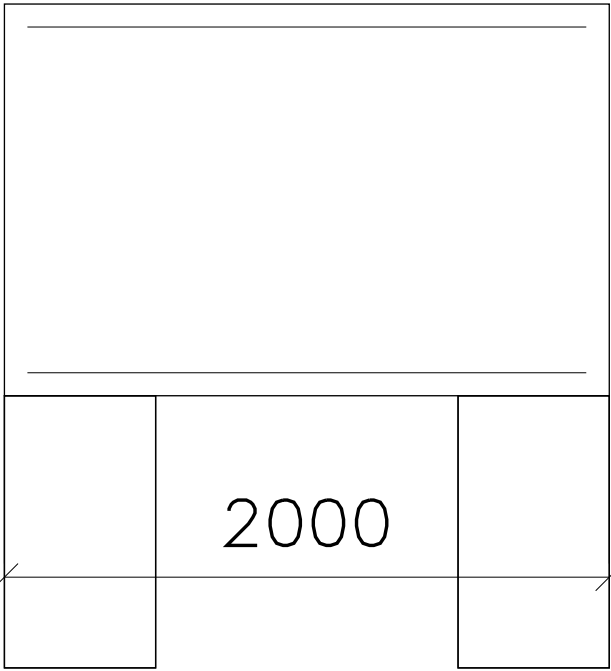

#5 @ 6" c/c B.W.

PC3 SECTION SCALE 1:25


PC4

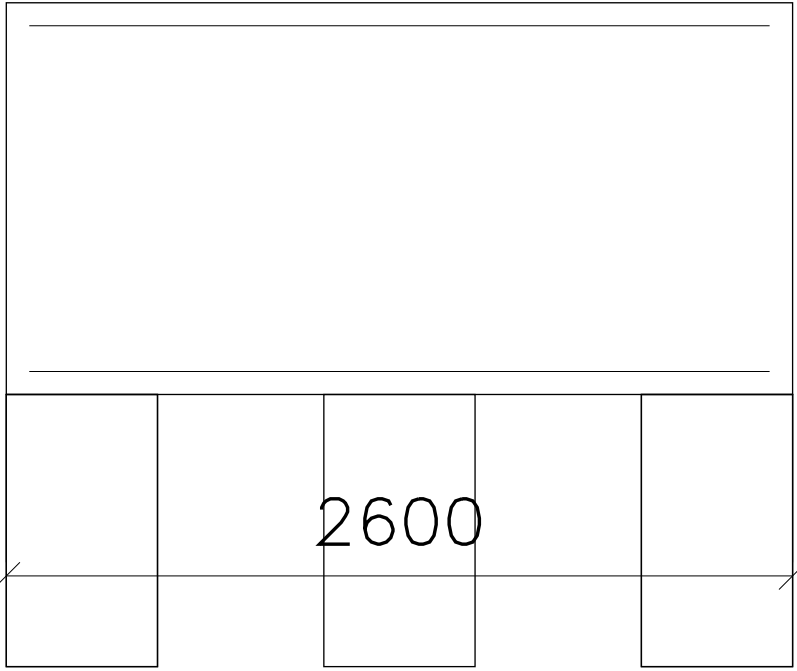

20Ø @ 125 B.W.

PC4 SECTION SCALE 1:25


PC5

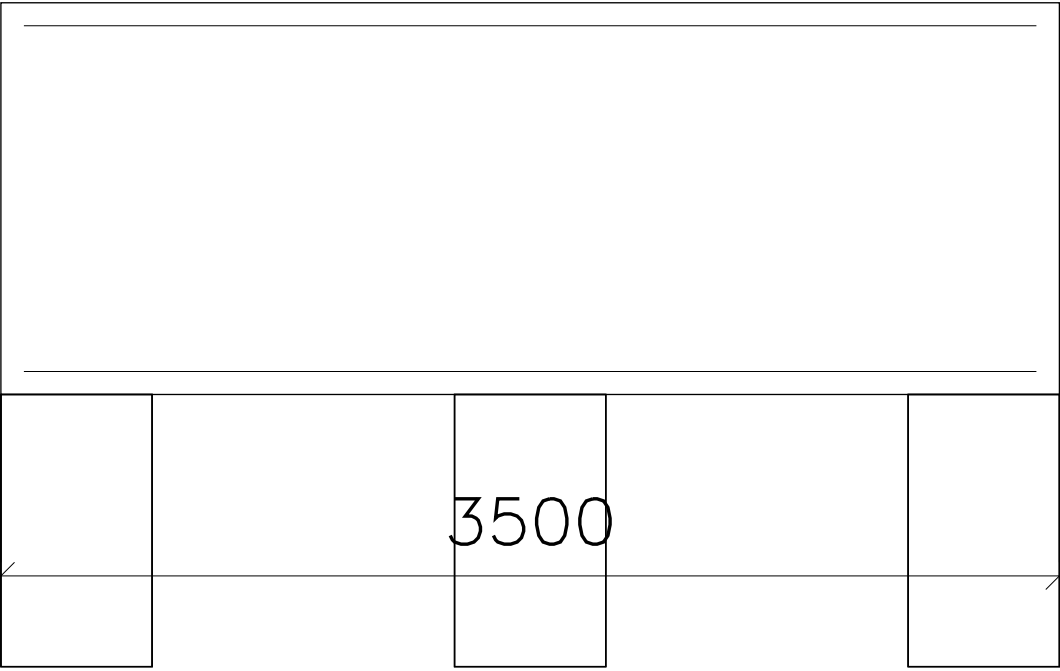

20Ø @ 125 B.W.

PC5 SECTION SCALE 1:25

F1

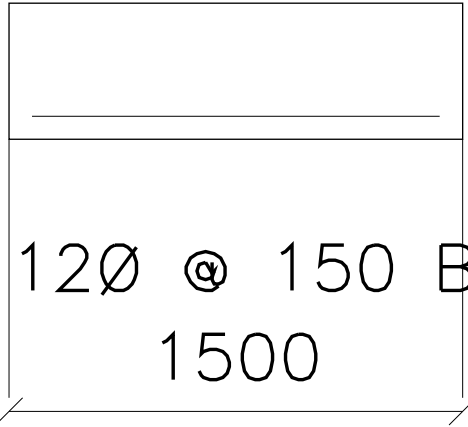


F1 ISOLATED FOOTING (RAMP WALL) SCALE 1:25

|   |               |                                      |                  |
|---|---------------|--------------------------------------|------------------|
| MEGHNA STRUCTURAL CONSULTANTS LTD.<br>FLAT 4B, HOUSE 27, ROAD 9, SECTOR 6, UTTARA MODEL TOWN, DHAKA<br>TEL +880 1XXX 000 000 / +880 2 4890 0000 |               |                                      |                  |
| CLIENT<br>M/S. PADMA HOMES LTD.   |               |                                      |                  |
| PROJECT<br>PROPOSED G+6 STORIED RESIDENTIAL BUILDING                                                                                            |               |                                      |                  |
| SITE<br>PLOT 23, ROAD 7, BLOCK C, BASHUNDHARA R/A, DHAKA                                                                                        |               |                                      |                  |
| SHEET TITLE<br>PILE CAP DETAILS   |               |                                      |                  |
| DESIGNED<br>S.R.   | DRAWN<br>M.H. | CHECKED<br>A.K.                      | APPROVED<br>T.I. |
| RAJUK REF.   |               | RAJUK/BAP/2026/0417                  |                  |
| JOB NO.   |               | MSC-2026-041                         |                  |
| DATE   |               | 12-08-2026                           |                  |
| SCALE   |               | 1:25                                 |                  |
| SHEET NO.<br>S-07   |               | REV.<br>B                            |                  |
| REVISIONS   |               |                                      |                  |
| REV   | DATE          | DESCRIPTION                          |                  |
| A   | 05-07-2026    | ISSUED FOR RAJUK APPROVAL            |                  |
| B   | 12-08-2026    | 4TH 3RD-4TH BARS REVISED; ISSUED FOR |                  |
| ALL DIMENSIONS IN mm U.N.O.<br>DO NOT SCALE THIS DRAWING                                                                                        |               |                                      |                  |





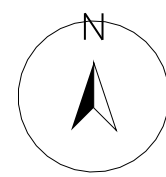

MEGHNA STRUCTURAL CONSULTANT  
S. LTD.  
FLAT 4B, HOUSE 27, ROAD 9, SECTOR 6, UTTARA MODEL TOWN, DHAKA  
TEL: +880 1XXX 000 000 / +880 2 4890 0000

CLIENT  
M/S. PADMA HOMES LTD.


PROJECT  
PROPOSED G+6 STORIED RESIDENTIAL BUILDING

SITE  
PLOT 23, ROAD 7, BLOCK C, BASHUNDHARA R/A, DHAKA



SHEET TITLE  
GRADE BEAM LAYOUT & GF SLAB-ON-GRADE

|                                |            |                                     |          |
|--------------------------------|------------|-------------------------------------|----------|
| DESIGNED                       | DRAWN      | CHECKED                             | APPROVED |
| S.R.                           | M.H.       | A.K.                                | T.I.     |
| RAJUK REF. RAJUK/BAP/2026/0417 |            |                                     |          |
| JOB NO. MSC-2026-041           |            |                                     |          |
| DATE 12-08-2026                |            |                                     |          |
| SCALE 1:100                    |            |                                     |          |
| SHEET NO.                      |            |                                     | REV.     |
| S-08                           |            |                                     | B        |
| REVISIONS                      |            |                                     |          |
| REV                            | DATE       | DESCRIPTION                         |          |
| A                              | 05-07-2026 | ISSUED FOR RAJUK APPROVAL           |          |
| B                              | 12-08-2026 | C4 3RD-4TH BARS REVISED; ISSUED FOR |          |

ALL DIMENSIONS IN mm U.N.D.  
DO NOT SCALE THIS DRAWING

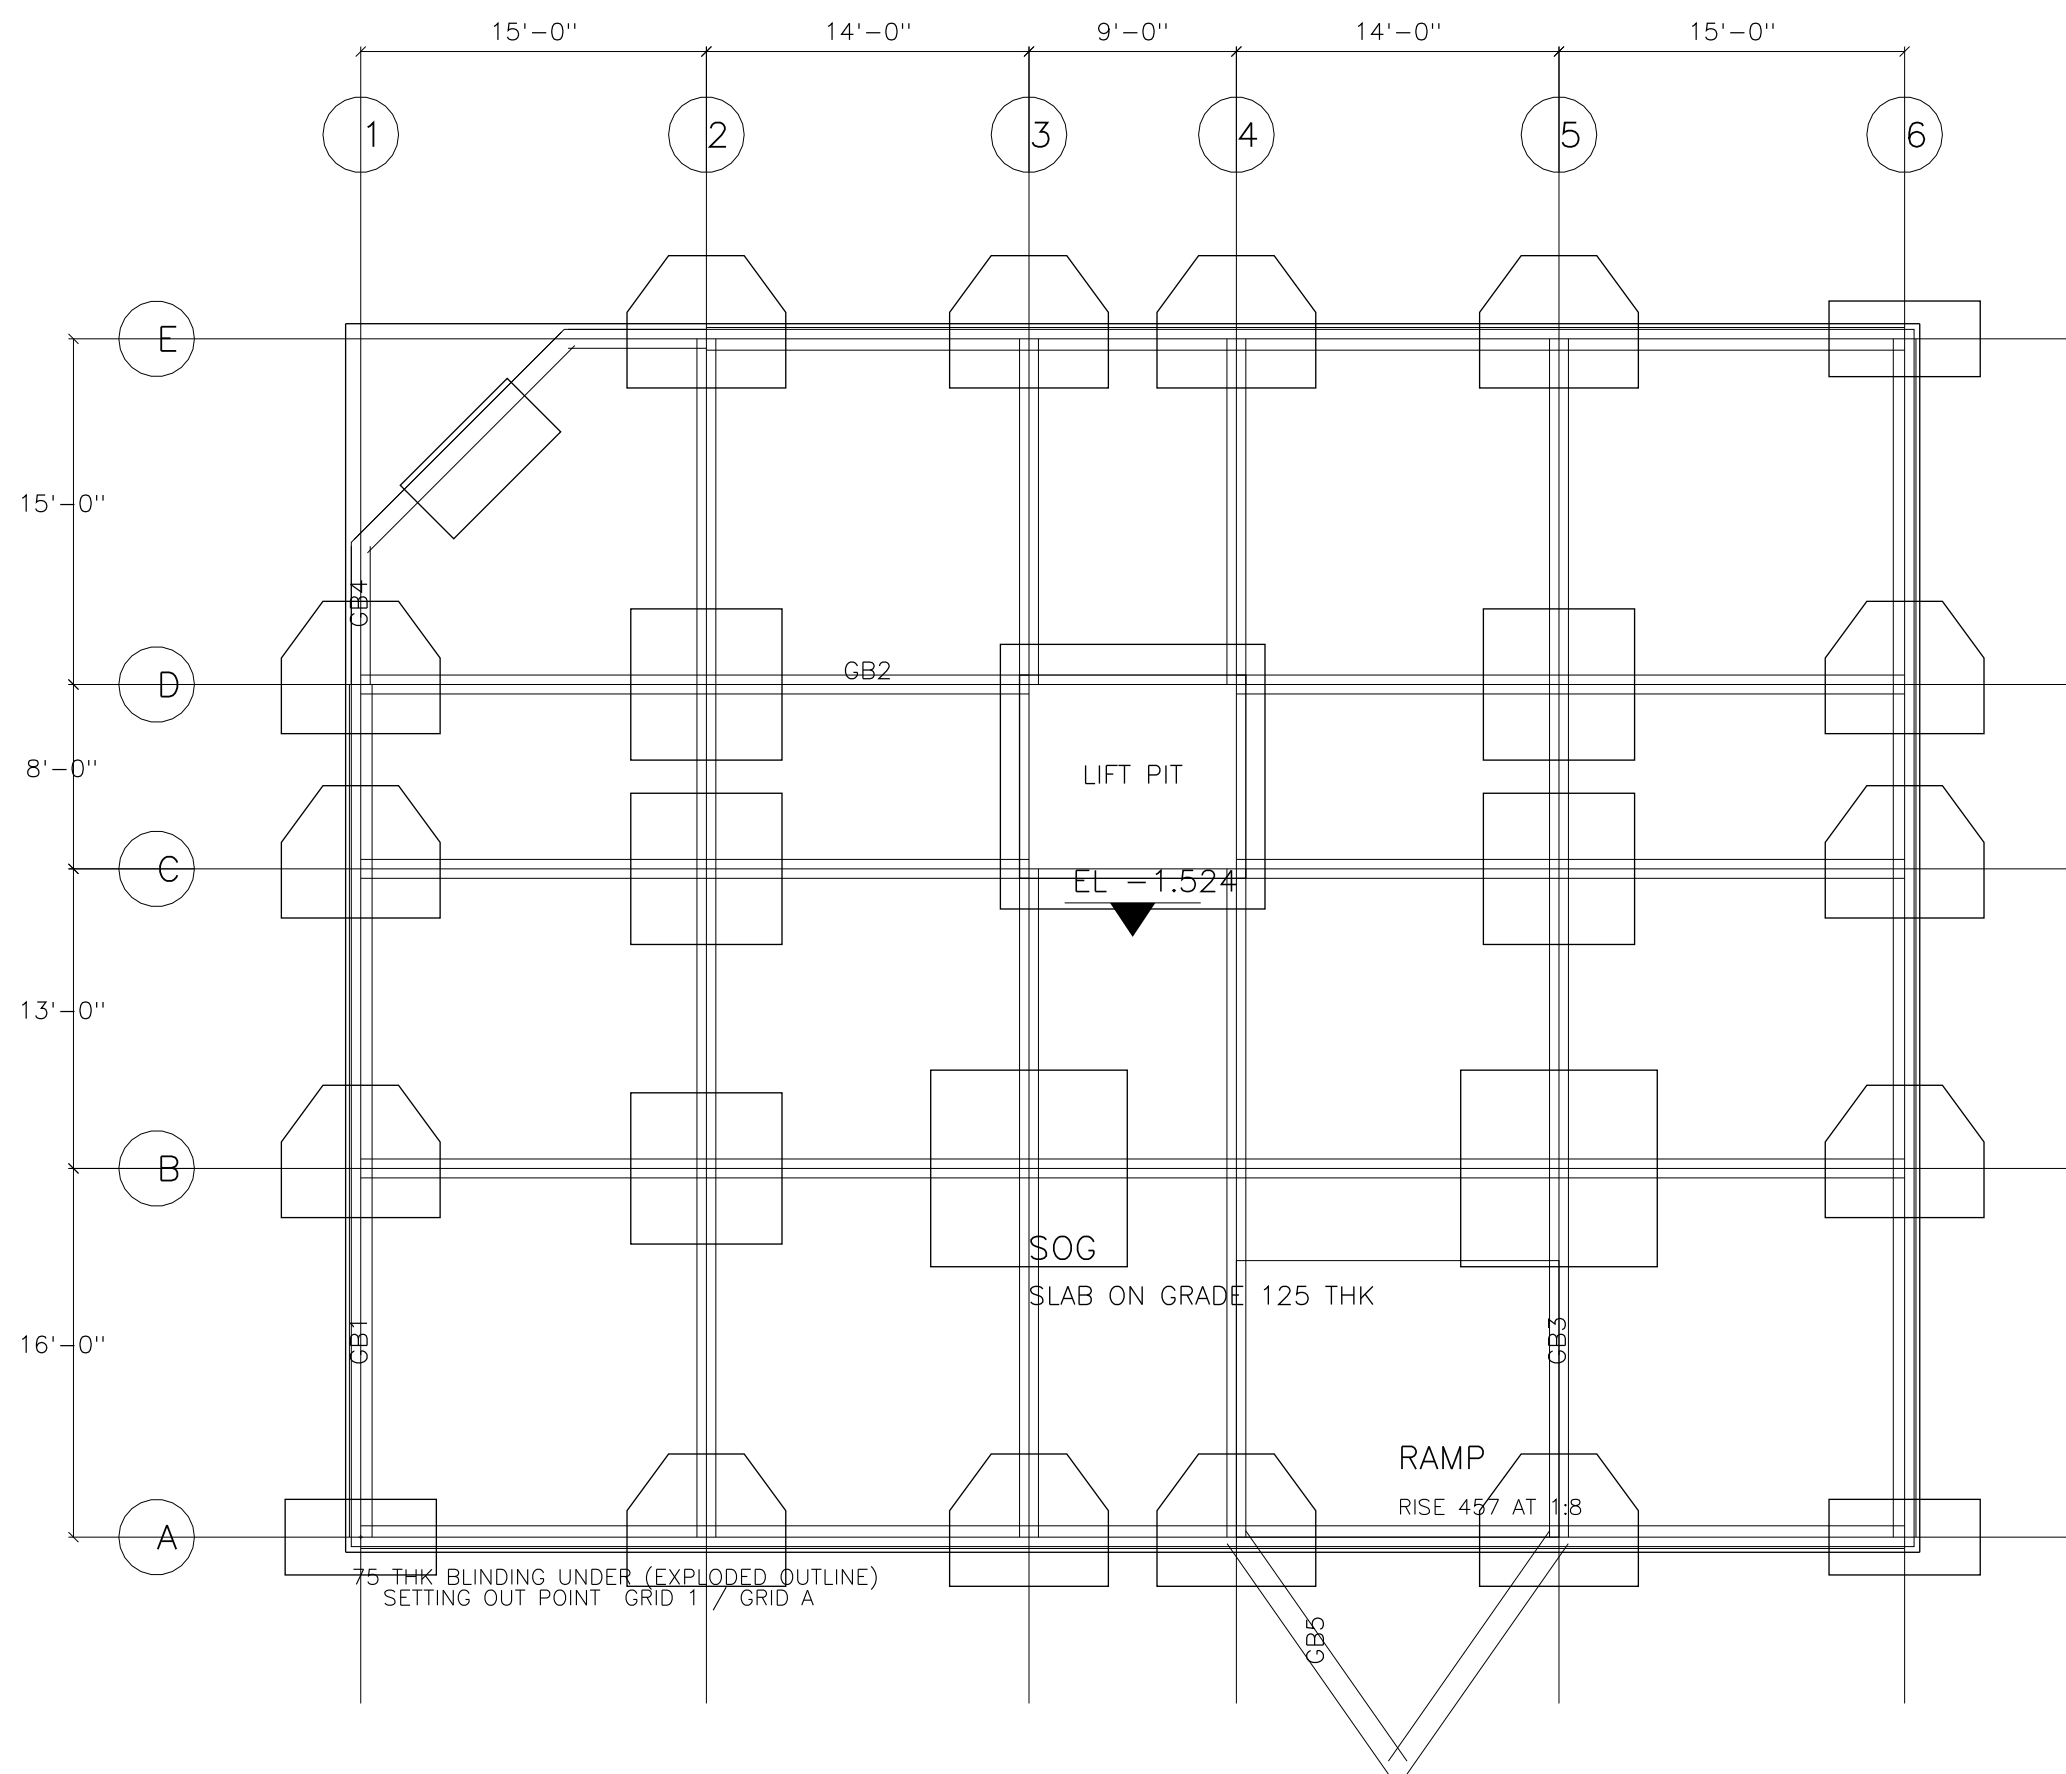

GRADE BEAM LAYOUT & GF SLAB ON GRADE SCALE 1:100

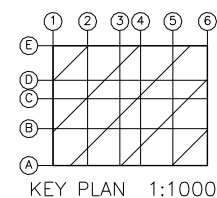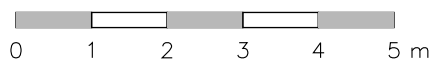





MEGHNA STRUCTURAL CONSULTANTS LTD.

FLAT 4B, HOUSE 27, ROAD 9, SECTOR 6, UTTARA MODEL TOWN, DHAKA

TEL: +880 1XXX 000 000 / +880 2 4890 0000

CLIENT

M/S. PADMA HOMES LTD.

PROJECT

PROPOSED G+6 STORIED RESIDENTIAL BUILDING

SITE

PLOT 23, ROAD 7, BLOCK C, BASHUNDHARA R/A, DHAKA

SHEET TITLE

GRADE BEAM DETAILS (LONG SECTIONS)

DESIGNED

S.R.

DRAWN

M.H.

CHECKED

A.K.

APPROVED

T.I.

RAJUK REF.

RAJUK/BAP/2026/0417

JOB NO.

MSC-2026-041

DATE

12-08-2026

SCALE

1:50

SHEET NO.

S-09

REV.

B


REVISIONS

| REV | DATE       | DESCRIPTION                         |
|-----|------------|-------------------------------------|
| A   | 05-07-2026 | ISSUED FOR RAJUK APPROVAL           |
| B   | 12-08-2026 | C4 3RD-4TH BARS REVISED; ISSUED FOR |




ALL DIMENSIONS IN mm U.N.O.

DO NOT SCALE THIS DRAWING






























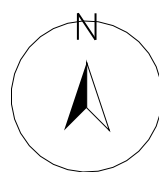


|   |               |                                                    |                  |
|---|---------------|----------------------------------------------------|------------------|
| MEGHNA STRUCTURAL CONSULTANT<br>S. LTD.<br>FLAT 4B, HOUSE 27, ROAD 9, SECTOR 6, UTTARA MODEL TOWN, DHAKA<br>TEL: +880 1XXX 000 000 / +880 2 4890 0000 |               |                                                    |                  |
| CLIENT<br>M/S. PADMA HOMES LTD.   |               |                                                    |                  |
| PROJECT<br>PROPOSED G+6 STORIED RESIDENTIAL BUILDING                                                                                                  |               |                                                    |                  |
| SITE<br>PLOT 23, ROAD 7, BLOCK C, BASHUNDHARA R/A, DHAKA                                                                                              |               |                                                    |                  |
| SHEET TITLE<br>COLUMN LAYOUT PLAN   |               |                                                    |                  |
| DESIGNED<br>S.R.   | DRAWN<br>M.H. | CHECKED<br>A.K.                                    | APPROVED<br>T.I. |
| RAJUK REF. RAJUK/BAP/2026/0417   |               |                                                    |                  |
| JOB NO. MSC-2026-041   |               |                                                    |                  |
| DATE 12-08-2026   |               |                                                    |                  |
| SCALE 1:100   |               |                                                    |                  |
| SHEET NO.<br>S-10   |               | REV.<br>B                                          |                  |
| REVISIONS   |               |                                                    |                  |
| REV   | DATE          | DESCRIPTION                                        |                  |
| A   | 05-07-2026    | ISSUED FOR RAJUK APPROVAL                          |                  |
| B   | 12-08-2026    | C4 3RD-4TH BARS REVISED; ISSUED FOR RAJUK APPROVAL |                  |

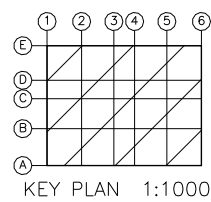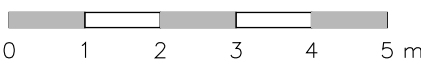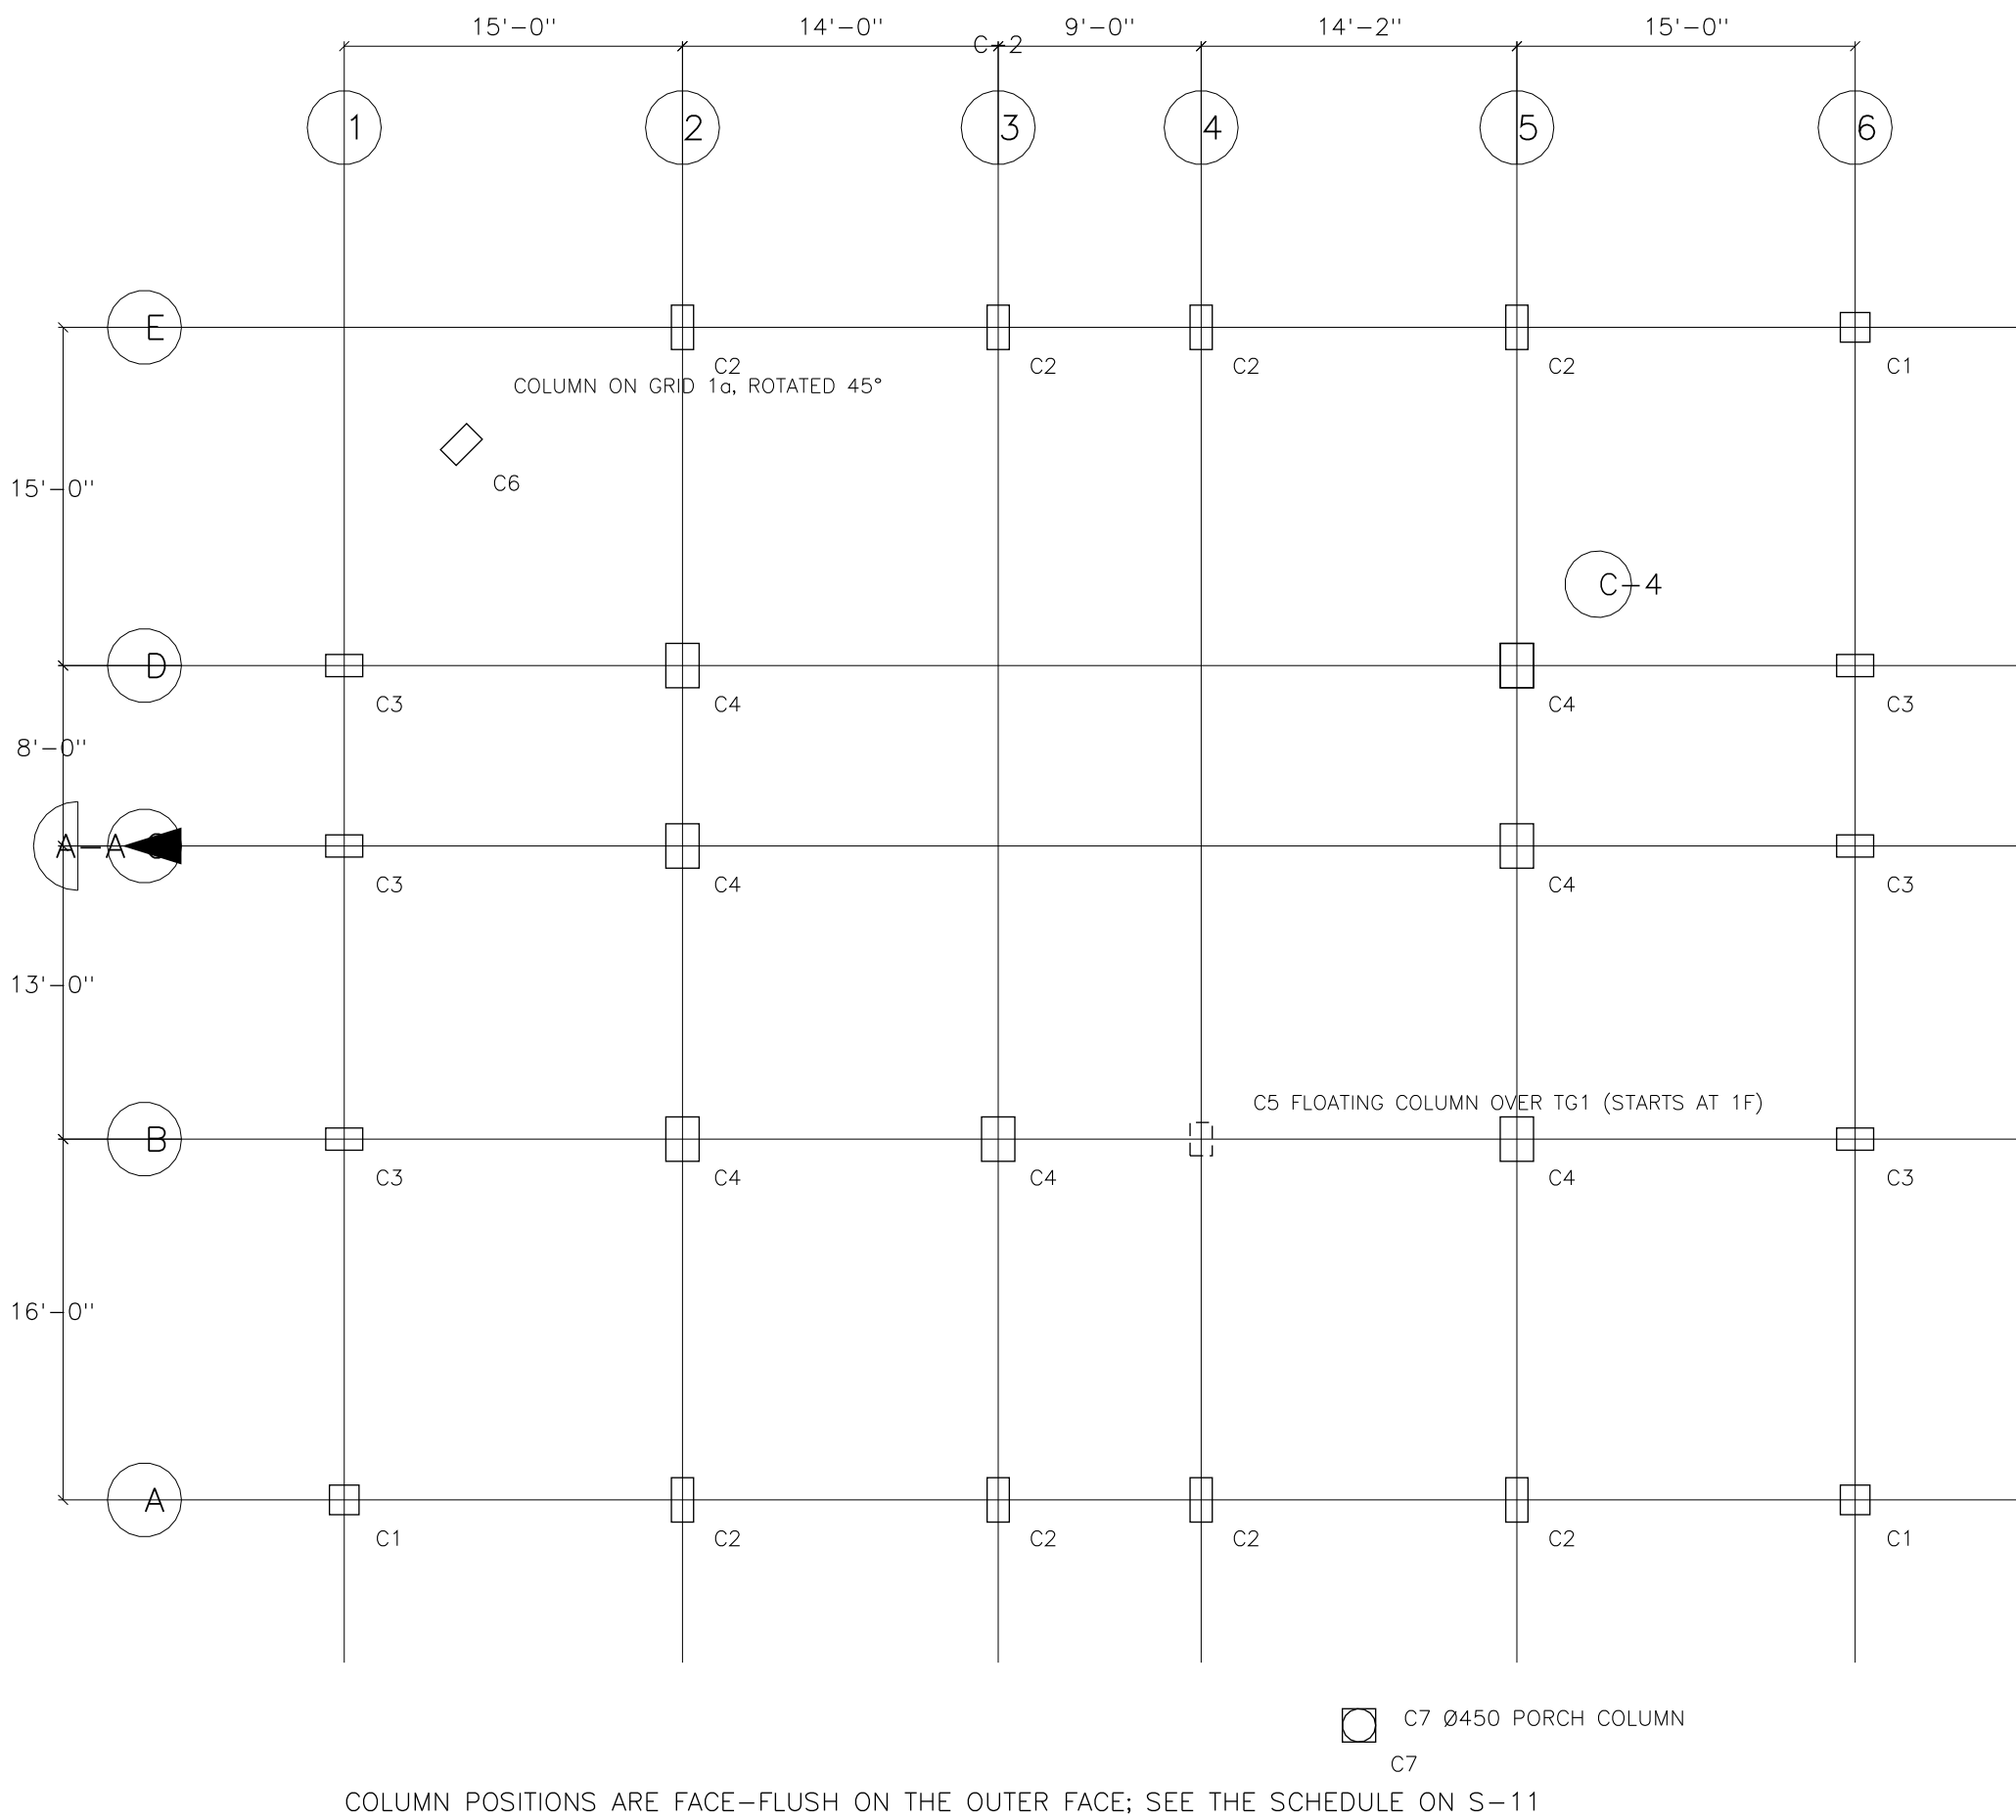




COLUMN SCHEDULE
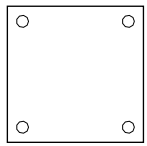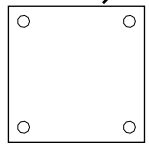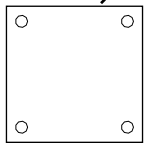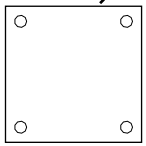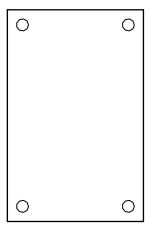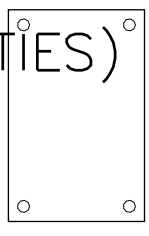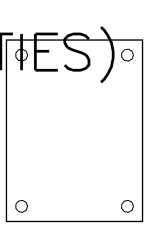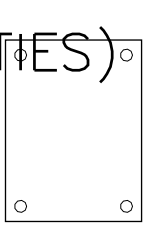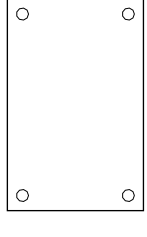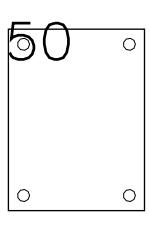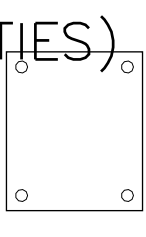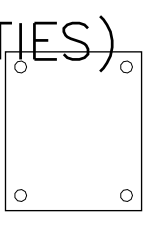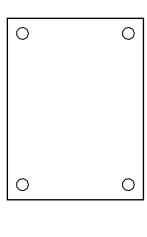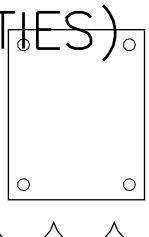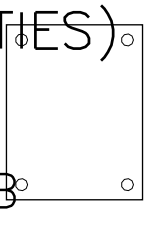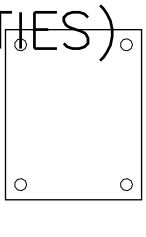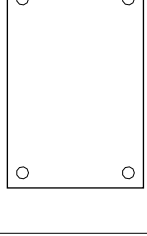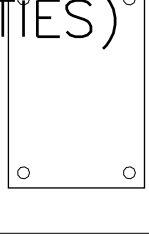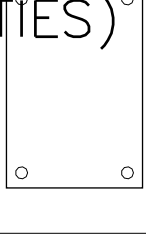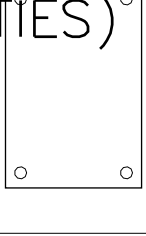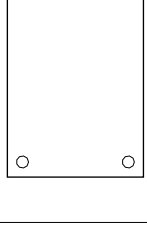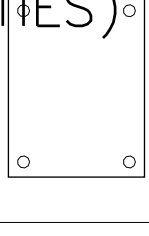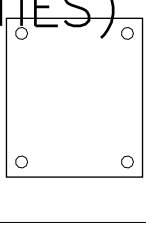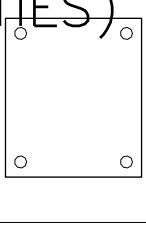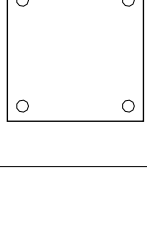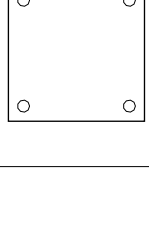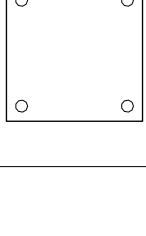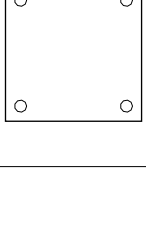
| MARK | GF TO 2ND   | 3RD & 4TH   | 5TH TO 6TH   | ROOF–SRR   |
|------|---|---|---|---|
| C1   | 400x400<br>8–16Ø<br>100@100/150 (TIES)<br>    | 350x350<br>8–16Ø<br>100@100/150 (TIES)<br>                            | 300x300<br>8–16Ø<br>100@100/150 (TIES)<br>   | 300x300<br>8–16Ø<br>100@100/150 (TIES)<br>   |
| C2   | 300x600<br>10–20Ø<br>100@100/150 (TIES)<br>   | 300x500<br>8–20Ø<br>100@100/150 (TIES)<br>                            | 300x400<br>8–16Ø<br>100@100/150 (TIES)<br>   | 300x400<br>8–16Ø<br>100@100/150 (TIES)<br>   |
| C3   | 300x500<br>8–20Ø<br>TIES 100@100/150<br>      | 300x400<br>8–16Ø<br>100@100/150 (TIES)<br>                            | 300x350<br>6–16Ø<br>100@100/150 (TIES)<br>   | 300x350<br>6–16Ø<br>100@100/150 (TIES)<br>   |
| C4   | 450x600<br>12–25Ø<br>100@100/150 (TIES)<br> | 400x500<br>10–25Ø<br>100@100/150 (TIES)<br>2–20Ø EXTRA<br>REV B<br> | 350x450<br>8–20Ø<br>100@100/150 (TIES)<br> | 300x375<br>6–16Ø<br>100@100/150 (TIES)<br> |
| C5   | 300x450<br>8–20Ø<br>100@100/150 (TIES)<br>  | 300x450<br>8–20Ø<br>100@100/150 (TIES)<br>                          | 300x450<br>6–20Ø<br>100@100/150 (TIES)<br> | 300x450<br>6–20Ø<br>100@100/150 (TIES)<br> |
| C6   | 300x500<br>8–20Ø<br>100@100/150 (TIES)<br>  | 300x400<br>8–16Ø<br>100@100/150 (TIES)<br>                          | 300x350<br>6–16Ø<br>100@100/150 (TIES)<br> | 300x350<br>6–16Ø<br>100@100/150 (TIES)<br> |
| C7   | 450x450<br>8–20Ø<br>100@100/100 (TIES)<br>  | 450x450<br>8–20Ø<br>100@100/100 (TIES)<br>                          | 450x450<br>8–20Ø<br>100@100/100 (TIES)<br> | 450x450<br>8–20Ø<br>100@100/100 (TIES)<br> |

C2 GF TO 2ND: 12"X24"      12" x 24"      300x600  
THE MILLIMETRE CELL GOVERNS; THE INCH CAPTION IS A ROUNDED RESTATEMENT  
ALL COLUMNS f'c = 3500 psi, fy = 500 MPa, 40 mm CLEAR COVER

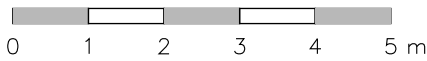

MEGHNA STRUCTURAL CONSULTANT  
S. LTD.  
FLAT-4B, HOUSE 27, ROAD 9, SECTOR 6, UTTARA MODEL TOWN, DHAKA  
TEL: +880 1XXXX 000 000 / +880 2 4890 0000

CLIENT  
M/S. PADMA HOMES LTD.

PROJECT  
PROPOSED G+6 STORIED RESIDENTIAL BUILDING

SITE  
PLOT 23, ROAD 7, BLOCK C, BASHUNDHARA R/A, DHAKA

SHEET TITLE  
COLUMN SCHEDULE

DESIGNED  
S.R.

DRAWN  
M.H.

CHECKED  
A.K.

APPROVED  
T.I.

RAJUK REF. RAJUK/BAP/2026/0417

JOB NO. MSC–2026–041

DATE 12–08–2026

SCALE N.T.S.

SHEET NO.  
S–11

REV.  
B

REVISIONS

REV




DATE

DESCRIPTION




A 05–07–2026 ISSUED FOR RAJUK APPROVAL

B 12–08–2026 C4 3RD–4TH BARS REVISED; ISSUED FOR

ALL DIMENSIONS IN mm U.N.D.  
DO NOT SCALE THIS DRAWING

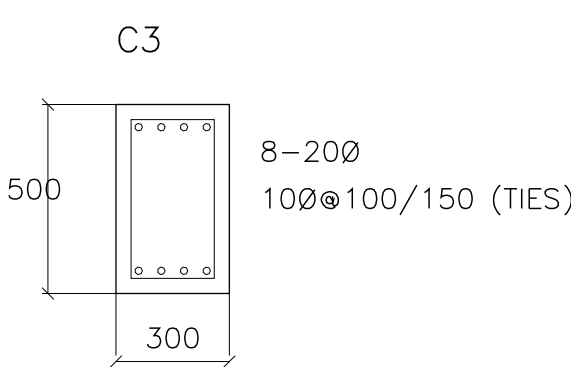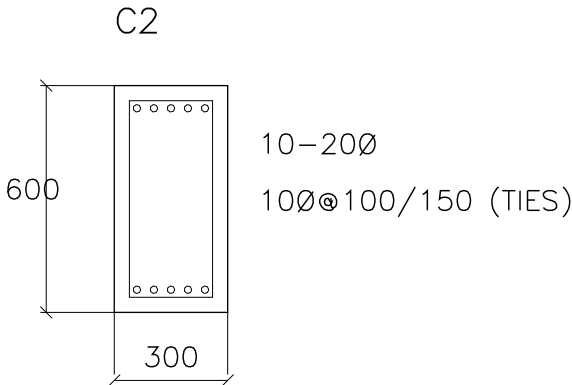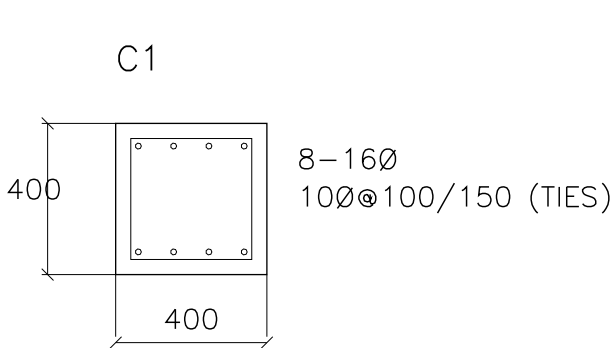

C1 SECTION SCALE 1:20 (DRAWN x5, DIMLFAC 0.2) C2 SECTION SCALE 1:20 (DRAWN x5, DIMLFAC 0.2) C3 SECTION SCALE 1:20 (DRAWN x5, DIMLFAC 0.2)

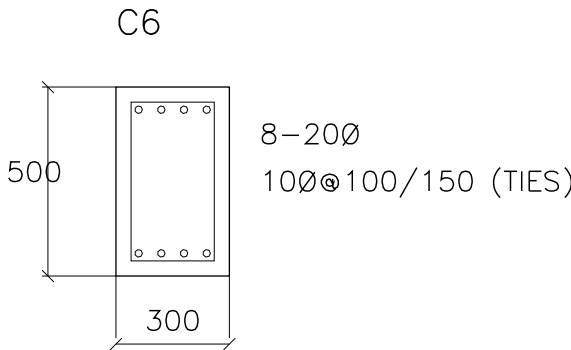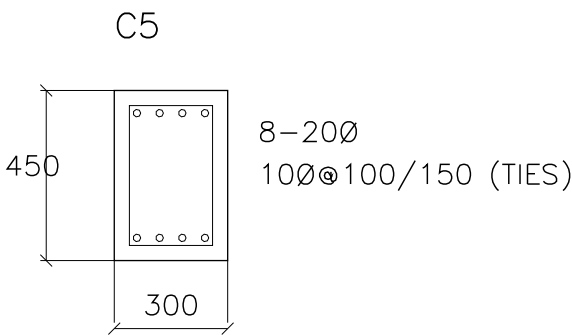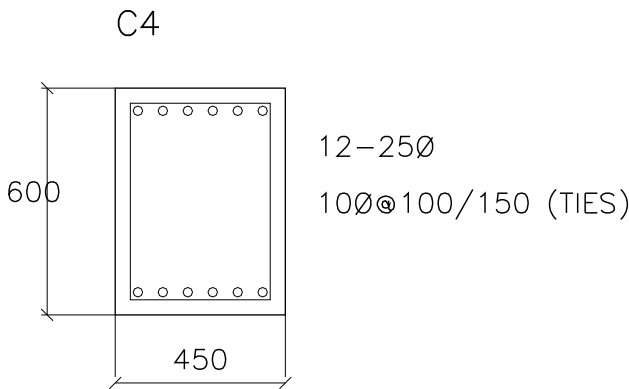


C4 SECTION SCALE 1:20 (DRAWN x5, DIMLFAC 0.2) C5 SECTION SCALE 1:20 (DRAWN x5, DIMLFAC 0.2) C6 SECTION SCALE 1:20 (DRAWN x5, DIMLFAC 0.2)




|   |               |                                     |                  |
|---|---------------|-------------------------------------|------------------|
| MEGHNA STRUCTURAL CONSULTANTS LTD.<br>FLAT 4B, HOUSE 27, ROAD 9, SECTOR 6, UTTARA MODEL TOWN, DHAKA<br>TEL +880 1XXX 000 000 / +880 2 4890 0000 |               |                                     |                  |
| CLIENT<br>M/S. PADMA HOMES LTD.   |               |                                     |                  |
| PROJECT<br>PROPOSED G+6 STORIED RESIDENTIAL BUILDING                                                                                            |               |                                     |                  |
| SITE<br>PLOT 23, ROAD 7, BLOCK C, BASHUNDHARA R/A, DHAKA                                                                                        |               |                                     |                  |
| SHEET TITLE<br>COLUMN DETAILS   |               |                                     |                  |
| DESIGNED<br>S.R.   | DRAWN<br>M.H. | CHECKED<br>A.K.                     | APPROVED<br>T.I. |
| RAJUK REF.   |               | RAJUK/BAP/2026/0417                 |                  |
| JOB NO.   |               | MSC-2026-041                        |                  |
| DATE   |               | 12-08-2026                          |                  |
| SCALE   |               | 1:20                                |                  |
| SHEET NO.<br>S-12   |               | REV.<br>B                           |                  |
| REVISIONS   |               |                                     |                  |
| REV   | DATE          | DESCRIPTION                         |                  |
| A   | 05-07-2026    | ISSUED FOR RAJUK APPROVAL           |                  |
| B   | 12-08-2026    | C4 3RD-4TH BARS REVISED; ISSUED FOR |                  |
| ALL DIMENSIONS IN mm U.N.O.<br>DO NOT SCALE THIS DRAWING                                                                                        |               |                                     |                  |





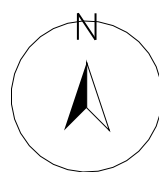


|   |               |                                     |                  |
|---|---------------|-------------------------------------|------------------|
| MEGHNA STRUCTURAL CONSULTANT<br>S. LTD.<br>FLAT 4B, HOUSE 27, ROAD 9, SECTOR 6, UTTARA MODEL TOWN, DHAKA<br>TEL: +880 1XXX 000 000 / +880 2 4890 0000 |               |                                     |                  |
| CLIENT<br>M/S. PADMA HOMES LTD.   |               |                                     |                  |
| PROJECT<br>PROPOSED G+6 STORIED RESIDENTIAL BUILDING                                                                                                  |               |                                     |                  |
| SITE<br>PLOT 23, ROAD 7, BLOCK C, BASHUNDHARA R/A, DHAKA                                                                                              |               |                                     |                  |
| SHEET TITLE<br>1ST FLOOR BEAM LAYOUT   |               |                                     |                  |
| DESIGNED<br>S.R.   | DRAWN<br>M.H. | CHECKED<br>A.K.                     | APPROVED<br>T.I. |
| RAJUK REF. RAJUK/BAP/2026/0417   |               |                                     |                  |
| JOB NO. MSC-2026-041   |               |                                     |                  |
| DATE 12-08-2026   |               |                                     |                  |
| SCALE 1:100   |               |                                     |                  |
| SHEET NO.<br>S-13   |               | REV.<br>B                           |                  |
| REVISIONS   |               |                                     |                  |
| REV.   | DATE          | DESCRIPTION                         |                  |
| A   | 05-07-2026    | ISSUED FOR RAJUK APPROVAL           |                  |
| B   | 12-08-2026    | C4 3RD-4TH BARS REVISED; ISSUED FOR |                  |

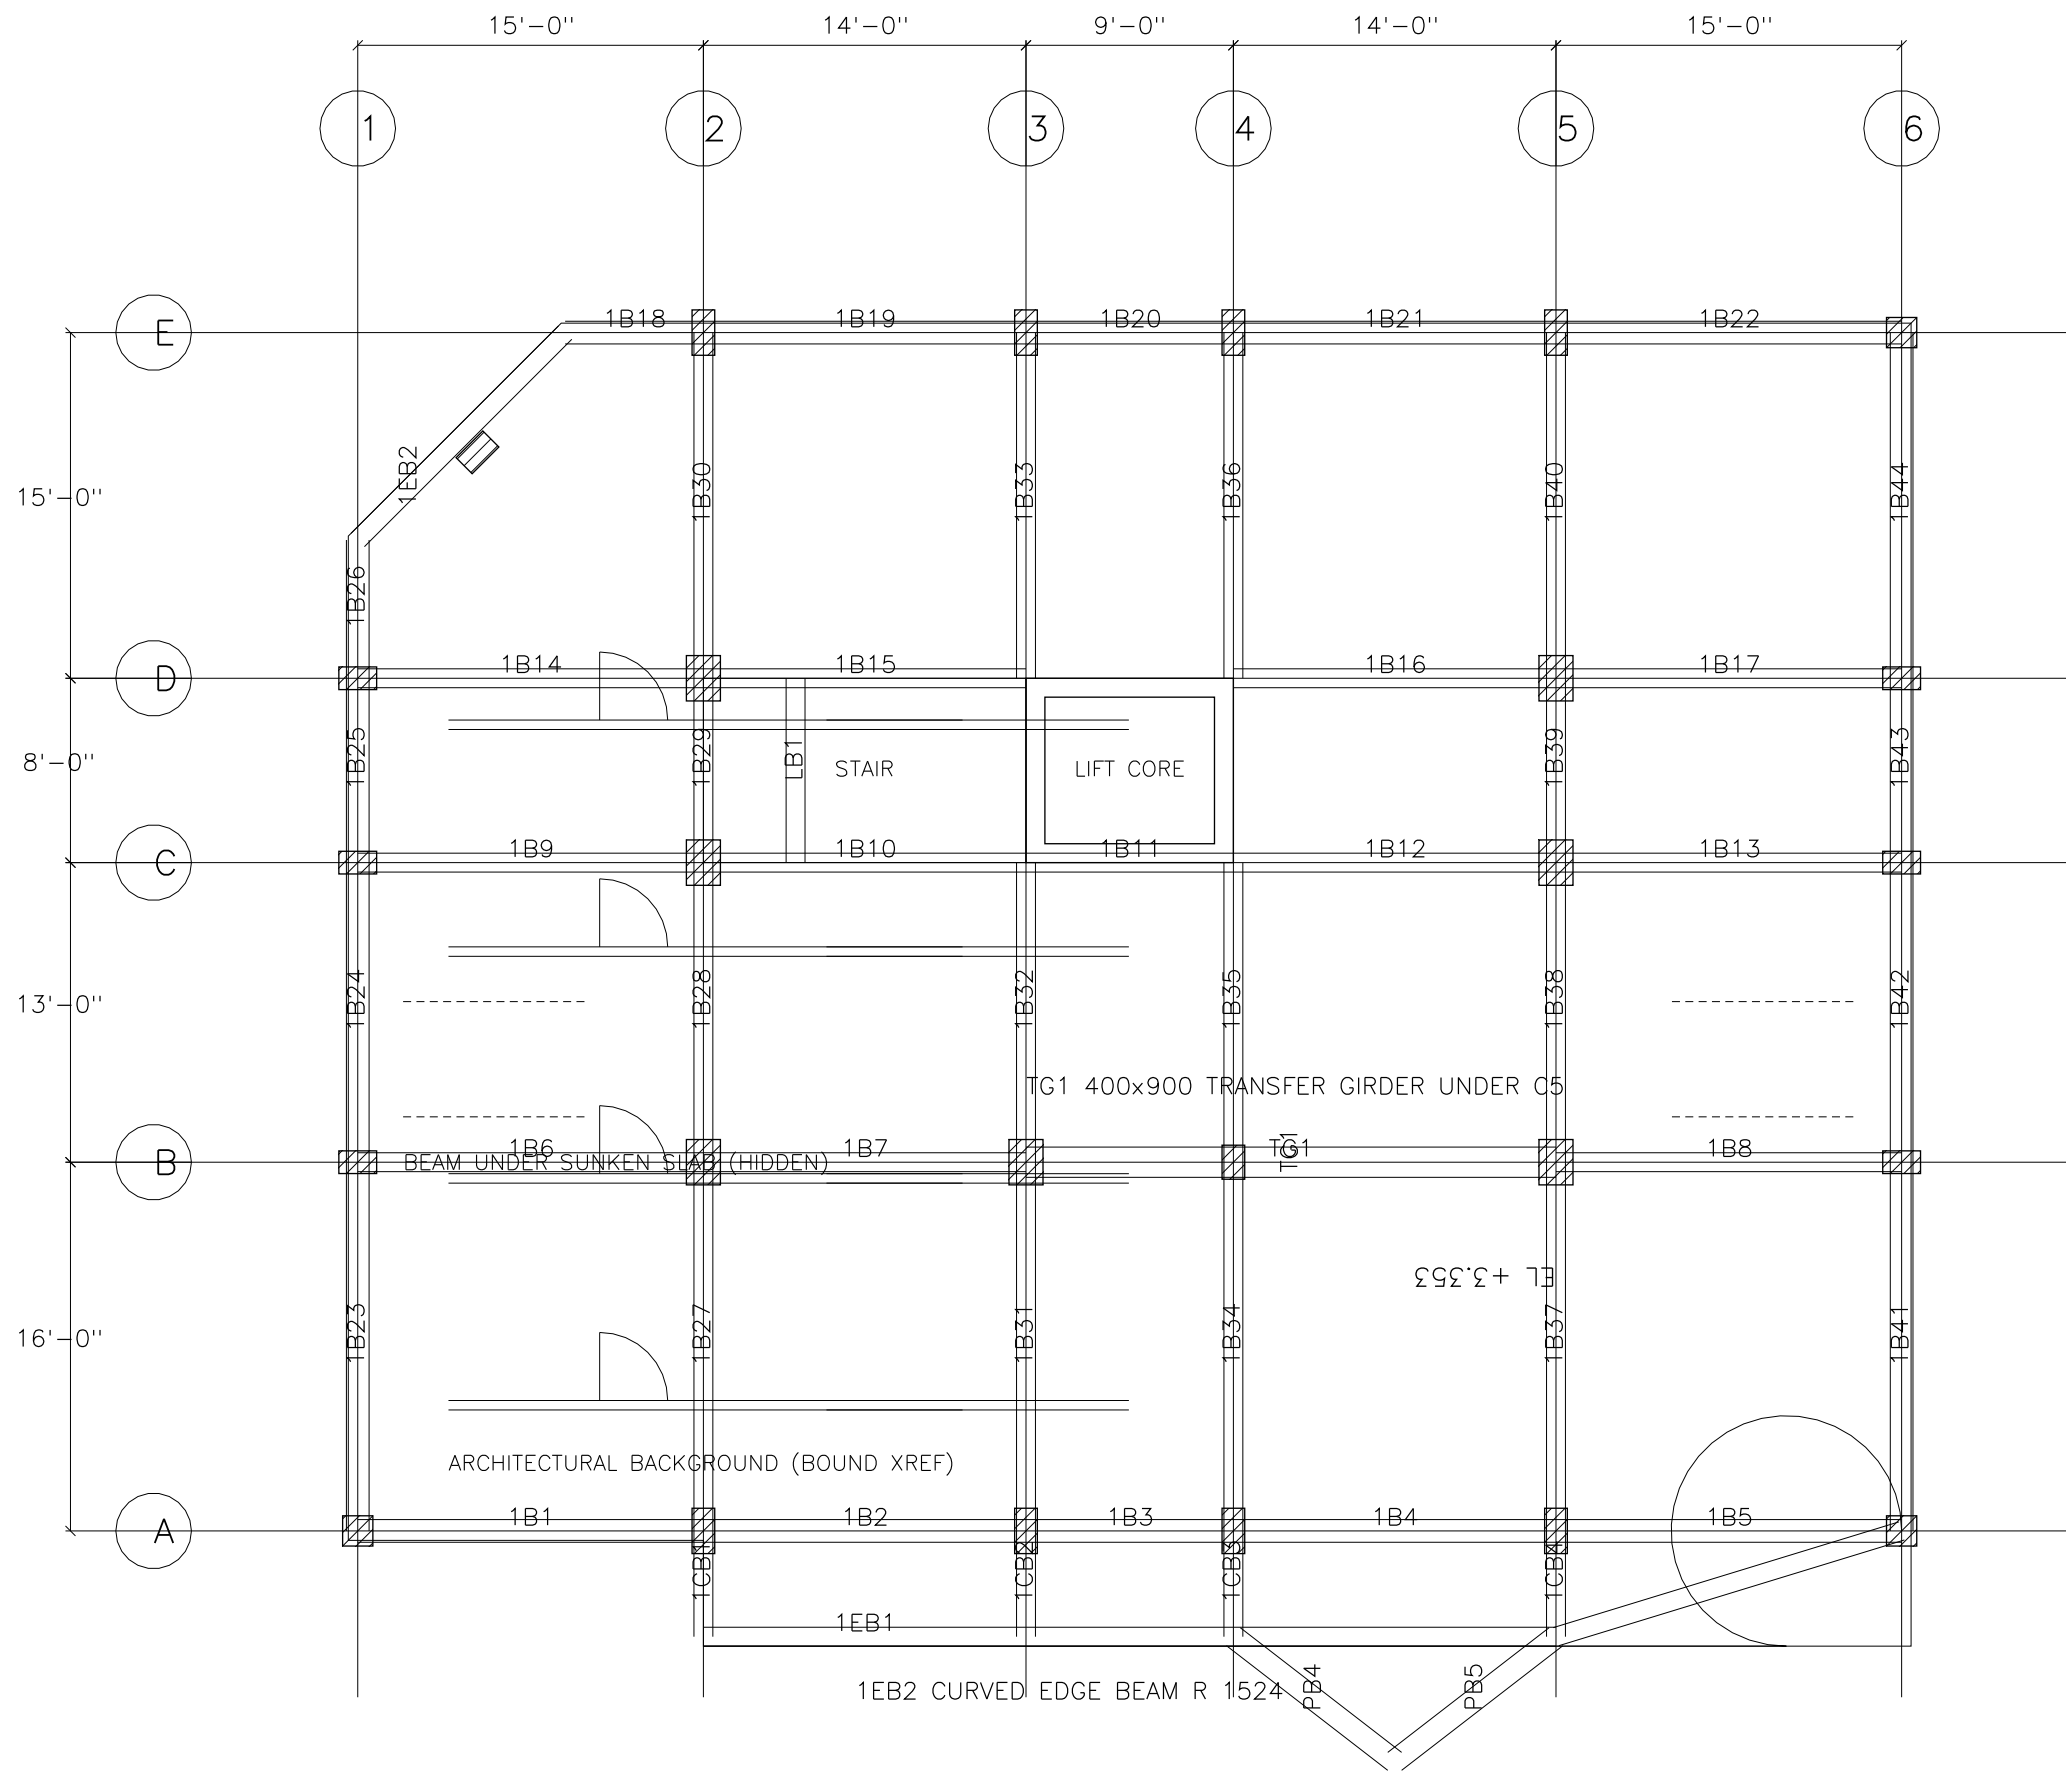


1ST FLOOR BEAM LAYOUT SCALE 1:100

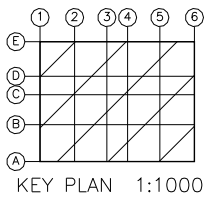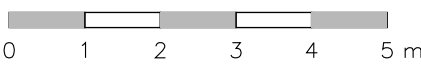



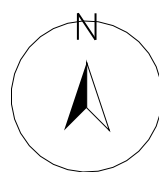


|   |               |                                                    |                  |
|---|---------------|----------------------------------------------------|------------------|
| MEGHNA STRUCTURAL CONSULTANT<br>S. LTD.<br>FLAT 4B, HOUSE 27, ROAD 9, SECTOR 6, UTTARA MODEL TOWN, DHAKA<br>TEL: +880 1XXX 000 000 / +880 2 4890 0000 |               |                                                    |                  |
| CLIENT<br>M/S. PADMA HOMES LTD.   |               |                                                    |                  |
| PROJECT<br>PROPOSED G+6 STORIED RESIDENTIAL BUILDING                                                                                                  |               |                                                    |                  |
| SITE<br>PLOT 23, ROAD 7, BLOCK C, BASHUNDHARA R/A, DHAKA                                                                                              |               |                                                    |                  |
| SHEET TITLE<br>TYPICAL FLOOR BEAM LAYOUT (2ND TO 6TH FLOOR)                                                                                           |               |                                                    |                  |
| DESIGNED<br>S.R.   | DRAWN<br>M.H. | CHECKED<br>A.K.                                    | APPROVED<br>T.I. |
| RAJUK REF. RAJUK/BAP/2026/0417   |               |                                                    |                  |
| JOB NO. MSC-2026-041   |               |                                                    |                  |
| DATE 12-08-2026   |               |                                                    |                  |
| SCALE 1:100   |               |                                                    |                  |
| SHEET NO.<br>S-14   |               | REV.<br>B                                          |                  |
| REVISIONS   |               |                                                    |                  |
| REV.   | DATE          | DESCRIPTION                                        |                  |
| A   | 05-07-2026    | ISSUED FOR RAJUK APPROVAL                          |                  |
| B   | 12-08-2026    | C4 3RD-4TH BARS REVISED; ISSUED FOR RAJUK APPROVAL |                  |

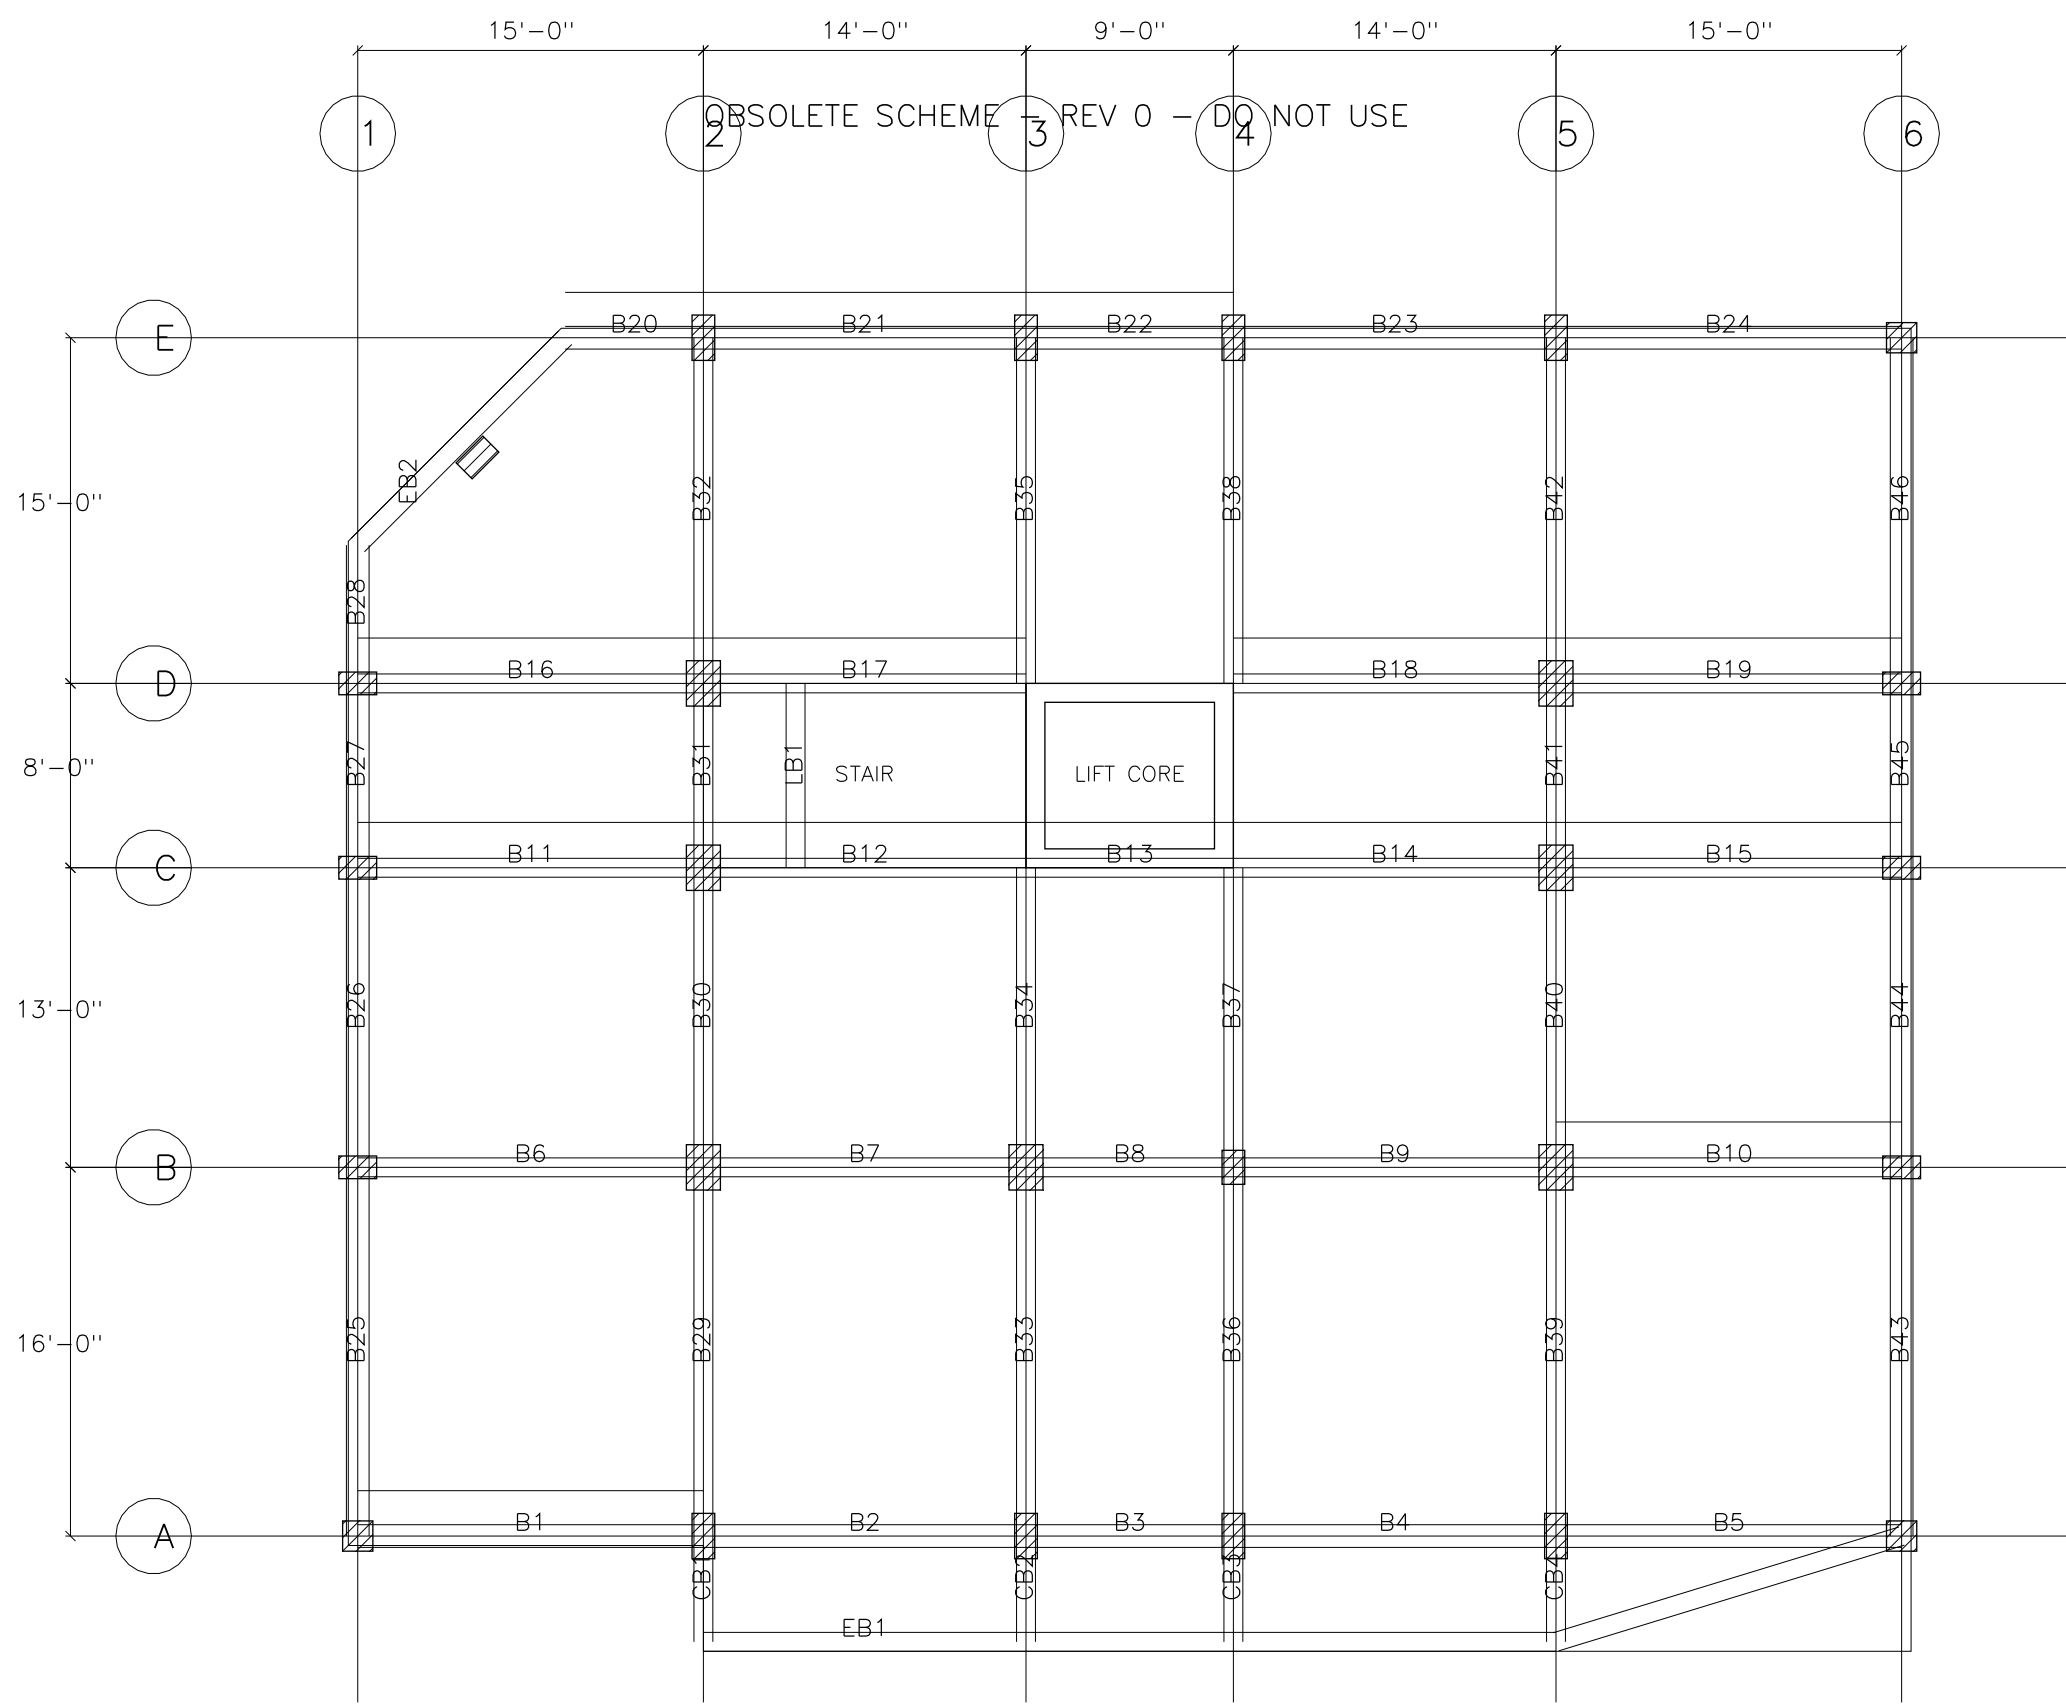


TYPICAL FLOOR BEAM LAYOUT  
(2ND TO 6TH FLOOR)

TYPICAL FLOOR BEAM LAYOUT SCALE 1:100

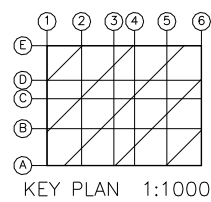



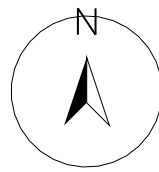

MEGHNA STRUCTURAL CONSULTANT  
S. LTD.  
FLAT #B, HOUSE 27, ROAD 9, SECTOR 6, UTTARA MODEL TOWN, DHAKA  
TEL: +880 1XXX 000 000 / +880 2 4890 0000


CLIENT  
M/S. PADMA HOMES LTD.

PROJECT  
PROPOSED G+6 STORIED RESIDENTIAL BUILDING


SITE  
PLOT 23, ROAD 7, BLOCK C, BASHUNDHARA R/A, DHAKA

SHEET TITLE  
ROOF & STAIR ROOF BEAM LAYOUT

|                                |            |                                     |           |
|--------------------------------|------------|-------------------------------------|-----------|
| DESIGNED                       | DRAWN      | CHECKED                             | APPROVED  |
| S.R.                           | M.H.       | A.K.                                | T.I.      |
| RAJUK REF. RAJUK/BAP/2026/0417 |            |                                     |           |
| JOB NO. MSC-2026-041           |            |                                     |           |
| DATE 12-08-2026                |            |                                     |           |
| SCALE 1:100                    |            |                                     |           |
| SHEET NO.<br>S-15              |            |                                     | REV.<br>B |
| REVISIONS                      |            |                                     |           |
| REV                            | DATE       | DESCRIPTION                         |           |
| A                              | 05-07-2026 | ISSUED FOR RAJUK APPROVAL           |           |
| B                              | 12-08-2026 | C4 3RD-4TH BARS REVISED; ISSUED FOR |           |

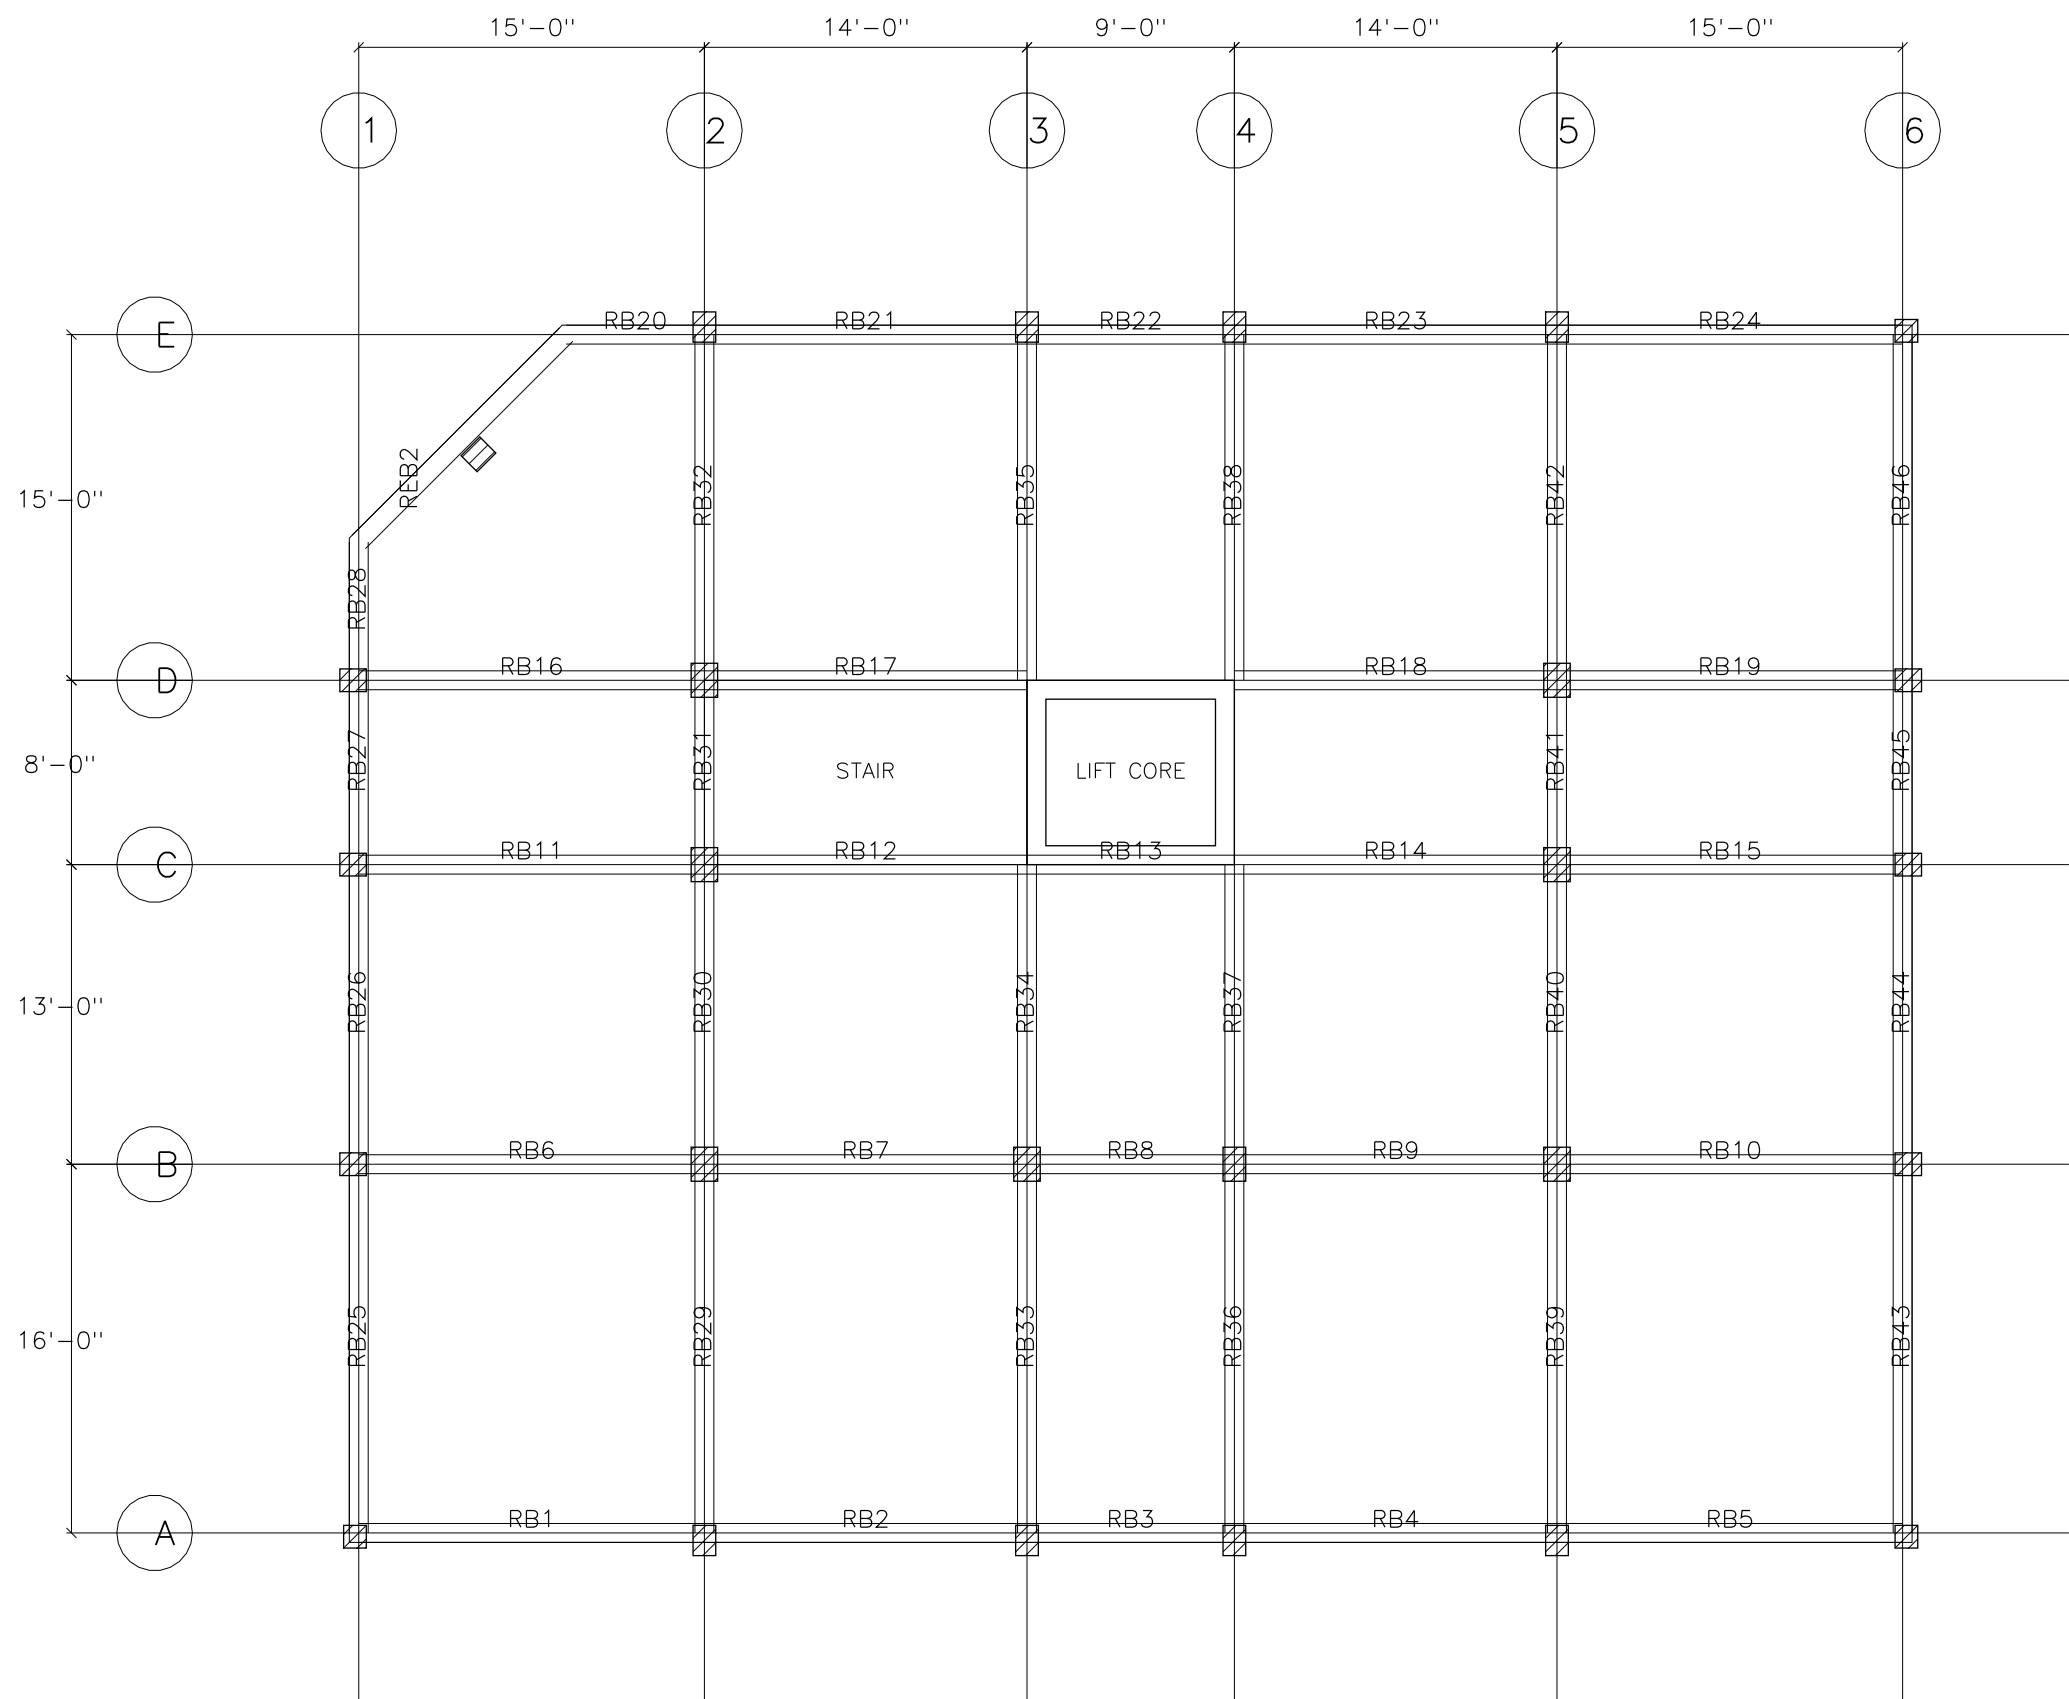



ROOF BEAM LAYOUT (AT ROOF LEVEL)

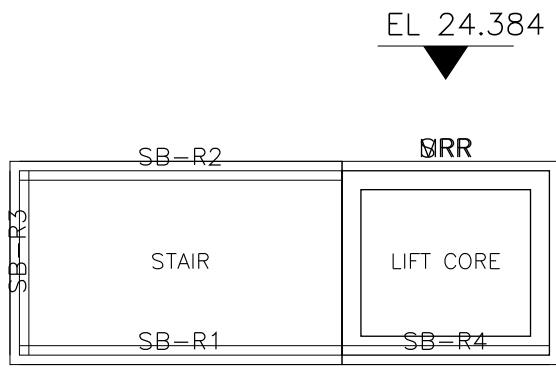

STAIR ROOF & MACHINE ROOM ROOF (5TH TO ROOF)

STAIR ROOF BEAM LAYOUT SCALE 1:100

ROOF BEAM LAYOUT SCALE 1:100

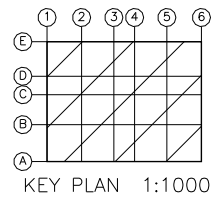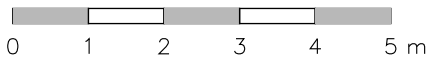

KEY PLAN 1:1000



1ST FLOOR BEAM LONG SECTIONS – TOP, BOTTOM AND EXTRA BARS



1ST FLOOR BEAM DETAILS SCALE 1:50

MEGHNA STRUCTURAL CONSULTANTS LTD.  
FLAT #B, HOUSE 27, ROAD 9, SECTOR 6, UTTARA MODEL TOWN  
TEL: +880 1XXX 000 000 / +880 2 4890 0000

CLIENT  
M/S. PADMA HOMES LTD.

PROJECT  
PROPOSED G+6 STORIED RESIDENTIAL BUILDING

SITE  
PLOT 23, ROAD 7, BLOCK C, BASHUNDHARA R/A, DHAKA

SHEET TITLE  
BEAM DETAILS (1 OF 3) – 1ST FLOOR

DESIGNED  
S.R.

DRAWN  
M.H.

CHECKED  
A.K.

APPROVED  
T.I.

RAJUK REF. RAJUK/BAP/2026/0417

JOB NO. MSC-2026-041

DATE 12-08-2026

SCALE 1:50


SHEET NO.  
S-16

REV.  
B

REVISIONS  

| REV | DATE       | DESCRIPTION                         |
|-----|------------|-------------------------------------|
| A   | 05-07-2026 | ISSUED FOR RAJUK APPROVAL           |
| B   | 12-08-2026 | B4 3RD-4TH BARS REVISED; ISSUED FOR |


ALL DIMENSIONS IN mm U.N.O.  
DO NOT SCALE THIS DRAWING

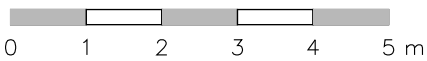




TYPICAL FLOOR BEAM LONG SECTIONS (2ND TO 6TH FLOOR)

2L-100<sup>L/4</sup> @ 100 c/c  
B1 300x600  
3-16 $\emptyset$  TOP

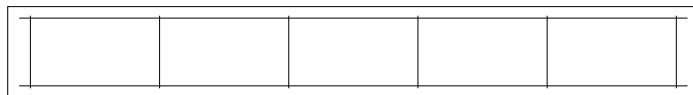


3-20 $\emptyset$  BOT. 100 @ 100 c/c

B2 300x600  
3-16 $\emptyset$  TOP

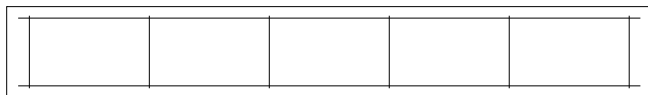


3-20 $\emptyset$  BOT. 100 @ 100 c/c

B3 300x600  
3-16 $\emptyset$  TOP

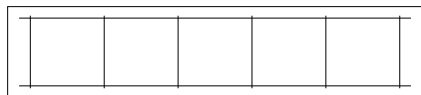


3-20 $\emptyset$  BOT. 100 @ 100 c/c

B4 300x600  
3-16 $\emptyset$  TOP

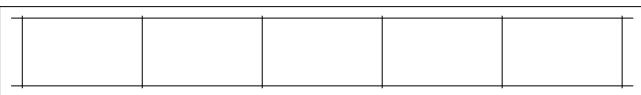


3-20 $\emptyset$  BOT. 100 @ 100 c/c

B5 300x600  
3-16 $\emptyset$  TOP

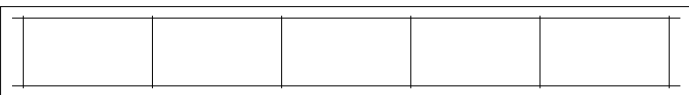


3-20 $\emptyset$  BOT. 100 @ 100 c/c

B6 250x450  
2-16 $\emptyset$  TOP

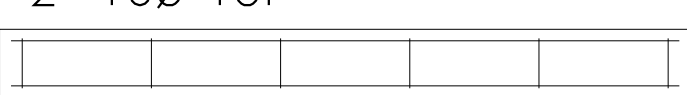


3-16 $\emptyset$  BOT. 100 @ 100 c/c

B7 250x450  
2-16 $\emptyset$  TOP

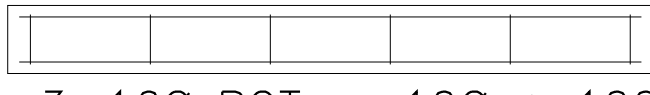


3-16 $\emptyset$  BOT. 100 @ 100 c/c

B8 250x450  
2-16 $\emptyset$  TOP

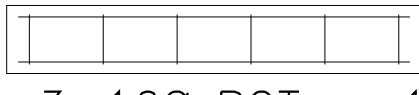


3-16 $\emptyset$  BOT. 100 @ 100 c/c

B9 250x450  
2-16 $\emptyset$  TOP

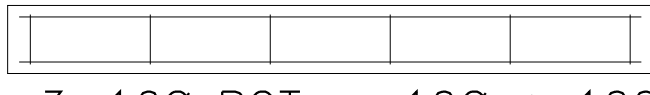


3-16 $\emptyset$  BOT. 100 @ 100 c/c

B10 250x450  
2-16 $\emptyset$  TOP

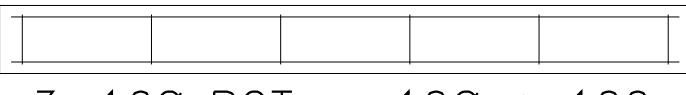


3-16 $\emptyset$  BOT. 100 @ 100 c/c

B11 250x450  
2-16 $\emptyset$  TOP

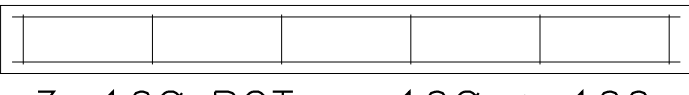


3-16 $\emptyset$  BOT. 100 @ 100 c/c

B12 250x450  
2-16 $\emptyset$  TOP

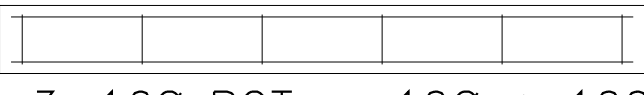


3-16 $\emptyset$  BOT. 100 @ 100 c/c

B13 250x450  
2-16 $\emptyset$  TOP

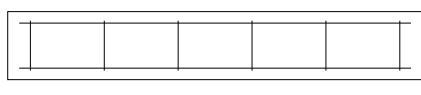


3-16 $\emptyset$  BOT. 100 @ 100 c/c

B14 250x450  
2-16 $\emptyset$  TOP

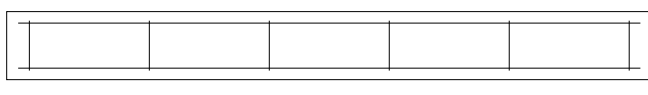


3-16 $\emptyset$  BOT. 100 @ 100 c/c

B15 250x450  
2-16 $\emptyset$  TOP

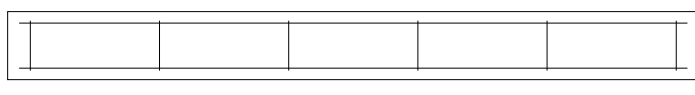


3-16 $\emptyset$  BOT. 100 @ 100 c/c

B16 250x450  
2-16 $\emptyset$  TOP

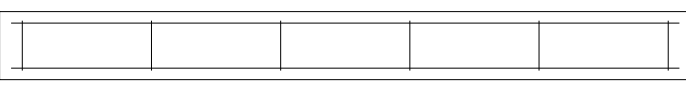


3-16 $\emptyset$  BOT. 100 @ 100 c/c

B17 250x450  
2-16 $\emptyset$  TOP

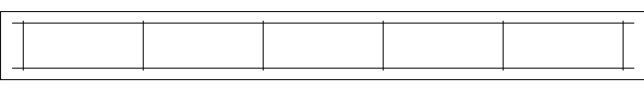


3-16 $\emptyset$  BOT. 100 @ 100 c/c

B18 250x450  
2-16 $\emptyset$  TOP

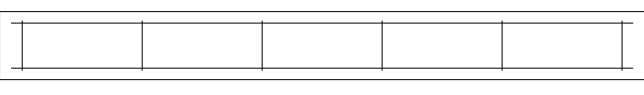


3-16 $\emptyset$  BOT. 100 @ 100 c/c

B19 250x450  
2-16 $\emptyset$  TOP

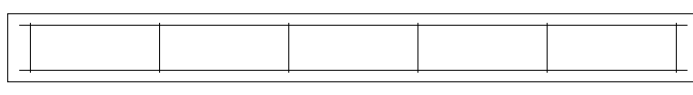


3-16 $\emptyset$  BOT. 100 @ 100 c/c

B20 300x600  
3-16 $\emptyset$  TOP

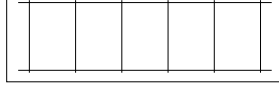


3-20 $\emptyset$  BOT. 100 @ 100 c/c

B21 300x600  
3-16 $\emptyset$  TOP

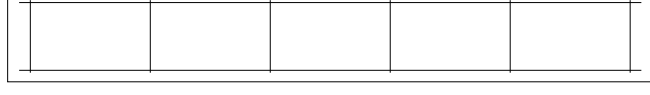


3-20 $\emptyset$  BOT. 100 @ 100 c/c

B22 300x600  
3-16 $\emptyset$  TOP

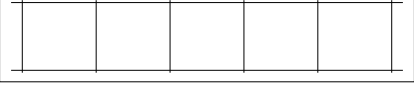


3-20 $\emptyset$  BOT. 100 @ 100 c/c

B23 300x600  
3-16 $\emptyset$  TOP

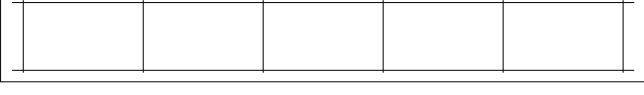

3-20 $\emptyset$  BOT. 100 @ 100 c/c

B24 300x600  
3-16 $\emptyset$  TOP

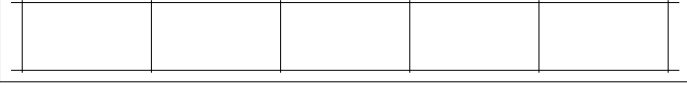

3-20 $\emptyset$  BOT. 100 @ 100 c/c

B25 300x600  
3-16 $\emptyset$  TOP




3-20 $\emptyset$  BOT. 100 @ 100 c/c

B26 300x600  
3-16 $\emptyset$  TOP




3-20 $\emptyset$  BOT. 100 @ 100 c/c

B27 300x600  
3-16 $\emptyset$  TOP

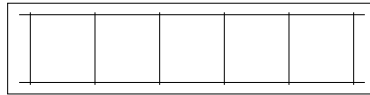


3-20 $\emptyset$  BOT. 100 @ 100 c/c

B28 300x600  
3-16 $\emptyset$  TOP

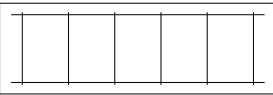


3-20 $\emptyset$  BOT. 100 @ 100 c/c

B29 250x450  
2-16 $\emptyset$  TOP

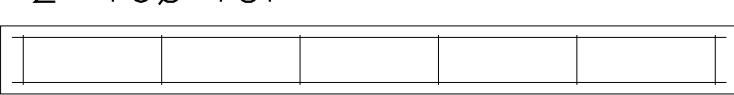


3-16 $\emptyset$  BOT. 100 @ 100 c/c

B30 250x450  
2-16 $\emptyset$  TOP

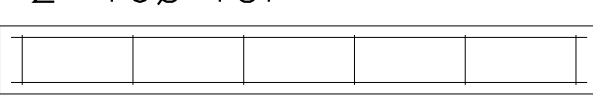


3-16 $\emptyset$  BOT. 100 @ 100 c/c

B31 250x450  
2-16 $\emptyset$  TOP

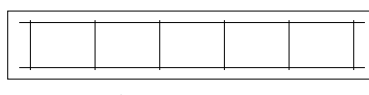


3-16 $\emptyset$  BOT. 100 @ 100 c/c

B32 250x450  
2-16 $\emptyset$  TOP

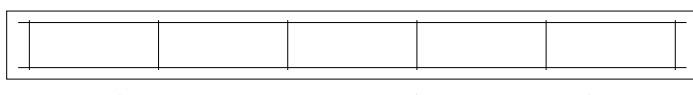


3-16 $\emptyset$  BOT. 100 @ 100 c/c

B33 250x450  
2-16 $\emptyset$  TOP

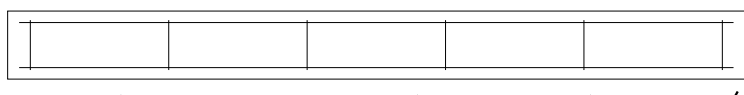


3-16 $\emptyset$  BOT. 100 @ 100 c/c

B34 250x450  
2-16 $\emptyset$  TOP

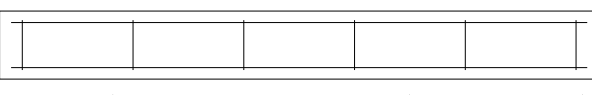


3-16 $\emptyset$  BOT. 100 @ 100 c/c

B35 250x450  
2-16 $\emptyset$  TOP

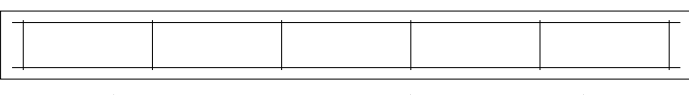


3-16 $\emptyset$  BOT. 100 @ 100 c/c

B36 250x450  
2-16 $\emptyset$  TOP

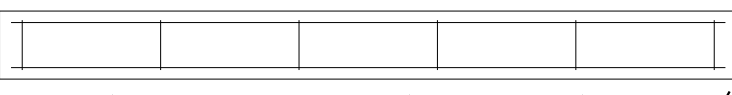


3-16 $\emptyset$  BOT. 100 @ 100 c/c

B37 250x450  
2-16 $\emptyset$  TOP

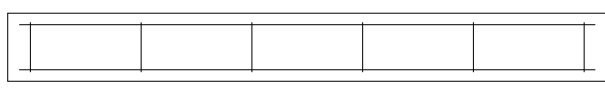


3-16 $\emptyset$  BOT. 100 @ 100 c/c

B38 250x450  
2-16 $\emptyset$  TOP

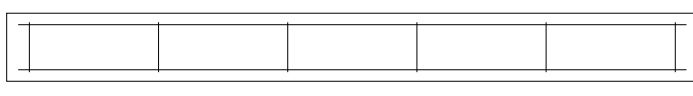


3-16 $\emptyset$  BOT. 100 @ 100 c/c

B39 250x450  
2-16 $\emptyset$  TOP

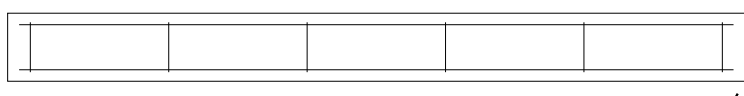


3-16 $\emptyset$  BOT. 100 @ 100 c/c

B40 250x450  
2-16 $\emptyset$  TOP

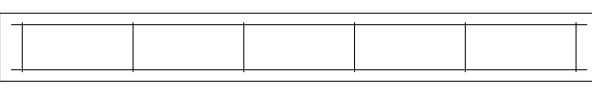


3-16 $\emptyset$  BOT. 100 @ 100 c/c

B41 250x450  
2-16 $\emptyset$  TOP

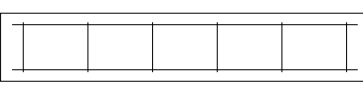


3-16 $\emptyset$  BOT. 100 @ 100 c/c

B42 250x450  
2-16 $\emptyset$  TOP

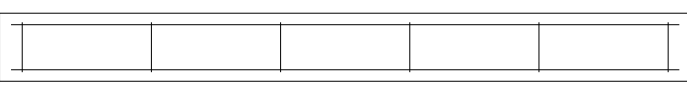

3-16 $\emptyset$  BOT. 100 @ 100 c/c

B43 300x600  
3-16 $\emptyset$  TOP

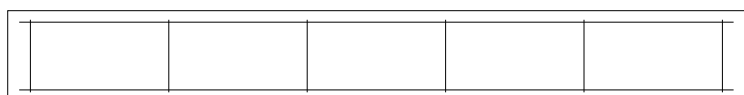


3-20 $\emptyset$  BOT. 100 @ 100 c/c

B44 300x600  
3-16 $\emptyset$  TOP




3-20 $\emptyset$  BOT. 100 @ 100 c/c

B45 300x600  
3-16 $\emptyset$  TOP

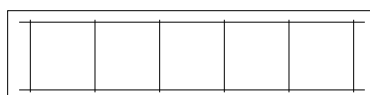

3-20 $\emptyset$  BOT. 100 @ 100 c/c

B46 300x600  
3-16 $\emptyset$  TOP

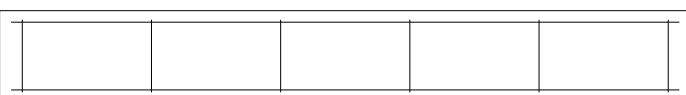

3-20 $\emptyset$  BOT. 100 @ 100 c/c

CB1 250x450  
3-20 $\emptyset$  TOP




2-16 $\emptyset$  BOT. 100 @ 100 c/c

CB2 250x450  
3-20 $\emptyset$  TOP




2-16 $\emptyset$  BOT. 100 @ 100 c/c

CB3 250x450  
3-20 $\emptyset$  TOP

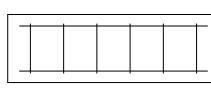


2-16 $\emptyset$  BOT. 100 @ 100 c/c

CB4 250x450  
3-20 $\emptyset$  TOP

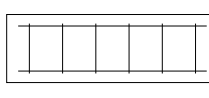


2-16 $\emptyset$  BOT. 100 @ 100 c/c

EB1 250x300  
3-16 $\emptyset$  TOP

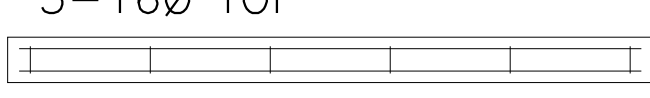


3-16 $\emptyset$  BOT. 100 @ 150 c/c

EB2 250x450  
2-16 $\emptyset$  TOP

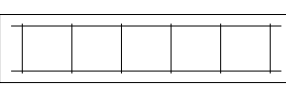

3-16 $\emptyset$  BOT. 100 @ 100 c/c


LB1 250x375  
2-16 $\emptyset$  TOP

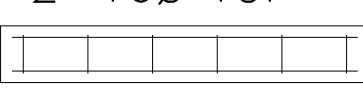

3-16 $\emptyset$  BOT. 100 @ 100 c/c

CONTD. ON S-18

|   |               |                                      |                  |
|---|---------------|--------------------------------------|------------------|
| MEGHNA STRUCTURAL CONSULTANTS LTD.<br>FLAT 4B, HOUSE 27, ROAD 9, SECTOR 6, UTTARA MODEL TOWN, DHAKA<br>TEL +880 1XXX 000 000 / +880 2 4890 0000 |               |                                      |                  |
| CLIENT<br>M/S. PADMA HOMES LTD.   |               |                                      |                  |
| PROJECT<br>PROPOSED G+6 STORIED RESIDENTIAL BUILDING                                                                                            |               |                                      |                  |
| SITE<br>PLOT 23, ROAD 7, BLOCK C, BASHUNDHARA R/A, DHAKA                                                                                        |               |                                      |                  |
| SHEET TITLE<br>BEAM DETAILS (2 OF 3) – TYPICAL                                                                                                  |               |                                      |                  |
| DESIGNED<br>S.R.   | DRAWN<br>M.H. | CHECKED<br>A.K.                      | APPROVED<br>T.I. |
| RAJUK REF. RAJUK/BAP/2026/0417   |               |                                      |                  |
| JOB NO. MSC-2026-041   |               |                                      |                  |
| DATE 12-08-2026   |               |                                      |                  |
| SCALE 1:50   |               |                                      |                  |
| SHEET NO.<br>S-17   |               | REV.<br>B                            |                  |
| REVISIONS   |               |                                      |                  |
| REV   | DATE          | DESCRIPTION                          |                  |
| A   | 05-07-2026    | ISSUED FOR RAJUK APPROVAL            |                  |
| B   | 12-08-2026    | C4, 3RD-4TH BARS REVISED; ISSUED FOR |                  |
| ALL DIMENSIONS IN mm U.N.D.<br>DO NOT SCALE THIS DRAWING                                                                                        |               |                                      |                  |

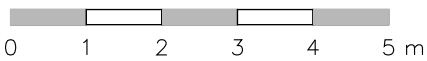



ROOF BEAM SCHEDULE (1 OF 2)      3T16 + 2Y16 (T AND Y BOTH MEAN

| MARK | SIZE    | SPAN (mm) | TOP   | BOTTOM | STIRRUPS |
|------|---------|-----------|-------|--------|----------|
| RB1  | 250x400 | 4572      | 2–16Ø | 3–16Ø  | 10Ø@100  |
| RB2  | 250x400 | 4267      | 2–16Ø | 3–16Ø  | 10Ø@100  |
| RB3  | 250x400 | 2743      | 2–16Ø | 3–16Ø  | 10Ø@100  |
| RB4  | 250x400 | 4267      | 2–16Ø | 3–16Ø  | 10Ø@100  |
| RB5  | 250x400 | 4572      | 2–16Ø | 3–16Ø  | 10Ø@100  |
| RB6  | 250x400 | 4572      | 2–16Ø | 3–16Ø  | 10Ø@100  |
| RB7  | 250x400 | 4267      | 2–16Ø | 3–16Ø  | 10Ø@100  |
| RB8  | 250x400 | 2743      | 2–16Ø | 3–16Ø  | 10Ø@100  |
| RB9  | 250x400 | 4267      | 2–16Ø | 3–16Ø  | 10Ø@100  |
| RB10 | 250x400 | 4572      | 2–16Ø | 3–16Ø  | 10Ø@100  |
| RB11 | 250x400 | 4572      | 2–16Ø | 3–16Ø  | 10Ø@100  |
| RB12 | 250x400 | 4267      | 2–16Ø | 3–16Ø  | 10Ø@100  |
| RB13 | 250x400 | 2743      | 2–16Ø | 3–16Ø  | 10Ø@100  |
| RB14 | 250x400 | 4267      | 2–16Ø | 3–16Ø  | 10Ø@100  |
| RB15 | 250x400 | 4572      | 2–16Ø | 3–16Ø  | 10Ø@100  |
| RB16 | 250x400 | 4572      | 2–16Ø | 3–16Ø  | 10Ø@100  |
| RB17 | 250x400 | 4267      | 2–16Ø | 3–16Ø  | 10Ø@100  |
| RB18 | 250x400 | 4267      | 2–16Ø | 3–16Ø  | 10Ø@100  |
| RB19 | 250x400 | 4572      | 2–16Ø | 3–16Ø  | 10Ø@100  |
| RB20 | 250x400 | 1829      | 2–16Ø | 3–16Ø  | 10Ø@100  |
| RB21 | 250x400 | 4267      | 2–16Ø | 3–16Ø  | 10Ø@100  |
| RB22 | 250x400 | 2743      | 2–16Ø | 3–16Ø  | 10Ø@100  |
| RB23 | 250x400 | 4267      | 2–16Ø | 3–16Ø  | 10Ø@100  |
| RB24 | 250x400 | 4572      | 2–16Ø | 3–16Ø  | 10Ø@100  |
| RB25 | 250x400 | 4877      | 2–16Ø | 3–16Ø  | 10Ø@100  |
| RB26 | 250x400 | 3962      | 2–16Ø | 3–16Ø  | 10Ø@100  |

ROOF BEAM SCHEDULE 1    SCALE 1:50

ROOF BEAM SCHEDULE (2 OF 2)

| MARK  | SIZE    | SPAN (mm) | TOP   | BOTTOM | STIRRUPS |
|-------|---------|-----------|-------|--------|----------|
| RB27  | 250x400 | 2438      | 2–16Ø | 3–16Ø  | 10Ø@100  |
| RB28  | 250x400 | 1829      | 2–16Ø | 3–16Ø  | 10Ø@100  |
| RB29  | 250x400 | 4877      | 2–16Ø | 3–16Ø  | 10Ø@100  |
| RB30  | 250x400 | 3962      | 2–16Ø | 3–16Ø  | 10Ø@100  |
| RB31  | 250x400 | 2438      | 2–16Ø | 3–16Ø  | 10Ø@100  |
| RB32  | 250x400 | 4572      | 2–16Ø | 3–16Ø  | 10Ø@100  |
| RB33  | 250x400 | 4877      | 2–16Ø | 3–16Ø  | 10Ø@100  |
| RB34  | 250x400 | 3962      | 2–16Ø | 3–16Ø  | 10Ø@100  |
| RB35  | 250x400 | 4572      | 2–16Ø | 3–16Ø  | 10Ø@100  |
| RB36  | 250x400 | 4877      | 2–16Ø | 3–16Ø  | 10Ø@100  |
| RB37  | 250x400 | 3962      | 2–16Ø | 3–16Ø  | 10Ø@100  |
| RB38  | 250x400 | 4572      | 2–16Ø | 3–16Ø  | 10Ø@100  |
| RB39  | 250x400 | 4877      | 2–16Ø | 3–16Ø  | 10Ø@100  |
| RB40  | 250x400 | 3962      | 2–16Ø | 3–16Ø  | 10Ø@100  |
| RB41  | 250x400 | 2438      | 2–16Ø | 3–16Ø  | 10Ø@100  |
| RB42  | 250x400 | 4572      | 2–16Ø | 3–16Ø  | 10Ø@100  |
| RB43  | 250x400 | 4877      | 2–16Ø | 3–16Ø  | 10Ø@100  |
| RB44  | 250x400 | 3962      | 2–16Ø | 3–16Ø  | 10Ø@100  |
| RB45  | 250x400 | 2438      | 2–16Ø | 3–16Ø  | 10Ø@100  |
| RB46  | 250x400 | 4572      | 2–16Ø | 3–16Ø  | 10Ø@100  |
| REB2  | 250x400 | 1940      | 2–16Ø | 3–16Ø  | 10Ø@100  |
| SB–R1 | 250x375 | 4267      | 2–16Ø | 3–16Ø  | 10Ø@100  |
| SB–R2 | 250x375 | 4267      | 2–16Ø | 3–16Ø  | 10Ø@100  |
| SB–R3 | 250x375 | 2438      | 2–16Ø | 3–16Ø  | 10Ø@100  |
| SB–R4 | 250x375 | 2743      | 2–16Ø | 3–16Ø  | 10Ø@100  |

ALL ROOF BEAM STIRRUPS 10Ø@150 U.N.O.  
10Ø@100 (ends)  
B9 (CONTD. FROM S–17)

ROOF BEAM SCHEDULE 2    SCALE 1:50

MEGHNA STRUCTURAL CONSULTANT  
S. LTD.  
FLAT #B, HOUSE 27, ROAD 9, SECTOR 6, UTTARA MODEL TOWN, DHAKA  
TEL: +880 1XXXX 000 000 / +880 2 4890 0000

CLIENT  
M/S. PADMA HOMES LTD.

PROJECT  
PROPOSED G+6 STORIED RESIDENTIAL BUILDING

SITE  
PLOT 23, ROAD 7, BLOCK C, BASHUNDHARA R/A, DHAKA

SHEET TITLE  
BEAM DETAILS (3 OF 3) – ROOF & SCHEDULE

DESIGNED  
S.R.

DRAWN  
M.H.

CHECKED  
A.K.

APPROVED  
T.I.

RAJUK REF. RAJUK/BAP/2026/0417

JOB NO. MSC–2026–041

DATE 12–08–2026

SCALE 1:50


SHEET NO.  
S–18

REV.  
B



REVISIONS  

| REV | DATE       | DESCRIPTION                         |
|-----|------------|-------------------------------------|
| A   | 05–07–2026 | ISSUED FOR RAJUK APPROVAL           |
| B   | 12–08–2026 | 24–3RD–4TH BARS REVISED; ISSUED FOR |


ALL DIMENSIONS IN mm U.N.O.  
DO NOT SCALE THIS DRAWING

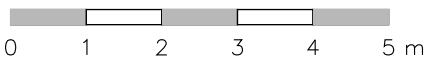




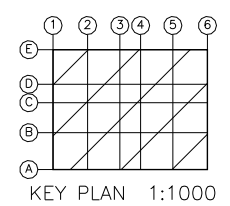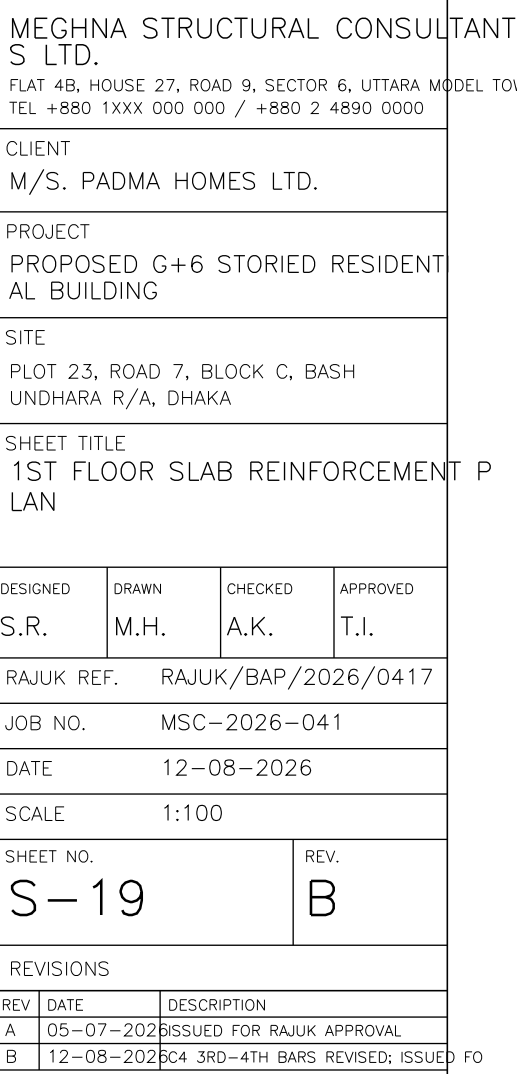




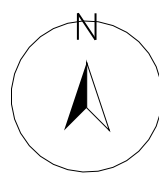


|   |               |                                     |                  |
|---|---------------|-------------------------------------|------------------|
| MEGHNA STRUCTURAL CONSULTANT<br>S. LTD.<br>FLAT 4B, HOUSE 27, ROAD 9, SECTOR 6, UTTARA MODEL TOWN, DHAKA<br>TEL: +880 1XXX 000 000 / +880 2 4890 0000 |               |                                     |                  |
| CLIENT<br>M/S. PADMA HOMES LTD.   |               |                                     |                  |
| PROJECT<br>PROPOSED G+6 STORIED RESIDENTIAL BUILDING                                                                                                  |               |                                     |                  |
| SITE<br>PLOT 23, ROAD 7, BLOCK C, BASHUNDHARA R/A, DHAKA                                                                                              |               |                                     |                  |
| SHEET TITLE<br>TYPICAL SLAB REINFORCEMENT PLAN   |               |                                     |                  |
| DESIGNED<br>S.R.   | DRAWN<br>M.H. | CHECKED<br>A.K.                     | APPROVED<br>T.I. |
| RAJUK REF. RAJUK/BAP/2026/0417   |               |                                     |                  |
| JOB NO. MSC-2026-041   |               |                                     |                  |
| DATE 12-08-2026   |               |                                     |                  |
| SCALE 1:100   |               |                                     |                  |
| SHEET NO.<br>S-20   |               | REV.<br>B                           |                  |
| REVISIONS   |               |                                     |                  |
| REV.   | DATE          | DESCRIPTION                         |                  |
| A   | 05-07-2026    | ISSUED FOR RAJUK APPROVAL           |                  |
| B   | 12-08-2026    | C4 3RD-4TH BARS REVISED; ISSUED FOR |                  |

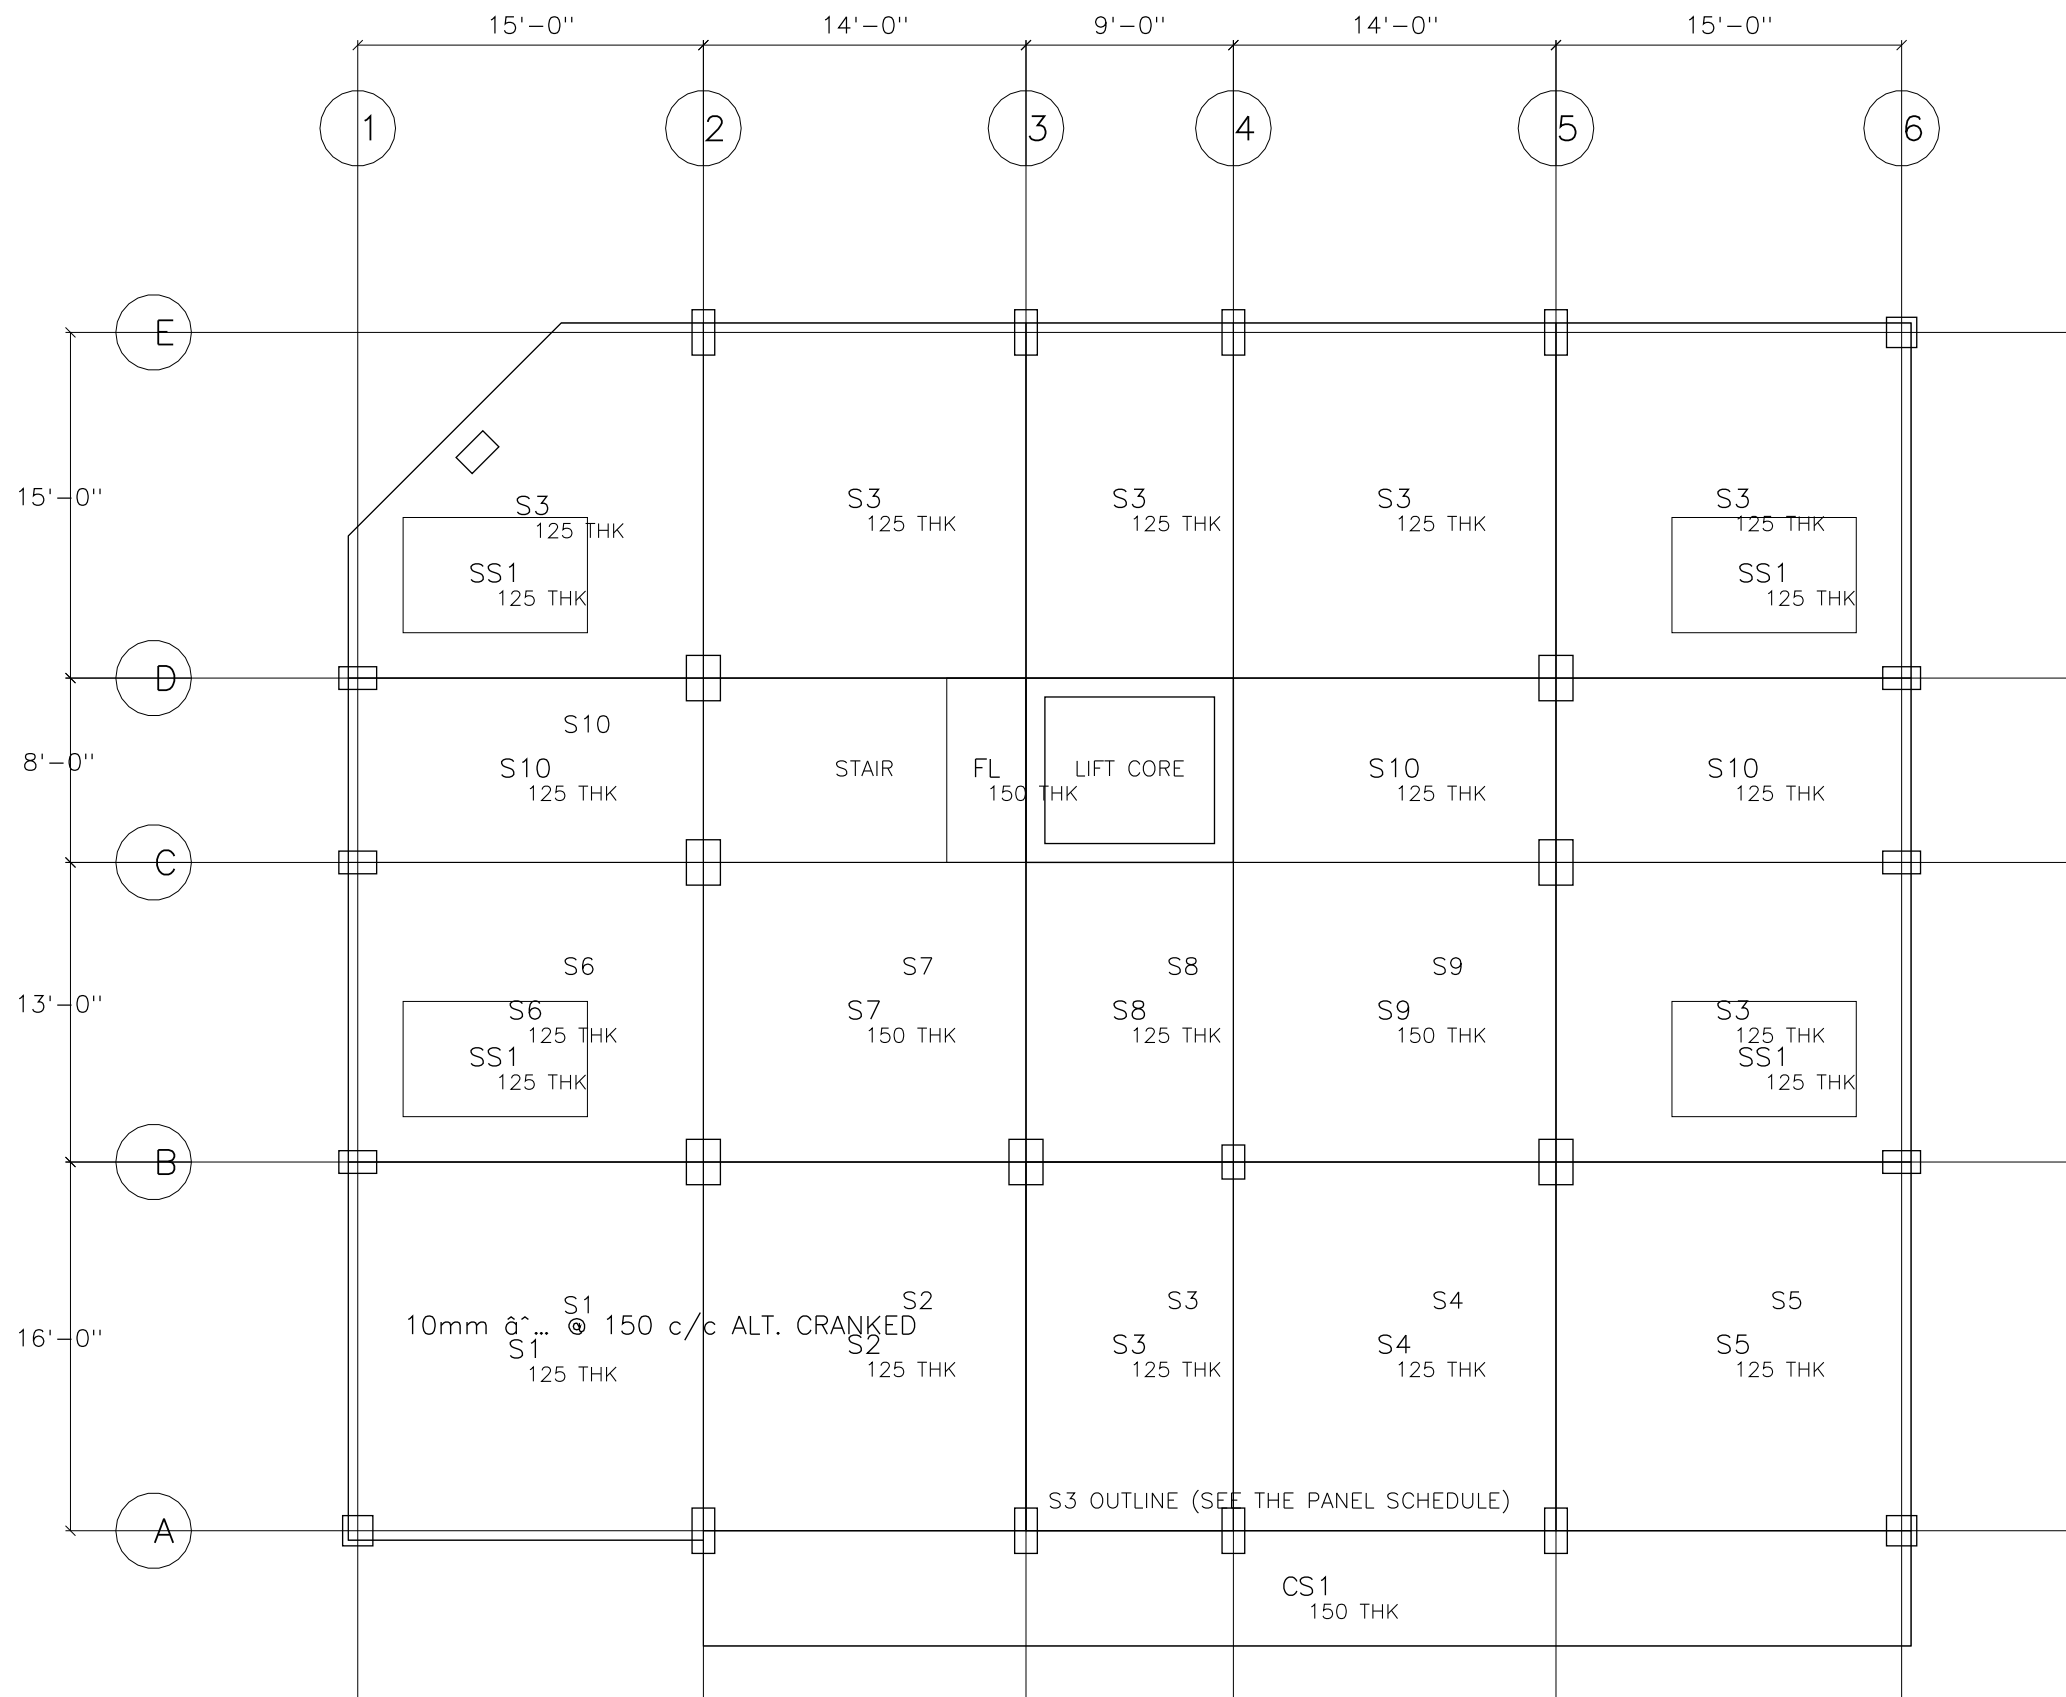


TYPICAL SLAB REINFORCEMENT PLAN



TYPICAL SLAB REINFORCEMENT PLAN SCALE 1:100

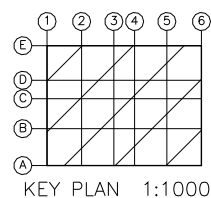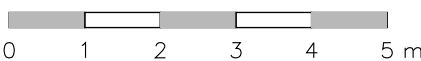




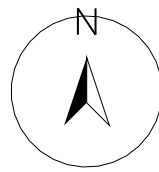


|   |               |                                                    |                  |
|---|---------------|----------------------------------------------------|------------------|
| MEGHNA STRUCTURAL CONSULTANTS LTD.<br>FLAT 4B, HOUSE 27, ROAD 9, SECTOR 6, UTTARA MODEL TOWN, DHAKA<br>TEL: +880 1XXX 000 000 / +880 2 4890 0000 |               |                                                    |                  |
| CLIENT<br>M/S. PADMA HOMES LTD.   |               |                                                    |                  |
| PROJECT<br>PROPOSED G+6 STORED RESIDENTIAL BUILDING                                                                                              |               |                                                    |                  |
| SITE<br>PLOT 23, ROAD 7, BLOCK C, BASHUNDHARA R/A, DHAKA                                                                                         |               |                                                    |                  |
| SHEET TITLE<br>ROOF, STAIR ROOF & PARAPET   |               |                                                    |                  |
| DESIGNED<br>S.R.   | DRAWN<br>M.H. | CHECKED<br>A.K.                                    | APPROVED<br>T.I. |
| RAJUK REF. RAJUK/BAP/2026/0417   |               |                                                    |                  |
| JOB NO. MSC-2026-041   |               |                                                    |                  |
| DATE 12-08-2026   |               |                                                    |                  |
| SCALE 1:100, 1:20   |               |                                                    |                  |
| SHEET NO.<br>S-21   |               | REV.<br>B                                          |                  |
| REVISIONS   |               |                                                    |                  |
| REV   | DATE          | DESCRIPTION                                        |                  |
| A   | 05-07-2026    | ISSUED FOR RAJUK APPROVAL                          |                  |
| B   | 12-08-2026    | C4 3RD-4TH BARS REVISED; ISSUED FOR RAJUK APPROVAL |                  |

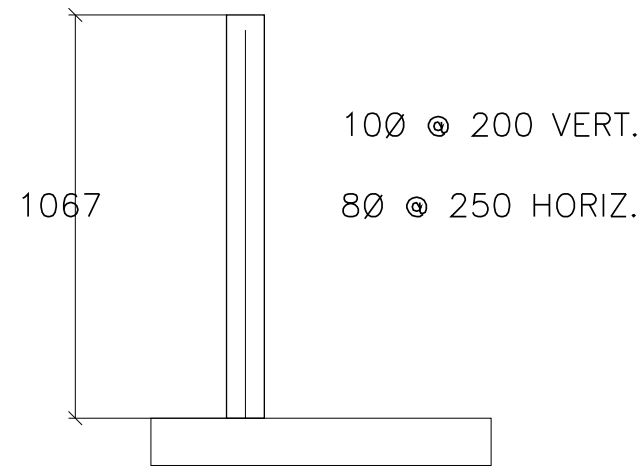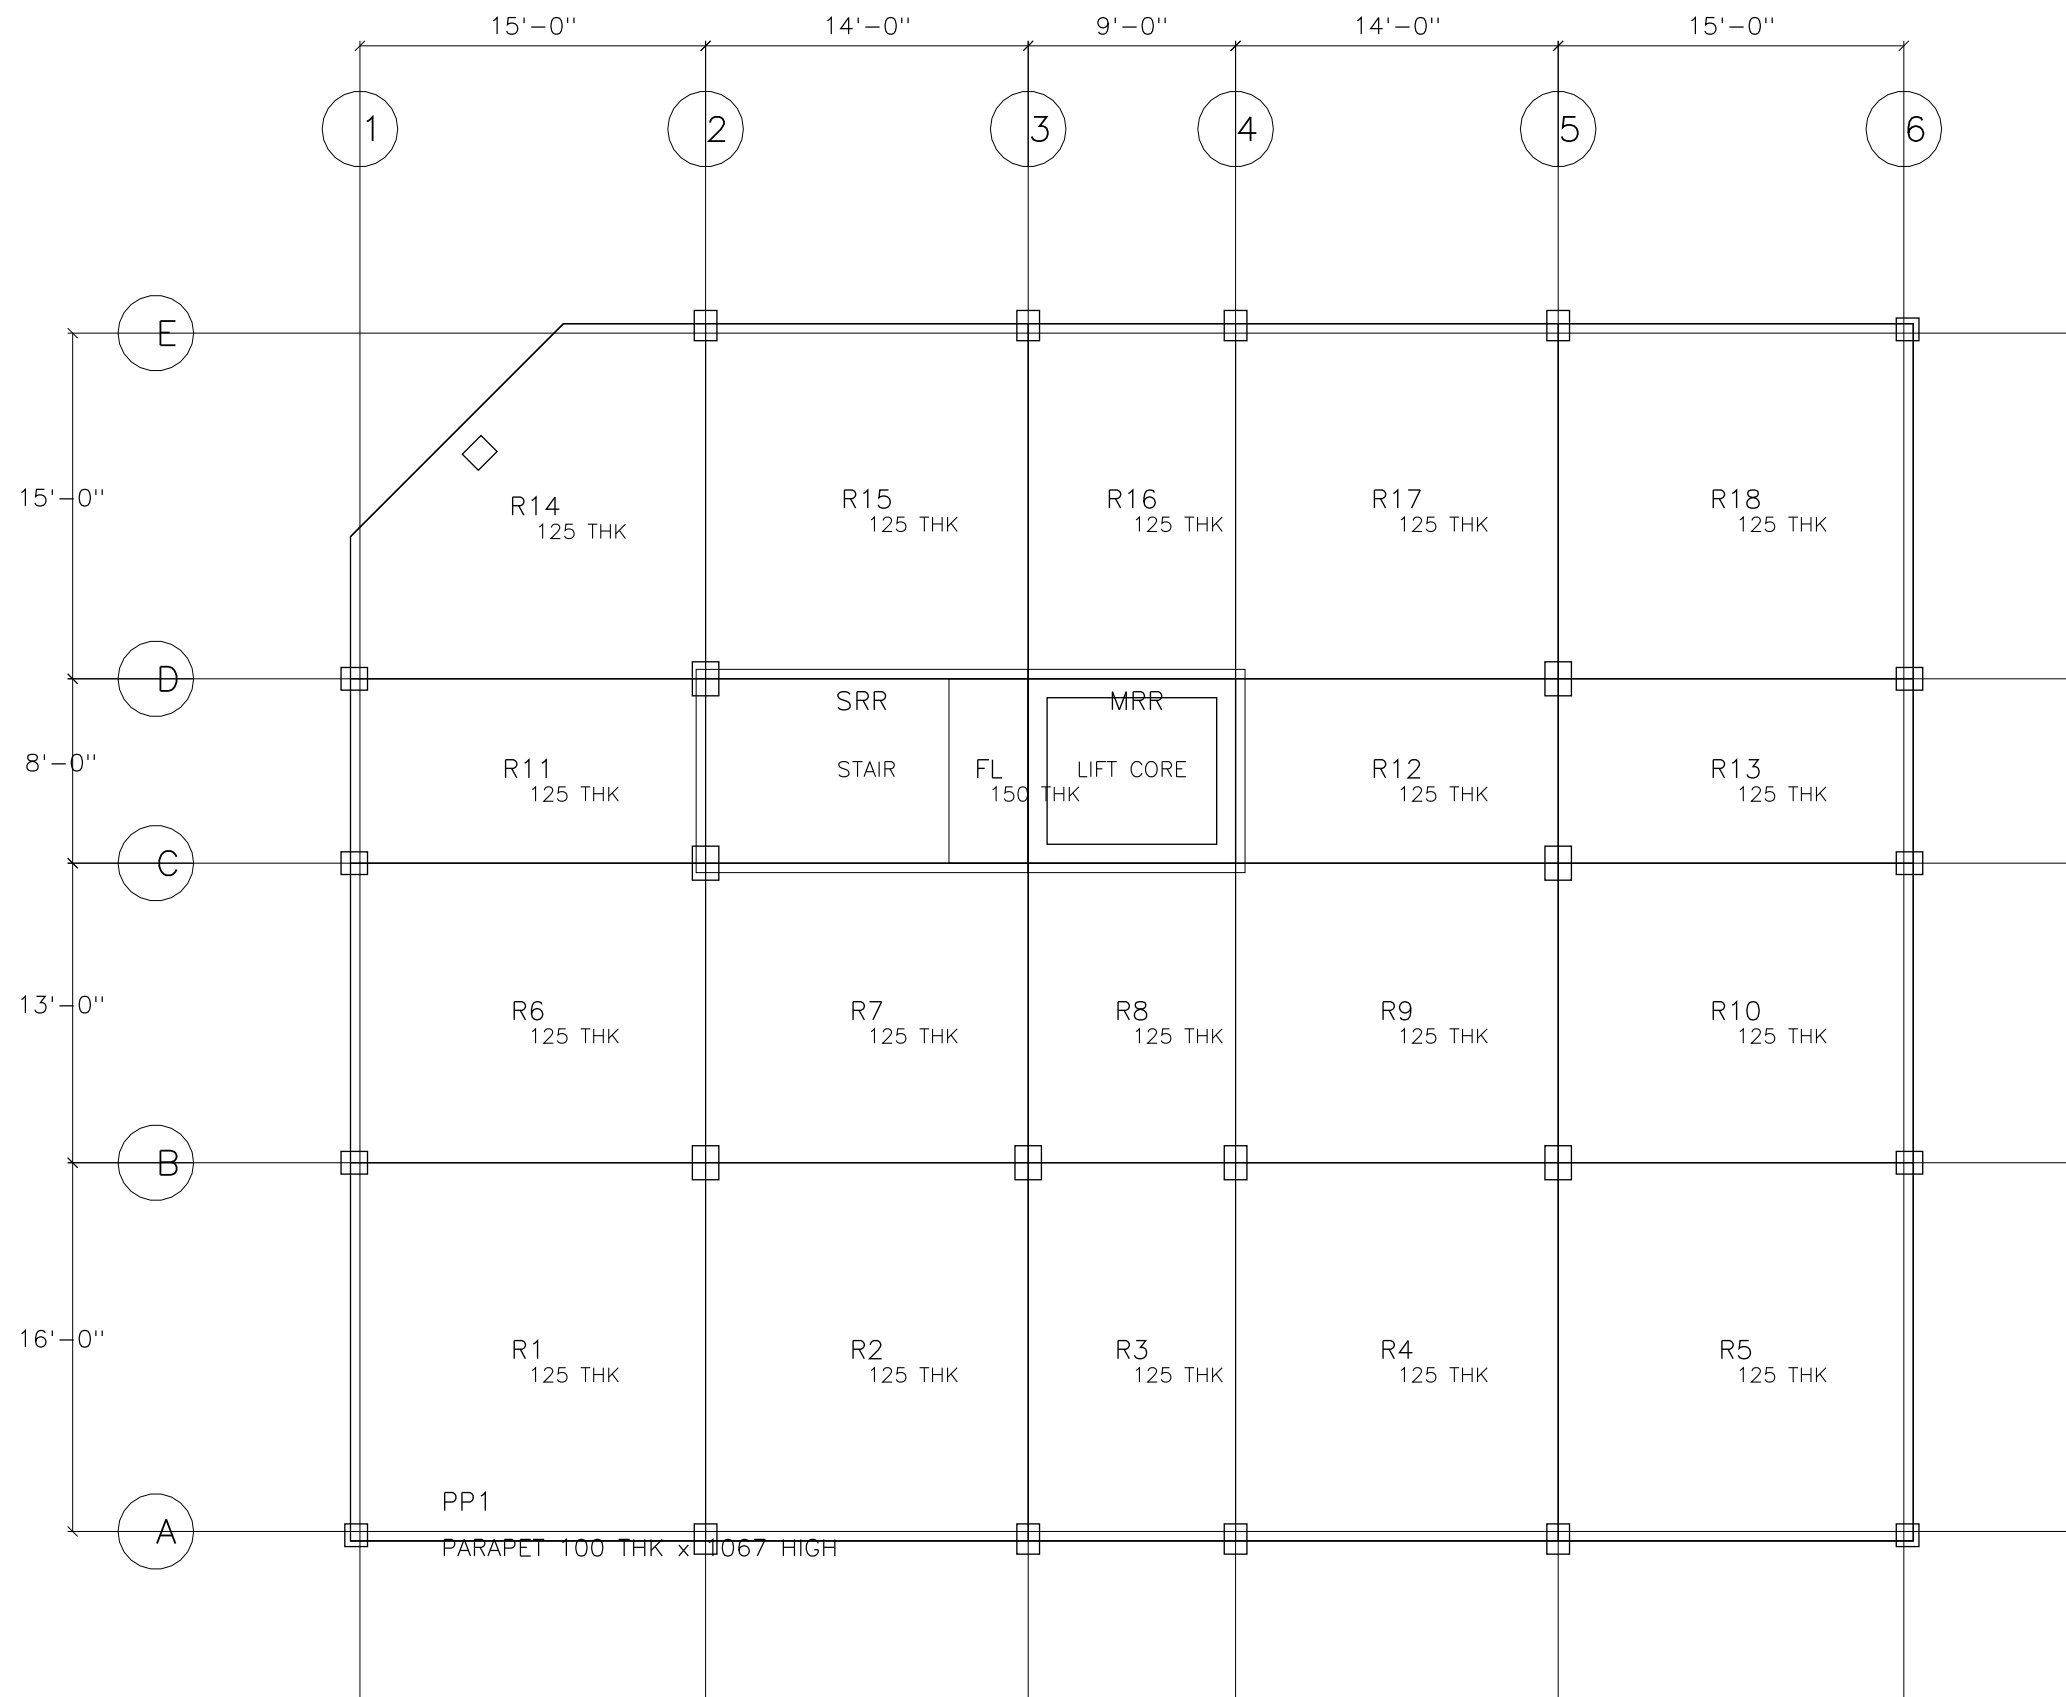


PARAPET DETAIL SCALE 1:20

ROOF & STAIR ROOF PLAN SCALE 1:100

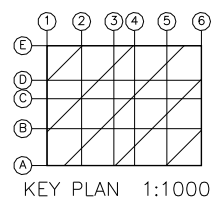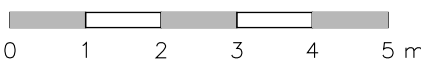




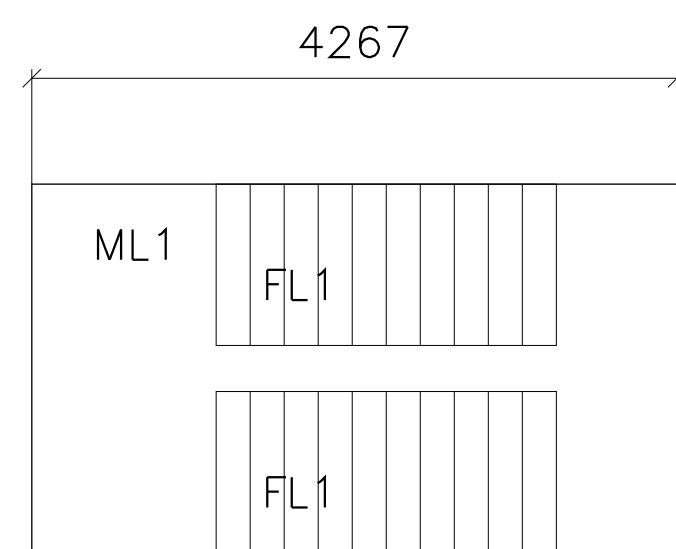


20 R @ 167.64 GOING 250

STAIR PLAN AT GROUND FLOOR SCALE 1:50

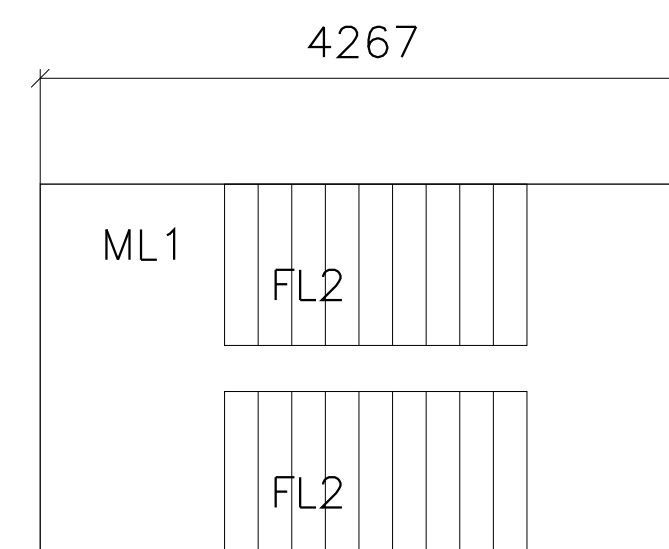

18 R @ 169.33 GOING 250

STAIR PLAN AT 1ST FLOOR (TYPICAL) SCALE 1:50

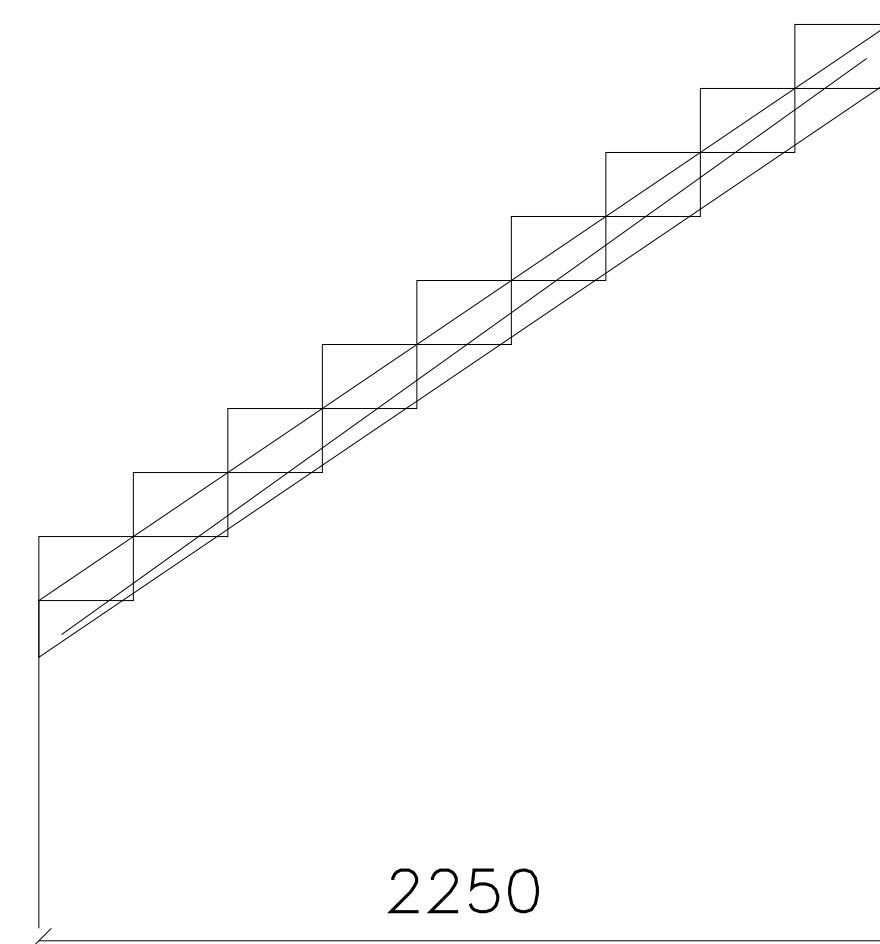

120 @ 125 c/c MAIN

80 @ 200 c/c DIST.

WAIST 150

FLIGHT WIDTH 3'-6½"

WELL 304 LANDING 1219


STAIR SECTION SCALE 1:20





|   |            |                                                 |          |
|---|------------|-------------------------------------------------|----------|
| MEGHNA STRUCTURAL CONSULTANTS LTD.   |            |                                                 |          |
| FLAT 4B, HOUSE 27, ROAD 9, SECTOR 6, UTTARA MODEL TOWNSHIP, KOLKATA-700016, WEST BENGAL, INDIA<br>TEL. +880 1XXXX 000 000 / +880 2 4890 0000 |            |                                                 |          |
| CLIENT<br>M/S. PADMA HOMES LTD.   |            |                                                 |          |
| PROJECT<br>PROPOSED G+6 STORIED RESIDENTIAL BUILDING                                                                                         |            |                                                 |          |
| SITE<br>PLOT 23, ROAD 7, BLOCK C, BASHUNDHARA R/A, DHAKA                                                                                     |            |                                                 |          |
| SHEET TITLE<br>STAIR DETAILS   |            |                                                 |          |
| DESIGNED   | DRAWN      | CHECKED                                         | APPROVED |
| S.R.   | M.H.       | A.K.                                            | T.I.     |
| RAJUK REF. RAJUK/BAP/2026/0417   |            |                                                 |          |
| JOB NO. MSC-2026-041   |            |                                                 |          |
| DATE 12-08-2026   |            |                                                 |          |
| SCALE 1:50, 1:20   |            |                                                 |          |
| SHEET NO.<br>S-22   |            | REV.<br>B                                       |          |
| REVISIONS   |            |                                                 |          |
| REV.   | DATE       | DESCRIPTION                                     |          |
| A   | 05-07-2022 | ISSUED FOR RAJUK APPROVAL                       |          |
| B   | 12-08-2026 | 3RD-4TH BARS REVISED, ISSUED FOR RAJUK APPROVAL |          |



SHEAR WALL 250 THK (LOWER), 200 THK ABOVE 4I

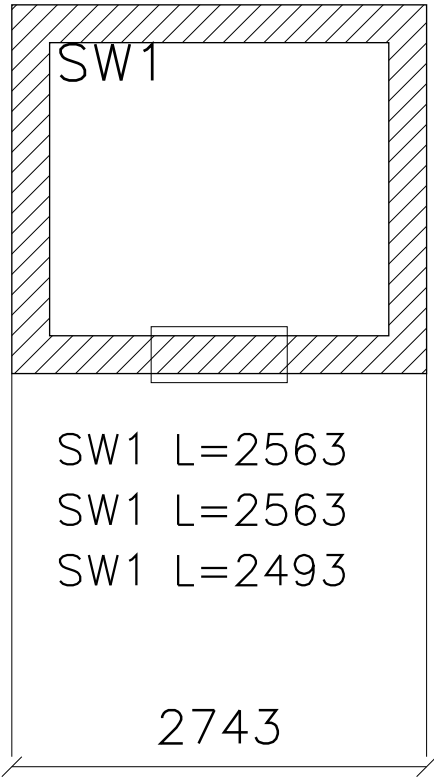

LIFT CORE PLAN SCALE 1:50

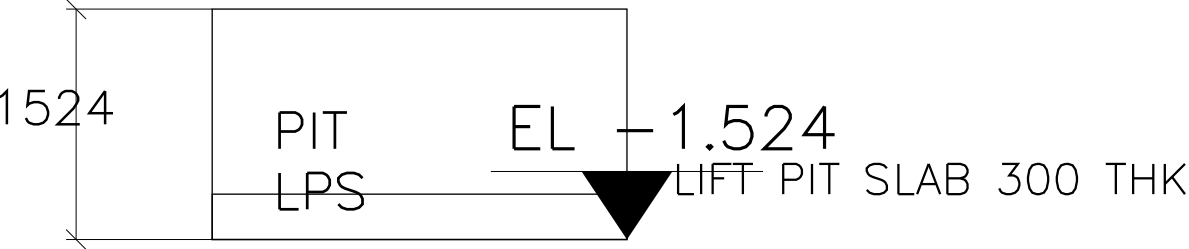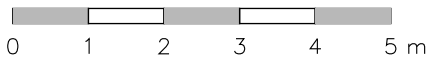


LIFT PIT SECTION SCALE 1:50

|   |               |                                     |                  |
|---|---------------|-------------------------------------|------------------|
| MEGHNA STRUCTURAL CONSULTANT<br>S LTD.<br>FLAT 4B, HOUSE 27, ROAD 9, SECTOR 6, UTTARA MODEL TOWN, DHAKA<br>TEL +880 1XXX 000 000 / +880 2 4890 0000 |               |                                     |                  |
| CLIENT<br>M/S. PADMA HOMES LTD.   |               |                                     |                  |
| PROJECT<br>PROPOSED G+6 STORIED RESIDENTIAL BUILDING                                                                                                |               |                                     |                  |
| SITE<br>PLOT 23, ROAD 7, BLOCK C, BASHUNDHARA R/A, DHAKA                                                                                            |               |                                     |                  |
| SHEET TITLE<br>LIFT CORE & SHEAR WALL DETAILS   |               |                                     |                  |
| DESIGNED<br>S.R.   | DRAWN<br>M.H. | CHECKED<br>A.K.                     | APPROVED<br>T.I. |
| RAJUK REF.<br>RAJUK/BAP/2026/0417   |               | JOB NO.<br>MSC-2026-041             |                  |
| DATE<br>12-08-2026   |               | SCALE<br>1:50                       |                  |
| SHEET NO.<br>S-23   |               | REV.<br>B                           |                  |
| REVISIONS   |               |                                     |                  |
| REV.   | DATE          | DESCRIPTION                         |                  |
| A   | 05-07-2026    | ISSUED FOR RAJUK APPROVAL           |                  |
| B   | 12-08-2026    | C4 3RD-4TH BARS REVISED; ISSUED FOR |                  |
| ALL DIMENSIONS IN mm U.N.D.<br>DO NOT SCALE THIS DRAWING                                                                                            |               |                                     |                  |




OVERHEAD WATER TANK

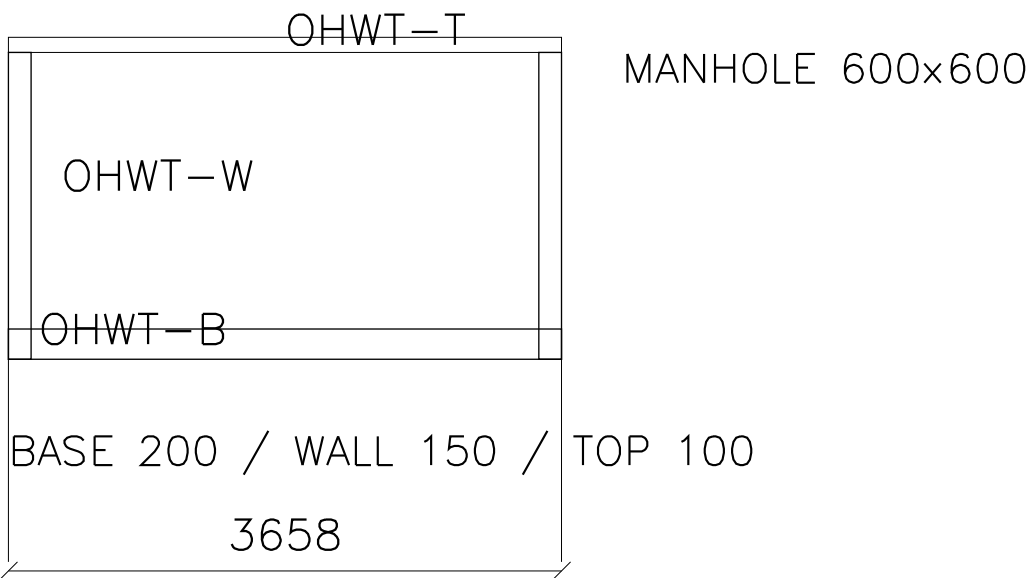


OVERHEAD WATER TANK SCALE 1:50

UNDERGROUND WATER RESERVOIR

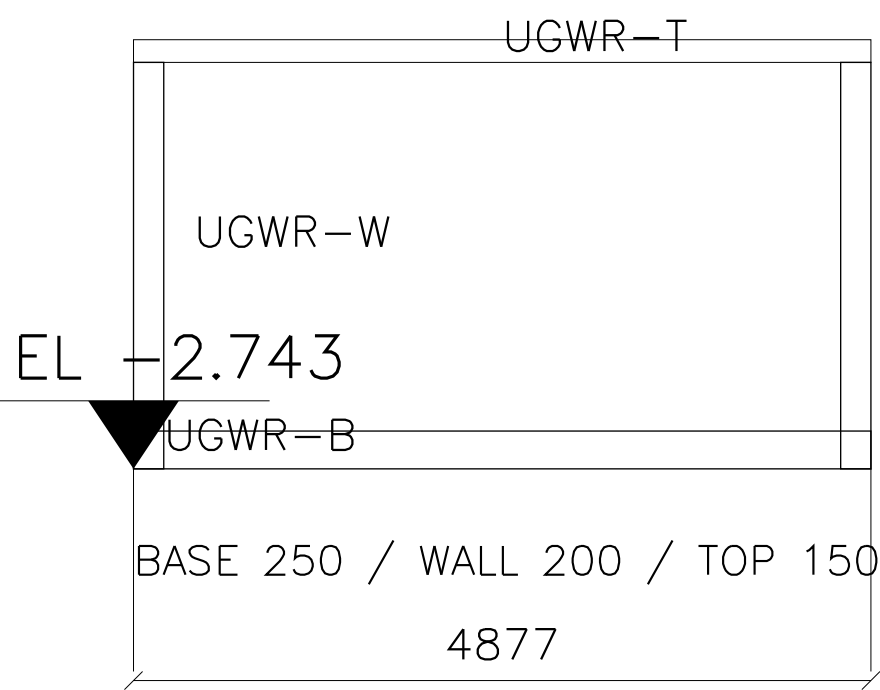


UNDERGROUND WATER RESERVOIR SCALE 1:50

SEPTIC TANK

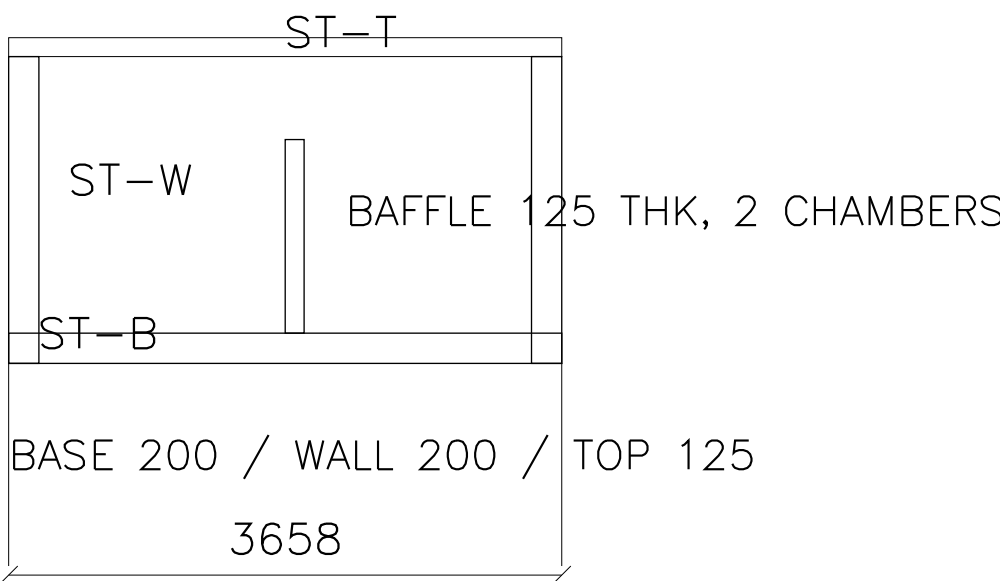

SEPTIC TANK SCALE 1:50

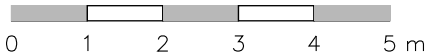

MEGHNA STRUCTURAL CONSULTANT  
S. LTD.  
FLAT 4B, HOUSE 27, ROAD 9, SECTOR 6, UTTARA MODEL TOWN, DHAKA  
TEL: +880 1XXX 000 000 / +880 2 4890 0000

CLIENT  
M/S. PADMA HOMES LTD.

PROJECT  
PROPOSED G+6 STORIED RESIDENTIAL BUILDING

SITE  
PLOT 23, ROAD 7, BLOCK C, BASHUNDHARA R/A, DHAKA

SHEET TITLE  
OVERHEAD WATER TANK & UGWR / SEPTIC TANK

DESIGNED  
S.R.

DRAWN  
M.H.

CHECKED  
A.K.

APPROVED  
T.I.

RAJUK REF. RAJUK/BAP/2026/0417

JOB NO. MSC-2026-041

DATE 12-08-2026

SCALE 1:50

SHEET NO.  
S-24

REV.  
B

REVISIONS

REV. DATE DESCRIPTION

A 05-07-2026 ISSUED FOR RAJUK APPROVAL

B 12-08-2026 C4 3RD-4TH BARS REVISED; ISSUED FOR

ALL DIMENSIONS IN mm U.N.D.  
DO NOT SCALE THIS DRAWING



LINTEL & SUNSHADE SCHEDULE


MARK                      SIZE                      BARS                      OPENING (mm)

|     |         |                               |     |     |     |
|-----|---------|-------------------------------|-----|-----|-----|
| L1  | 250x150 | 2–12%<br>%C T&B + 8%<br>%1000 | 150 | L1  | OVE |
| L2  | 250x200 | 2–12%<br>%C T&B + 8%<br>%1200 | 150 | L2  | OVE |
| LS1 | 250x200 | 2–12%<br>%C T&B + 8%<br>%1500 | 150 | LS1 | OVE |

BW250    BRICK WALL 250 THK                      BW250


BW125    BRICK WALL 125 THK                      BW125

LINTEL & SUNSHADE SCHEDULE    SCALE 1:50

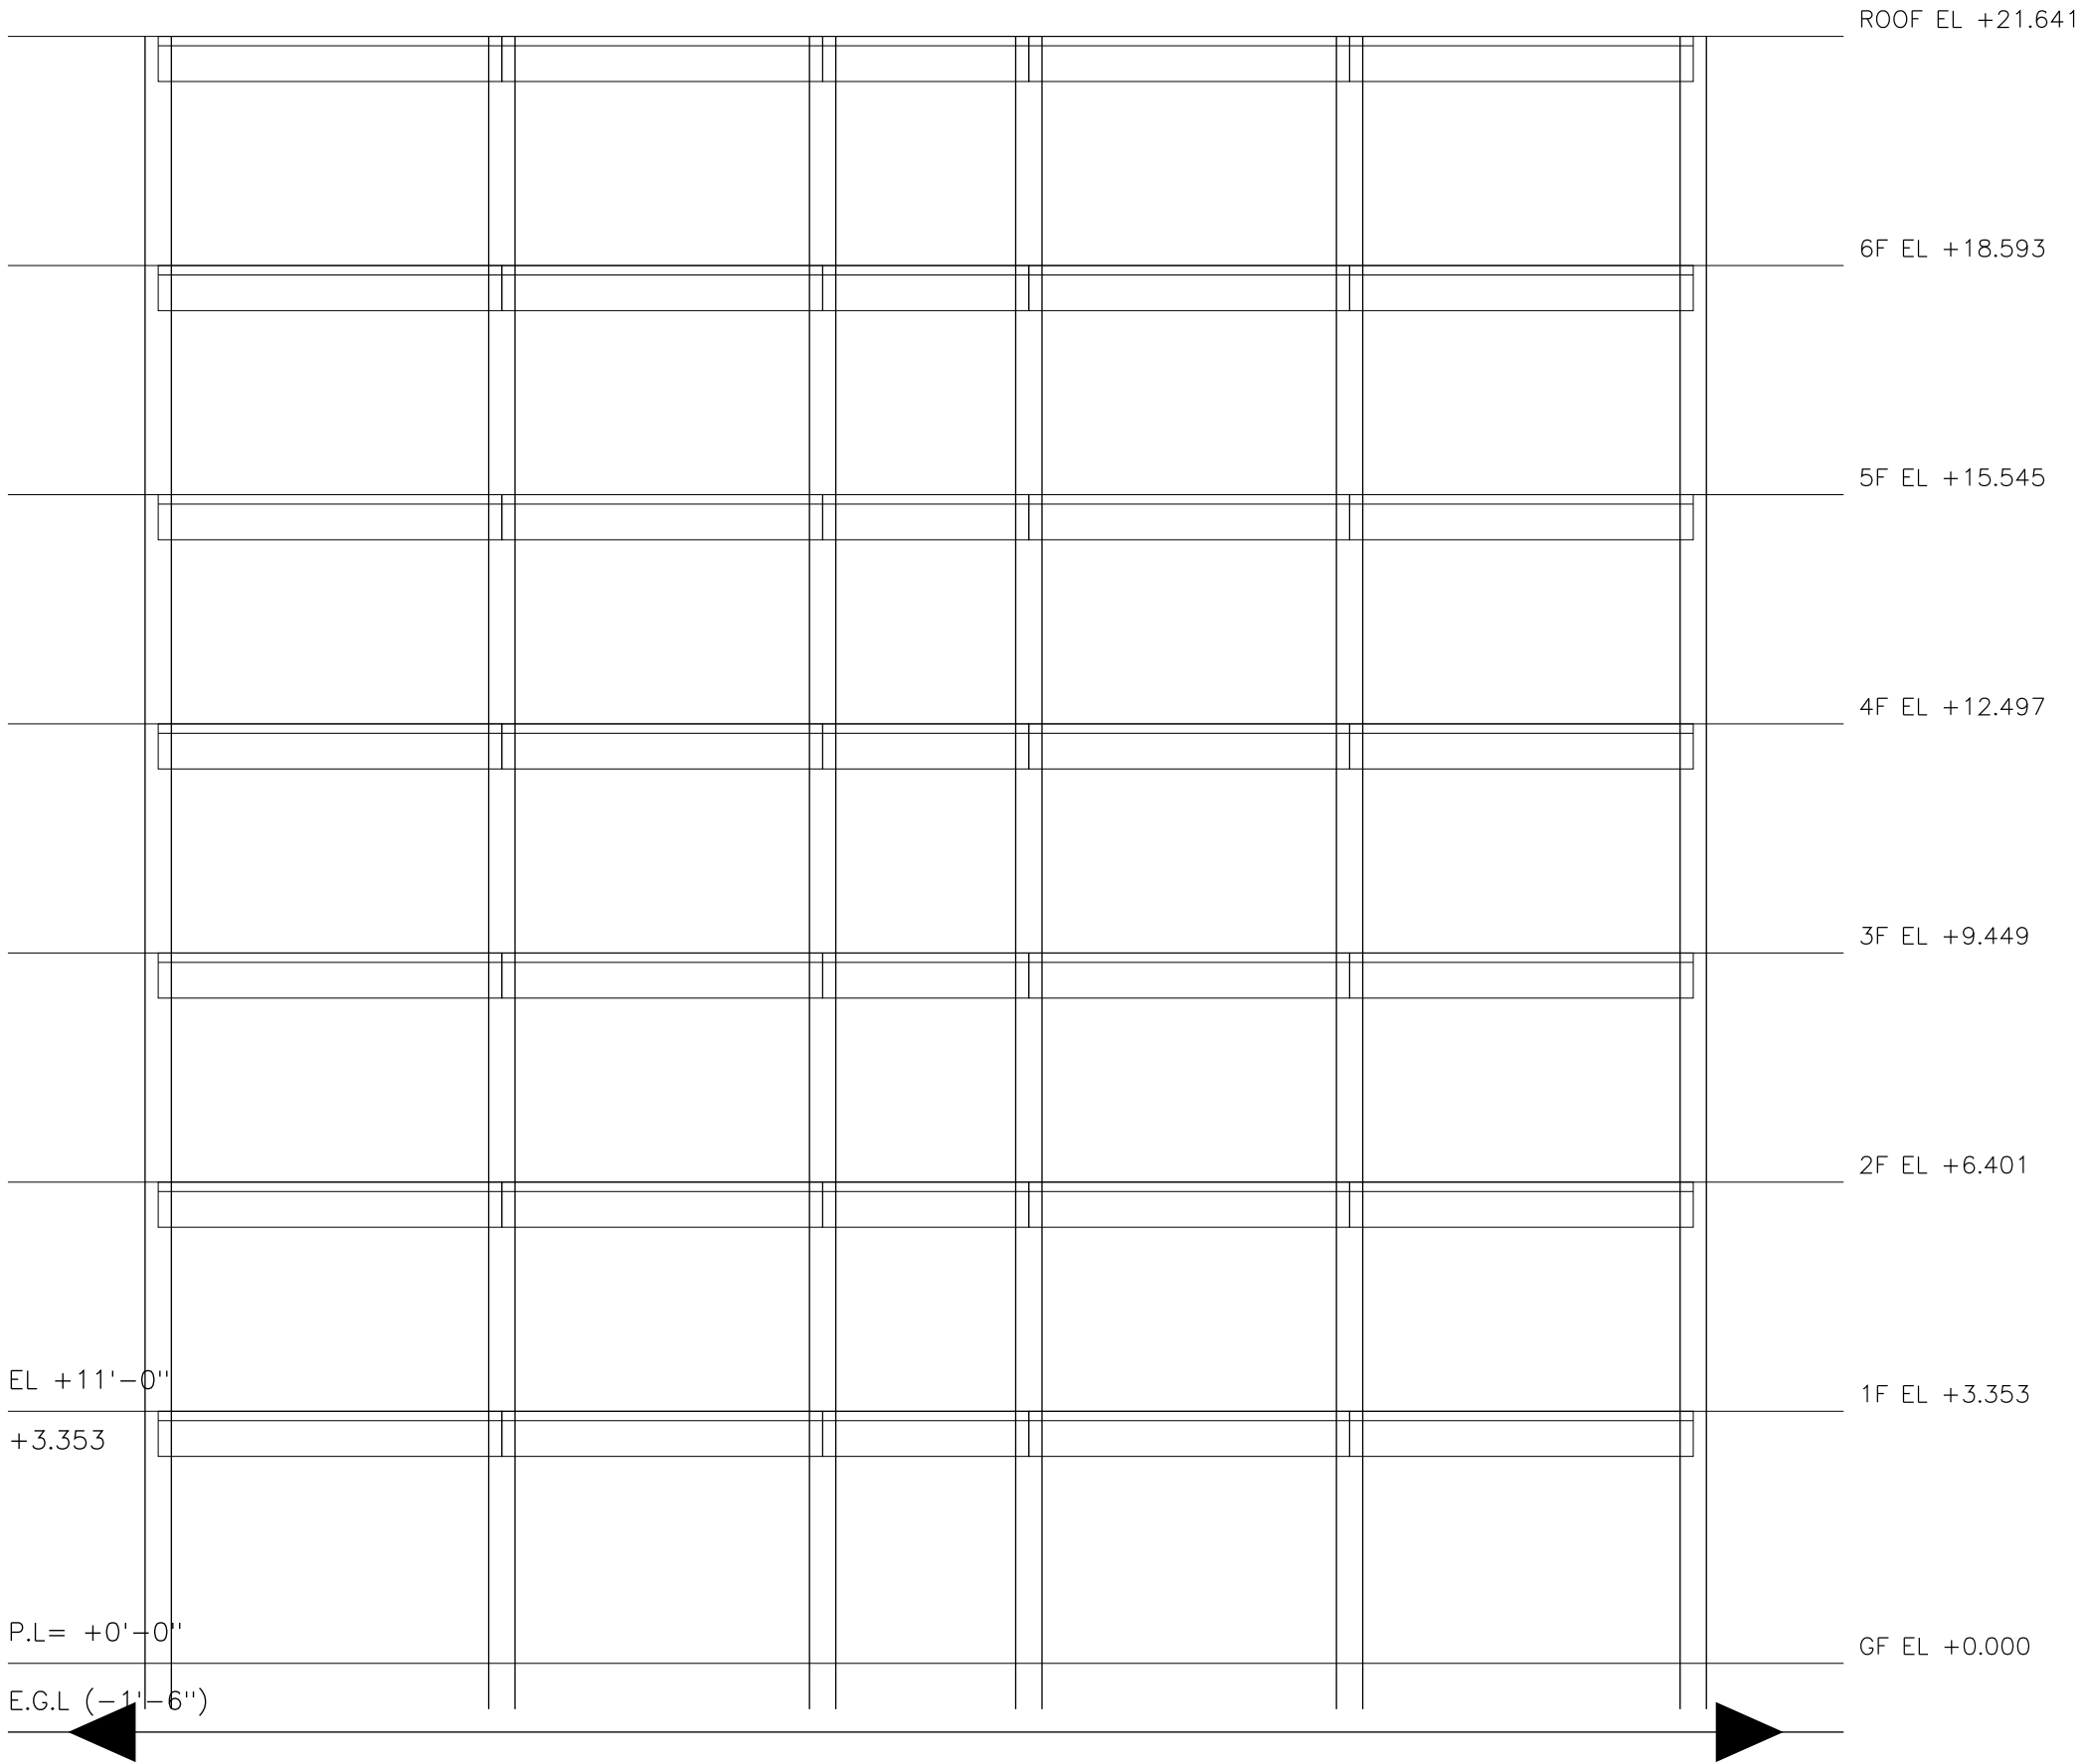

SECTION A–A

BUILDING SECTION A–A    SCALE 1:100

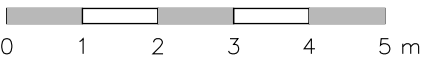

MEGHNA STRUCTURAL CONSULTANTS LTD.

FLAT 4B, HOUSE 27, ROAD 9, SECTOR 6, UTTARA MODEL TOWN  
 TEL: +880 1XXX 000 000 / +880 2 4890 0000

CLIENT

M/S. PADMA HOMES LTD.

PROJECT

PROPOSED G+6 STORIED RESIDENTIAL BUILDING

SITE

PLOT 23, ROAD 7, BLOCK C, BASHUNDHARA R/A, DHAKA

SHEET TITLE

LINTEL & SUNSHADE SCHEDULE, BUILDING SECTION

DESIGNED

DRAWN

CHECKED

APPROVED

S.R.

M.H.

A.K.

T.I.

RAJUK REF.

RAJUK/BAP/2026/0417

JOB NO.

MSC-2026-041

DATE

12-08-2026

SCALE

1:100

SHEET NO.

S-25

REV.

B

REVISIONS

| REV | DATE       | DESCRIPTION                         |
|-----|------------|-------------------------------------|
| A   | 05-07-2026 | ISSUED FOR RAJUK APPROVAL           |
| B   | 12-08-2026 | 24-3RD-4TH BARS REVISED; ISSUED FOR |

ALL DIMENSIONS IN mm U.N.D.

DO NOT SCALE THIS DRAWING

BAR BENDING SCHEDULE (SAMPLE)

BS 8666 CUTTING LENGTHS; LAPS AND HOOKS PER THE S-02 TABLE

| MEMBER | BAR MARK | SHAPE | DIA | A / B / C (mm)                                               | CUT LENGTH | NOS | MASS (kg) |
|--------|----------|-------|-----|--------------------------------------------------------------|------------|-----|-----------|
| PC3    | PC3-bx   | 21    | 16Ø | A=192.000/B=1850.000/C=24152.000                             | 24152.000  | 15  | 51.396    |
| PC3    | PC3-by   | 21    | 16Ø | A=192.000/B=1850.000/C=24152.000                             | 24152.000  | 15  | 51.396    |
| PC3    | PC3-tx   | 21    | 12Ø | A=144.000/B=1850.000/C=24044.000                             | 24044.000  | 10  | 18.559    |
| PC3    | PC3-ty   | 21    | 12Ø | A=144.000/B=1850.000/C=24044.000                             | 24044.000  | 10  | 18.559    |
| PC3    | PC3-s    | 00    | 12Ø | A=7400.000                                                   | 7400       | 3   | 19.714    |
|        |          |       |     |                                                              |            |     |           |
| 2B7    | B7-b     | 00    | 16Ø | A=5417.200                                                   | 5425       | 3   | 25.661    |
| 2B7    | B7-bx    | 00    | 16Ø | A=1908.600                                                   | 1925       | 2   | 6.027     |
| 2B7    | B7-t     | 00    | 16Ø | A=5897.200                                                   | 5900       | 2   | 18.623    |
| 2B7    | B7-tx1   | 00    | 20Ø | A=2336.800                                                   | 2350       | 2   | 11.525    |
| 2B7    | B7-s     | 51    | 10Ø | A=200.000/B=400.000/C=4200.000/D=400.000/E=100.000/F=100.000 | 4200       | 3   | 26.426    |
|        |          |       |     |                                                              |            |     |           |
| S3     | S3-bx    | 21    | 10Ø | A=120.000/B=2703.200/C=29125.000                             | 29125.000  | 17  | 30.402    |
| S3     | S3-cx    | CRK   | 10Ø | A=2703.200/B=35.700/C=2350.000                               | 2350.000   | 16  | 26.558    |
| S3     | S3-tx    | 11    | 10Ø | A=1371.600/B=120.000                                         | 1475       | 66  | 59.829    |
| S3     | S3-by    | 21    | 10Ø | A=120.000/B=4836.800/C=59520.000                             | 59520.000  | 10  | 31.027    |
| S3     | S3-cy    | CRK   | 10Ø | A=4836.800/B=35.700/C=4850.000                               | 4850.000   | 9   | 26.768    |
| S3     | S3-ty    | 11    | 10Ø | A=2438.400/B=120.000                                         | 2550       | 38  | 59.419    |
|        |          |       |     |                                                              |            |     |           |

GRAND TOTAL (KG) 490.081  
(THE ROW SUMS ARE THE TRUTH; THIS TOTAL IS THE TYPIST'S)

MEGHNA STRUCTURAL CONSULTANTS LTD.  
FLAT 4B, HOUSE 27, ROAD 9, SECTOR 6, UTTARA MODEL TOWN, DHAKA  
TEL +880 1XXX 000 000 / +880 2 4890 0000

CLIENT  
M/S. PADMA HOMES LTD.

PROJECT  
PROPOSED G+6 STORIED RESIDENTIAL BUILDING

SITE  
PLOT 23, ROAD 7, BLOCK C, BASHUNDHARA R/A, DHAKA

SHEET TITLE  
BAR BENDING SCHEDULE (SAMPLE: PC3, 2B7, SLAB S3)

DESIGNED  
S.R.

DRAWN  
M.H.

CHECKED  
A.K.

APPROVED  
T.I.

RAJUK REF. RAJUK/BAP/2026/0417

JOB NO. MSC-2026-041

DATE 12-08-2026

SCALE N.T.S.

SHEET NO.  
S-26

REV.  
B

REVISIONS

| REV | DATE       | DESCRIPTION                          |
|-----|------------|--------------------------------------|
| A   | 05-07-2026 | ISSUED FOR RAJUK APPROVAL            |
| B   | 12-08-2026 | PC4 3RD-4TH BARS REVISED; ISSUED FOR |

ALL DIMENSIONS IN mm U.N.O.  
DO NOT SCALE THIS DRAWING