




PROPOSED G+6 STORIED RESIDENTIAL BUILDING


PLOT 23, ROAD 7, BLOCK C, BASHUNDHARA R/A, DHAKA
FOR M/S. PADMA HOMES LTD.
RAJUK REF. RAJUK/BAP/2026/0417

DRAWING INDEX

SHEET	TITLE	SIZE	SCALE	REV
S-00	COVER, DRAWING INDEX & KEY PLAN	A2	N.T.S.	B
S-01	GENERAL NOTES (1 OF 2)	A2	N.T.S.	B
S-02	GENERAL NOTES (2 OF 2) & LAP/DEVELOPMENT TABLE	A2	N.T.S.	B
S-03	TYPICAL REINFORCEMENT DETAILS	A2	N.T.S.	B
S-04	PILE LAYOUT PLAN	A1	1:100	B
S-05	PILE DETAILS & PILE SCHEDULE	A2	1:20, 1:50	B
S-06	PILE CAP LAYOUT & SCHEDULE	A1	1:100	B
S-07	PILE CAP DETAILS	A2	1:25	B
S-08	GRADE BEAM LAYOUT & GF SLAB-ON-GRADE	A1	1:100	B
S-09	GRADE BEAM DETAILS (LONG SECTIONS)	A1	1:50	B
S-10	COLUMN LAYOUT PLAN	A1	1:100	B
S-11	COLUMN SCHEDULE	A1	N.T.S.	B
S-12	COLUMN DETAILS	A2	1:20	B
S-13	1ST FLOOR BEAM LAYOUT	A1	1:100	B
S-14	TYPICAL FLOOR BEAM LAYOUT (2ND TO 6TH FLOOR)	A1	1:100	B
S-15	ROOF & STAIR ROOF BEAM LAYOUT	A1	1:50	B
S-16	BEAM DETAILS (1 OF 3) - 1ST FLOOR	A1	1:50	B
S-17	BEAM DETAILS (2 OF 3) - TYPICAL	A1	1:50	B
S-18	BEAM DETAILS (3 OF 3) - ROOF & SCHEDULE	A1	1:100	B
S-19	1ST FLOOR SLAB REINFORCEMENT PLAN	A1	1:100	B
S-20	TYPICAL SLAB REINFORCEMENT PLAN	A1	1:100, 1:20	B
S-21	ROOF, STAIR ROOF & PARAPET	A1	1:50, 1:20	B
S-22	STAIR DETAILS	A1	1:50	B
S-23	LIFT CORE & SHEAR WALL DETAILS	A1	1:50	B
S-24	OVERHEAD WATER TANK & UGWR / SEPTIC TANK	A1	1:100	B
S-25	LINTEL & SUNSHADE SCHEDULE, BUILDING SECTION	A1	N.T.S.	B
S-26	BAR BENDING SCHEDULE (SAMPLE: PC3, 2B7, SLAB S	A3	N.T.S.	B

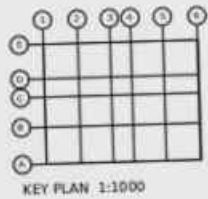

LOCATION MAP (N.T.S.)

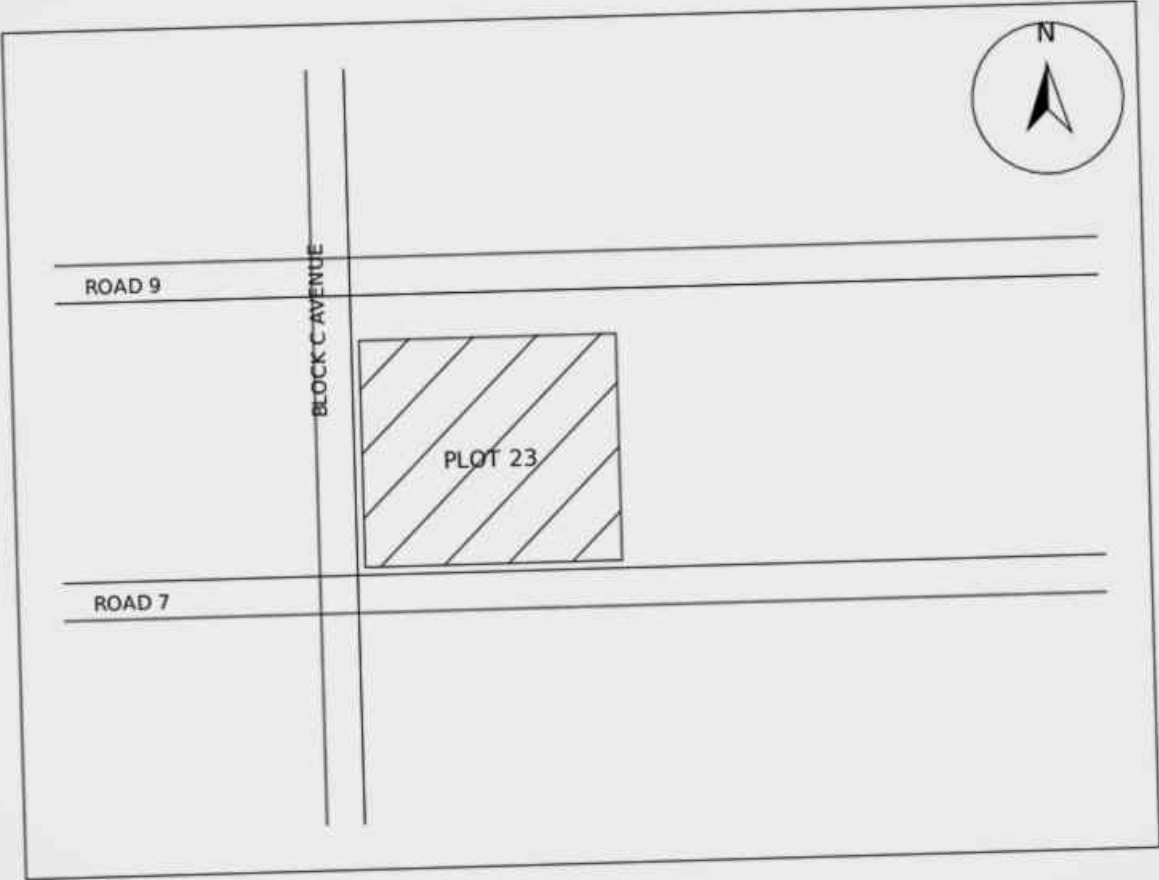

MEGHNA STRUCTURAL CONSULTANT S LTD. HOUSE 12, ROAD 5, BLOCK 8, BANANI, DHAKA-1213 TEL +880 2 5555 0000			
CLIENT M/S. PADMA HOMES LTD.			
PROJECT PROPOSED G+6 STORIED RESIDENTI AL BUILDING			
SITE PLOT 23, ROAD 7, BLOCK C, BASH UNDHARA R/A, DHAKA			
SHEET TITLE COVER, DRAWING INDEX & KEY PLA N			
DESIGNED S.R.	DRAWN M.H.	CHECKED A.K.	APPROVED T.I.
RAJUK REF.		RAJUK/BAP/2026/0417	
JOB NO.		MSC-2026-041	
DATE		12-08-2026	
SCALE		N.T.S.	
SHEET NO. S-00			REV. B
REVISIONS			
REV	DATE	DESCRIPTION	
A	05-07-2026	ISSUED FOR RAJUK APPROVAL	
B	12-08-2026	C4 3RD-6TH BARS REVISED; ISSUED FO	

ALL DIMENSIONS IN mm U.N.O.
DO NOT SCALE THIS DRAWING

GENERAL NOTES

1. THESE DRAWINGS SHALL BE READ WITH THE ARCHITECTURAL AND MEP DRAWINGS. ANY DISCREPANCY SHALL BE REFERRED TO THE ENGINEER BEFORE WORK PROCEEDS.
2. DESIGN CODE: BNBC 2020, ACI 318-19 WHERE THE CODE IS SILENT.
3. IMPOSED LOAD 2.0 kN/m%%2 (RESIDENTIAL), PARTITION 1.5 kN/m%%2, FINISH 1.2 kN/m%%2. BASIC WIND SPEED 65.7 m/s, SEISMIC ZONE 2 (Z=0.20).
4. ALL DIMENSIONS ARE IN MILLIMETRES UNLESS FIGURED IN FEET AND INCHES. LEVELS ARE IN METRES ABOVE P.L.
5. DO NOT SCALE THIS DRAWING - FIGURED DIMENSIONS GOVERN.

CONCRETE AND REINFORCEMENT

6. CONCRETE: CYLINDER STRENGTH AT 28 DAYS AS NOTED BELOW. CEMENT CEM-I 52.5N. MAXIMUM AGGREGATE 20 mm, SLUMP 100 ± 25 mm.
7. REINFORCEMENT: DEFORMED BARS TO BDS ISO 6935-2.
8. BAR LETTERS: T AND Y BOTH MEAN A DEFORMED BAR OF THE DIAMETER THAT FOLLOWS (T16 = Y16 = 16Ø). A SECOND DRAUGHTSMAN'S SHEET MAY MIX THEM ON ONE LINE.
9. LEGACY IMPERIAL BAR CALLS: #3 = 10Ø, #4 = 12Ø, #5 = 16Ø, #6 = 20Ø, #8 = 25Ø.
10. WELDED HOOKS ARE NOT PERMITTED. ALL HOOKS 135° WHERE SHOWN ON S-03.

MATERIALS

f_c = 3500 psi (24 MPa) cylinder

f_c = 3000 psi (BORED PILES)

f_y = 72,500 psi (500 MPa) BDS ISO 6935-2 B500DWR

B500DWR

CLEAR COVER

2" clear cover (pile caps)

25mm clear cover (beams)

40mm clear cover (columns)

20mm clear cover (slabs)

MEASUREMENT CONVENTIONS (AM-02 / AM-03)

COUNTING: [(distance + 0.5 mm)/spacing] + 1

CURVED BALCONY: the R 1524 corner is authored analytically (rect – r² + πr²/4) in both golden paths; the outline polygon keeps the corner point

CUTTING LENGTH: BS 8666 per L-FRM-05 (bend radius 2d ≤16 mm else 3.5d; generic SUMlegs – bends (0.5r + d)); IS-additive printed beside, never billed

HOOKS: 90° = 12d; stirrup/tie 135° = 10d, min 75 mm (S-03)

JUNCTION OWNERSHIP: pile > pile cap > column/shear wall (full floor-to-floor, through joints) > beam (clear between support faces, depth below the slab soffit) > slab (runs through; outline – column/wall plan areas – openings > 0.1 m²)

JUNCTION OWNERSHIP: grade beams clear between cap faces; stair flights sloped length × width × waist + step triangles; landings AREA_THICK

JUNCTION OWNERSHIP: formwork: column 2(b+d) × (floor-to-floor – slab t) – beam-end contacts > 500 cm²; beam sides (D – t each side) + soffit b, × clear; slab soffit net of beam soffits and columns, free edges × t as EDGE; caps/GB/footing sides only; piles none; stair soffit + risers + strings

JUNCTION OWNERSHIP: a junction deduction may defer only where the published figure is then under, never over (AM-02)

LAPS: tension 50d / compression 40d (S-02 general note overrides the BNBC table, J-032); columns and walls one lap per storey

MEMBER END NO DEDUCT CM2: 500

OPENING THRESHOLD M2: 0.1

RAMP: sloped area × thickness (plan × √(run² + rise²))/run)

REBAR UNIT: kg = cutting length (raw, unrounded) × table kg/m

ROUNDED CUTTING LENGTH MM: 25

STOCK MM: 12000

STOCK SPLIT: n = [(L – lap)/(stock – lap)], billable L + (n – 1)·lap; laps are the LAP component

SUNKEN SLAB: drop 300; slab 125 + drop walls 125 × 175 on the cut-out perimeter; formwork soffit + both drop faces

UNIT WEIGHTS: L-FRM-05 table (8->0.395, 10->0.616, 12->0.888, 16->1.579, 20->2.466, 25->3.854 kg/m); d²/162 is a check only

WASTAGE: raw in quantities > 3% and binding wire 8 kg/t belong to resource summaries only (AM-03a)

S-01 GENERAL NOTES (1 OF 2)



MEGHNA STRUCTURAL CONSULTANT
S LTD.
HOUSE 12, ROAD 5, BLOCK B, BAHANI, DHAKA-1213
TEL +880 2 5555 0000

CLIENT
M/S. PADMA HOMES LTD.

PROJECT
PROPOSED G+6 STORIED RESIDENTIAL BUILDING

SITE
PLOT 23, ROAD 7, BLOCK C, BASH
UNDHARA R/A, DHAKA

SHEET TITLE
GENERAL NOTES (1 OF 2)

DESIGNED
S.R.

DRAWN
M.H.

CHECKED
A.K.

APPROVED
T.I.

RAJUK REF. RAJUK/BAP/2026/0417

JOB NO. MSC-2026-041

DATE 12-08-2026

SCALE N.T.S.

SHEET NO.
S-01

REV.
B

REVISIONS

REV	DATE	DESCRIPTION
A	05-07-2026	ISSUED FOR RAJUK APPROVAL
B	12-08-2026	CE 3RD-4TH BARS REVISED; ISSUED FOR

ALL DIMENSIONS IN mm U.N.O.
DO NOT SCALE THIS DRAWING

DO NOT SCALE

DETAILING NOTES

11. LAPS SHALL BE STAGGERED; NOT MORE THAN 50% OF BARS MAY BE LAPPED AT ONE SECTION. NO LAP WITHIN A BEAM-COLUMN JOINT.

12. TOP BARS OVER SUPPORTS SHALL EXTEND L/4 EACH SIDE OF THE SUPPORT FACE, BOTTOM BARS L/5, UNLESS THE LONG SECTION SHOWS OTHERWISE.

13. STIRRUP ZONES: 2D FROM EACH SUPPORT FACE AT THE CLOSE SPACING, THE MIDDLE AT THE WIDE SPACING.

14. CHAIRS AT 1.0 m c/c BOTH WAYS IN EVERY DOUBLE-LAYER SLAB AND RAFT.

LAP 50d TENSION / 40d COMPRESSION U.N.O.

(THIS NOTE GOVERNS OVER THE CODE TABLE)

DEVELOPMENT LENGTH l_d - f_y 500 MPa, f'_c 3500 psi

BAR	l_d BOTTOM (mm)	l_d TOP (mm)	LAP TENSION (mm)	LAP COMPRESSION (mm)
8Ø	400	520	400	320
10Ø	500	650	500	400
12Ø	600	780	600	480
16Ø	800	1040	800	640
20Ø	1000	1300	1000	800
25Ø	1250	1625	1250	1000

BAR BENDING TO BS 8666; THE IS ADDITIVE FIGURE IS PRINTED BESIDE IT ON S-26.

MEGHNA STRUCTURAL CONSULTANT
S LTD.
HOUSE 12, ROAD 5, BLOCK B, BANAH, DHAKA-1213
TEL +880 2 5555 0000

CLIENT
M/S. PADMA HOMES LTD.

PROJECT
PROPOSED G+6 STORIED RESIDENTIAL BUILDING

SITE
PLOT 23, ROAD 7, BLOCK C, BASH
UNDHARA R/A, DHAKA

SHEET TITLE
GENERAL NOTES (2 OF 2) & LAP/D
EVELOPMENT TABLE

DESIGNED
S.R.

DRAWN
M.H.

CHECKED
A.K.

APPROVED
T.I.

RAJUK REF. RAJUK/BAP/2026/0417

JOB NO. MSC-2026-041

DATE 12-08-2026

SCALE N.T.S.

SHEET NO.
S-02

REV.
B

REVISIONS

REV	DATE	DESCRIPTION
A	05-07-2026	ISSUED FOR RAJUK APPROVAL
B	12-08-2026	CA 3RD-FTH BARS REVISED; ISSUED FOR

ALL DIMENSIONS IN mm U.N.O.
DO NOT SCALE THIS DRAWING

DO NOT SCALE

MEGHNA STRUCTURAL CONSULTANTS LTD.

HOUSE 12, ROAD 5, BLOCK 8, BANARI, DHAKA-1213

TEL +880 2 5555 0000

CLIENT

M/S. PADMA HOMES LTD.

PROJECT

PROPOSED G+6 STORIED RESIDENTIAL BUILDING

SITE

PLOT 23, ROAD 7, BLOCK C, BASHUNDHARA R/A, DHAKA

SHEET TITLE

TYPICAL REINFORCEMENT DETAILS

DESIGNED

S.R.

DRAWN

M.H.

CHECKED

A.K.

APPROVED

T.I.

RAJUK REF.

RAJUK/BAP/2026/0417

JOB NO.

MSC-2026-041

DATE

12-08-2026

SCALE

N.T.S.

SHEET NO.

S-03

REV.

B

REVISIONS

REV	DATE	DESCRIPTION
A	05-07-2026	ISSUED FOR RAJUK APPROVAL
B	12-08-2026	CA 3RD-FTH BARS REVISED; ISSUED FOR

ALL DIMENSIONS IN mm U.N.O.

DO NOT SCALE THIS DRAWING

BS 8666 SHAPE CODES USED IN THE BAF

- SHAPE 21


A + B + C
- SHAPE 51

2(A+B) + 2C - 2.5r - 5d
- SHAPE 11


A + (B) hook
- SHAPE 00

A straight


BAR SHAPE CODES SCALE 1:25

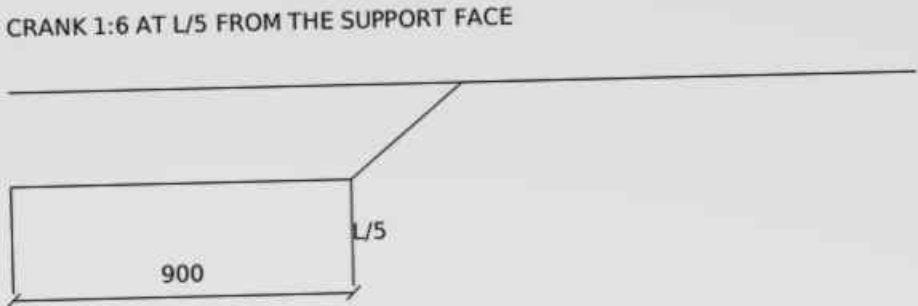

TYPICAL SLAB BAR CRANK SCALE 1:20

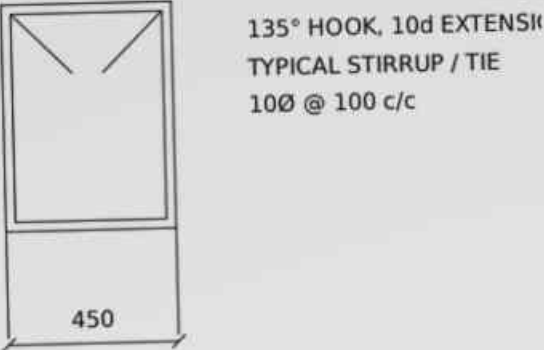

TYPICAL STIRRUP HOOK DETAIL SCALE 1:20

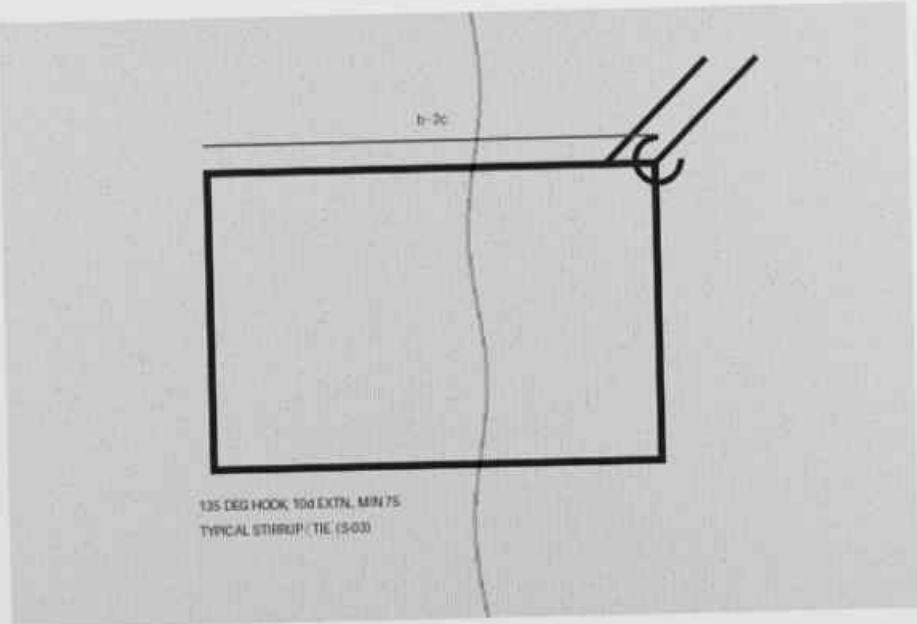

PASTED DETAIL - HOOK (SCANNED FROM THE STANDARD SHEET)

HOOK 135° = 10d, MIN 75 mm; 90° = 12d





MEGHNA STRUCTURAL CONSULTANT
S LTD.
HOUSE 12, ROAD 3, BLOCK R, BANANI, DHAKA-1213
TEL: +880 2 5533 8800


CLIENT
M.S. PADMA HOMES LTD.

PROJECT
PROPOSED G+6 STORIED RESIDENTIAL BUILDING

SITE
PLOT 23, ROAD 7, BLOCK C, BASH
UNDHARA RAJA, DHAKA

SHEET TITLE
PILE LAYOUT PLAN

DESIGNED	DRAWN	CHECKED	APPROVED
S.R.	M.H.	A.K.	T.I.
RAJUK REF. RAJUK/BAP/2026/0417			
JOB NO. MSC-2026-041			
DATE 12-08-2026			
SCALE 1:100			
SHEET NO. S-04			REV. B
REVISIONS			
REV	DATE	DESCRIPTION	
A	12-08-2026	DESIGNED FOR RAJUK APPROVAL	
B	12-08-2026	CS 3RD-4TH FLOOR SERVICES, REVISION 1.0	

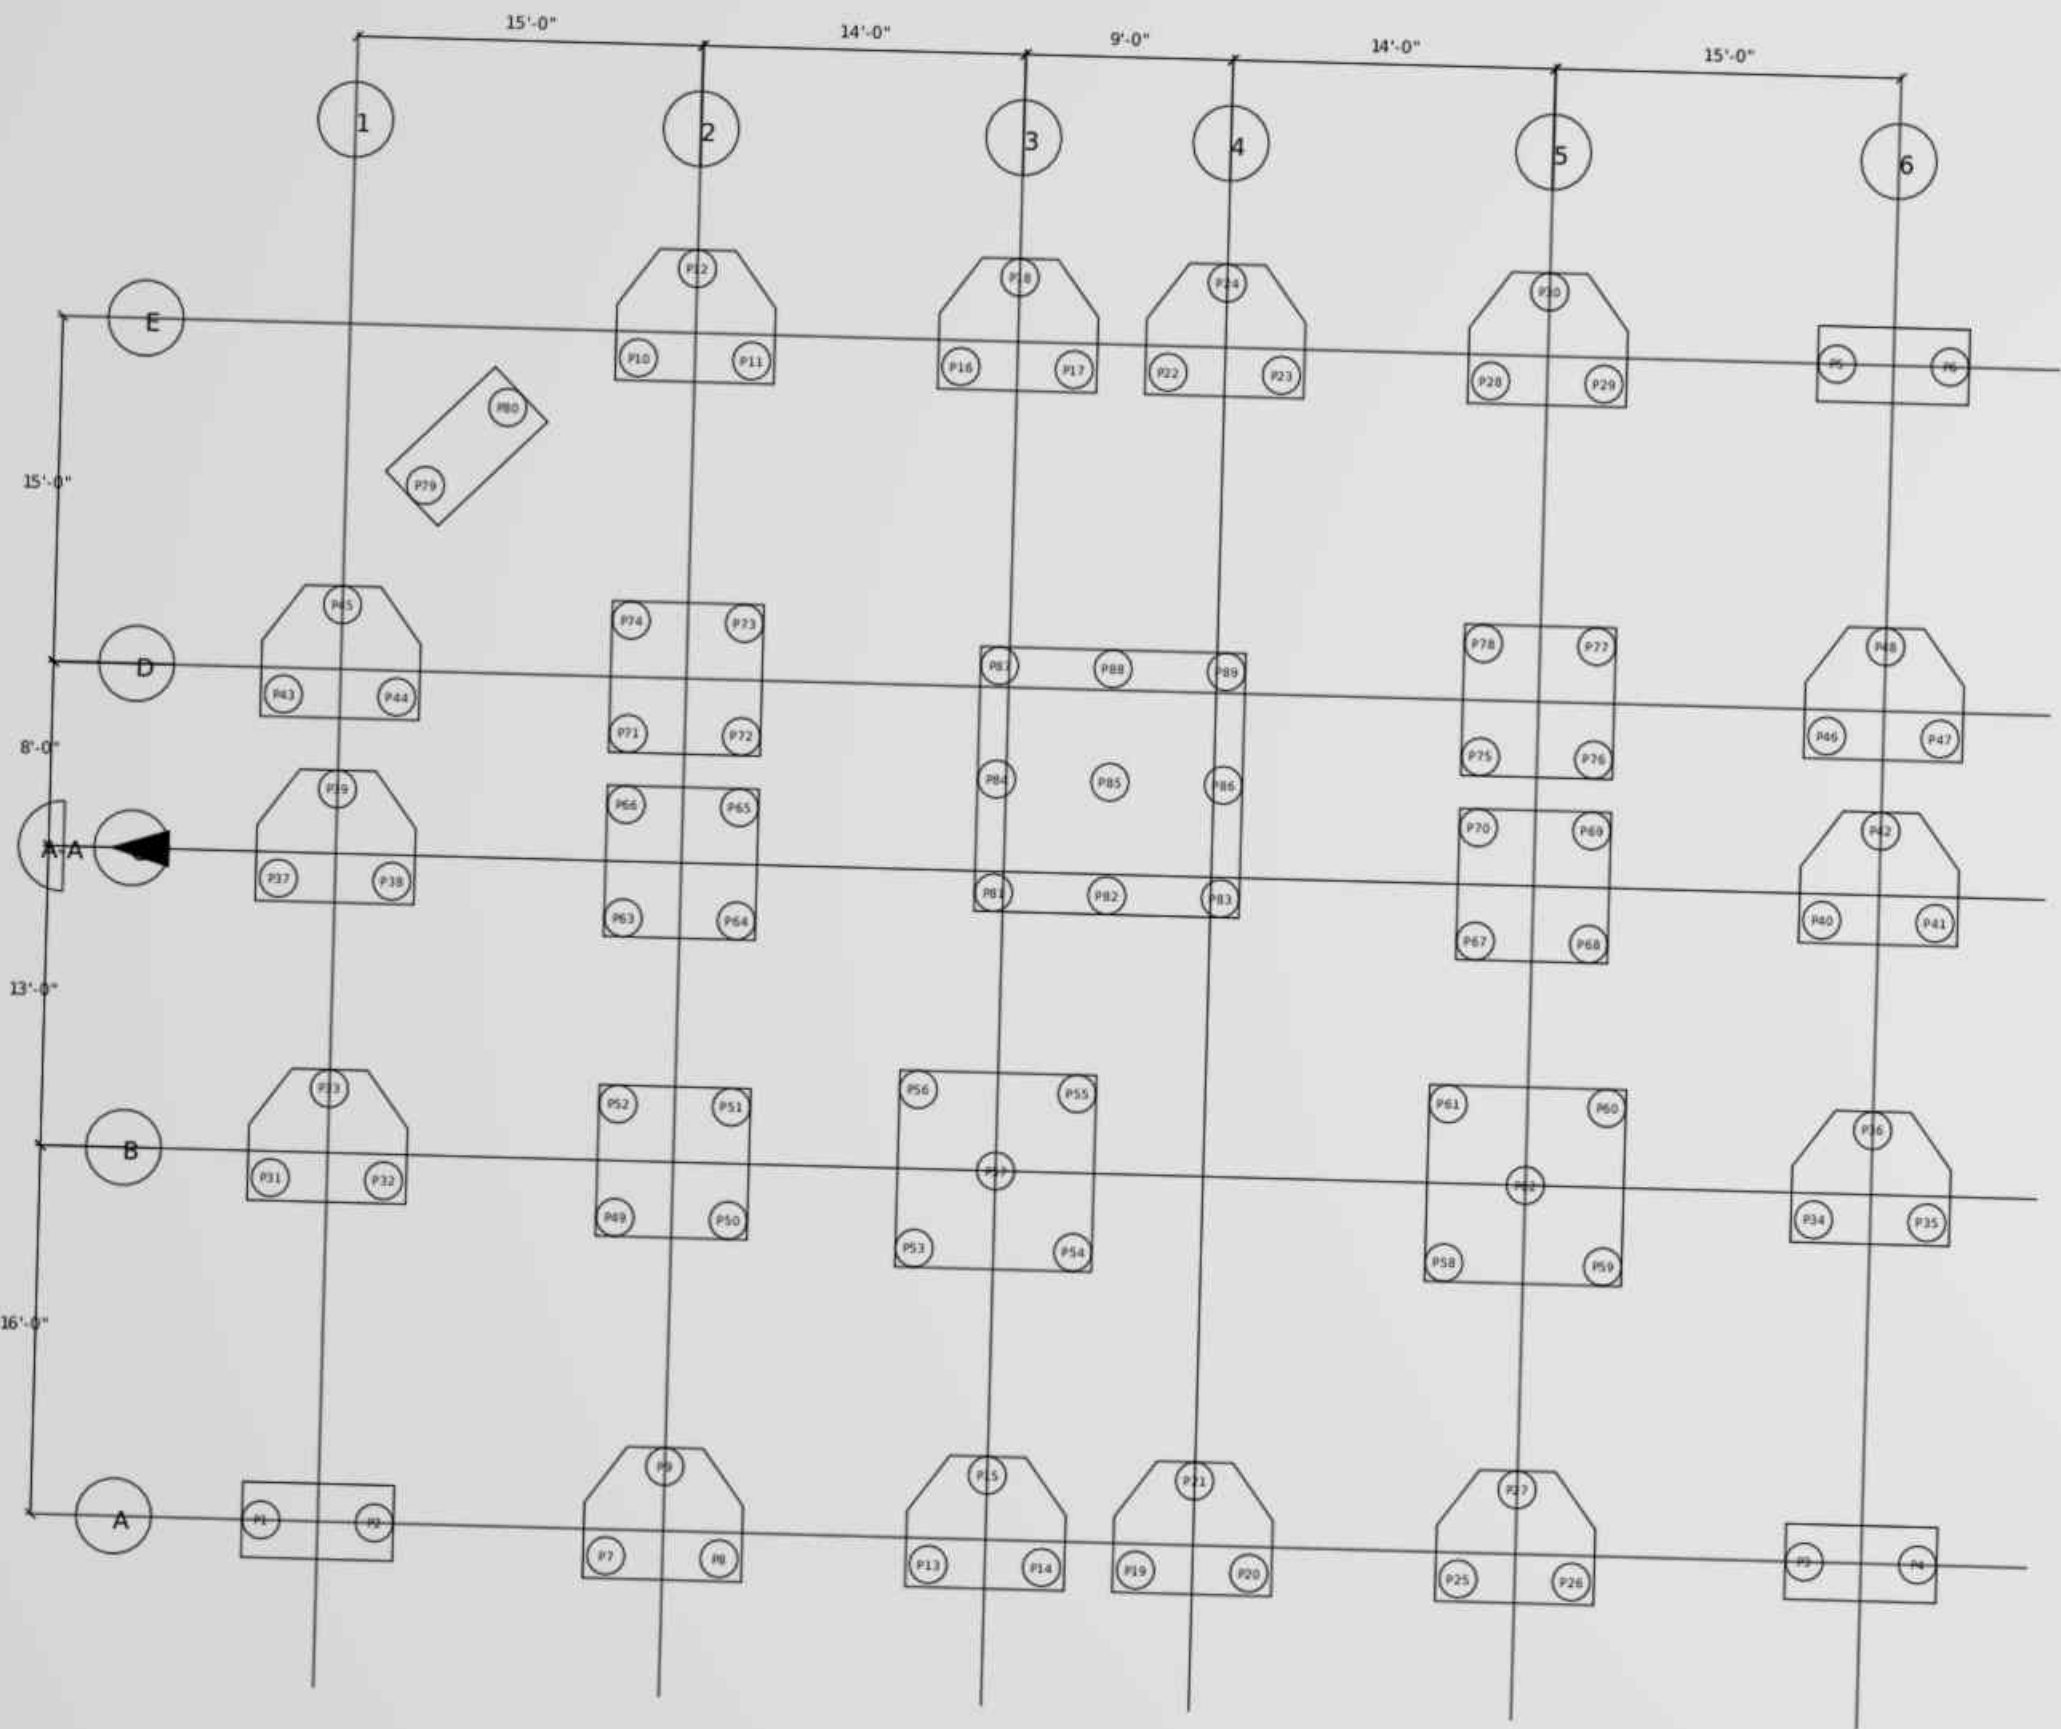



89 NOS. Ø500 BORED PILES, TOE AT EL -23.165


PILE SET-OUT TABLE - COORDINATES FROM GRID 1 / GRID A

PILE	X (mm)	Y (mm)	PILE	X (mm)	Y (mm)	PILE	X (mm)	Y (mm)
P1	-750	0	P31	-750	4527	P61	14800	5927
P2	750	0	P32	750	4527	P62	15850	4877
P3	19672	0	P33	0	5727	P63	3822	8089
P4	21172	0	P34	19672	4527	P64	5322	8089
P5	19672	15850	P35	21172	4527	P65	5322	9589
P6	21172	15850	P36	20422	5727	P66	3822	9589
P7	3822	-350	P37	-750	8489	P67	15100	8089
P8	5322	-350	P38	750	8489	P68	16600	8089
P9	4572	850	P39	0	9689	P69	16600	9589
P10	3822	15500	P40	19672	8489	P70	15100	9589
P11	5322	15500	P41	21172	8489	P71	3822	10528
P12	4572	16700	P42	20422	9689	P72	5322	10528
P13	8089	-350	P43	-750	10928	P73	5322	12028
P14	9589	-350	P44	750	10928	P74	3822	12028
P15	8839	850	P45	0	12128	P75	15100	10528
P16	8089	15500	P46	19672	10928	P76	16600	10528
P17	9589	15500	P47	21172	10928	P77	16600	12028
P18	8839	16700	P48	20422	12128	P78	15100	12028
P19	10832	-350	P49	3822	4127	P79	1053	11736
P20	12332	-350	P50	5322	4127	P80	2114	14796
P21	11582	850	P51	5322	5627	P81	8711	8558
P22	10832	15500	P52	3822	5627	P82	10211	8558
P23	12332	15500	P53	7789	3827	P83	11711	8558
P24	11582	16700	P54	9889	3827	P84	8711	10058
P25	15100	-350	P55	9889	5927	P85	10211	10058
P26	16600	-350	P56	7789	5927	P86	11711	10058
P27	15850	850	P57	8839	4877	P87	8711	11558
P28	15100	15500	P58	14800	3827	P88	10211	11558
P29	16600	15500	P59	16900	3827	P89	11711	11558
P30	15850	16700	P60	16900	5927			

PILE SET-OUT TABLE SCALE 1:100

PILE LAYOUT PLAN SCALE 1:100

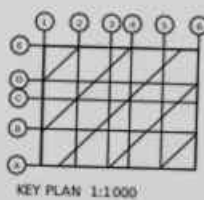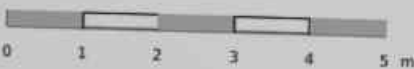

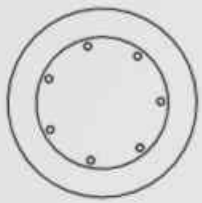

4-200 FULL LEN-
3-200 CURTAILE




PILE SECTION SCALE 1:20


BORED CAST-IN-SITU PILES, f'c = 3000 psi

MARK	DIA (mm)	LENGTH (mm)	MAIN BARS	SPIRAL	NOS
P	500	21336	4-20Ø + 3-20Ø	10Ø @ 75/150	89

PILE SCHEDULE SCALE 1:50

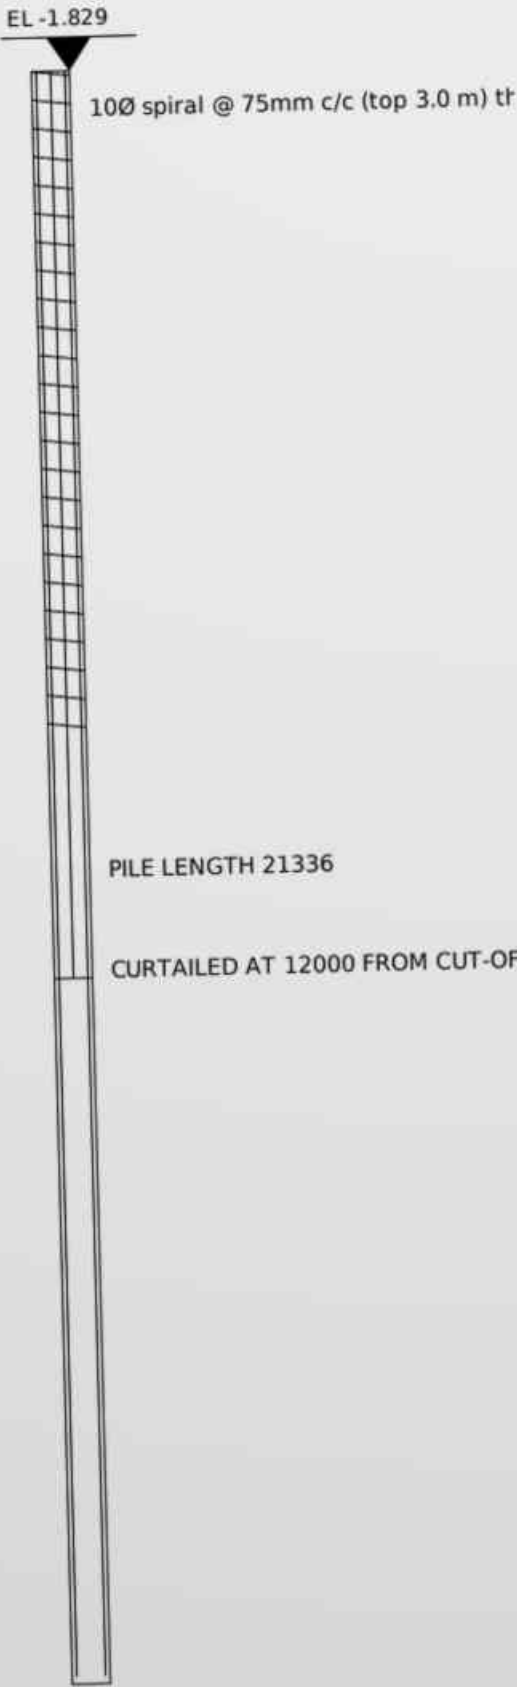

PILE CURTAILMENT & SPIRAL ZONES SCALE 1:100

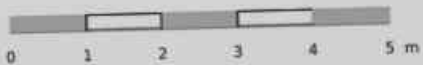

MEGHNA STRUCTURAL CONSULTANT S LTD. HOUSE 12, ROAD 5, BLOCK B, BANARI, DHAKA-1213 TEL +880 2 5555 0000			
CLIENT M/S. PADMA HOMES LTD.			
PROJECT PROPOSED G+6 STORIED RESIDENTIAL BUILDING			
SITE PLOT 23, ROAD 7, BLOCK C, BASH UNDHARA R/A, DHAKA			
SHEET TITLE PILE DETAILS & PILE SCHEDULE			
DESIGNED S.R.	DRAWN M.H.	CHECKED A.K.	APPROVED T.I.
RAJUK REF.		RAJUK/BAP/2026/0417	
JOB NO.		MSC-2026-041	
DATE		12-08-2026	
SCALE		1:20, 1:50	
SHEET NO. S-05			REV. B
REVISIONS			
REV	DATE	DESCRIPTION	
A	05-07-2026	ISSUED FOR RAJUK APPROVAL	
B	12-08-2026	CA 3RD-4TH BARS REVISED; ISSUED FOR	

ALL DIMENSIONS IN mm U.N.O.
DO NOT SCALE THIS DRAWING



MEGHNA STRUCTURAL CONSULTANT
S.LTD.
HOUSE 12, ROAD 3, BLOCK B, BANANI, DHAKA-1213
TEL +880 2 5555 0000

CLIENT
M/S. PADMA HOMES LTD.


PROJECT
PROPOSED G+6 STORIED RESIDENTIAL BUILDING

SITE
PLOT 23, ROAD 7, BLOCK C, BASH
URDHOGRA RA, DHAKA


SHEET TITLE
PILE CAP LAYOUT & SCHEDULE

DESIGNED	DRAWN	CHECKED	APPROVED
S.R.	M.H.	A.K.	T.I.
RAJUK REF.	RAJUK/BAP/2026/0417		
JOB NO.	MSC-2026-041		
DATE	12-08-2026		
SCALE	1:100		
SHEET NO.	S-06		REV. B
REVISIONS			
REV	DATE	DESCRIPTION	
A	05-07-2026	ISSUED FOR RAJUK APPROVAL	
B	12-08-2026	CS 3RD-4TH FAS REVISED, ISSUED PD	

ALL DIMENSIONS IN mm U.N.O.
DO NOT SCALE THIS DRAWING

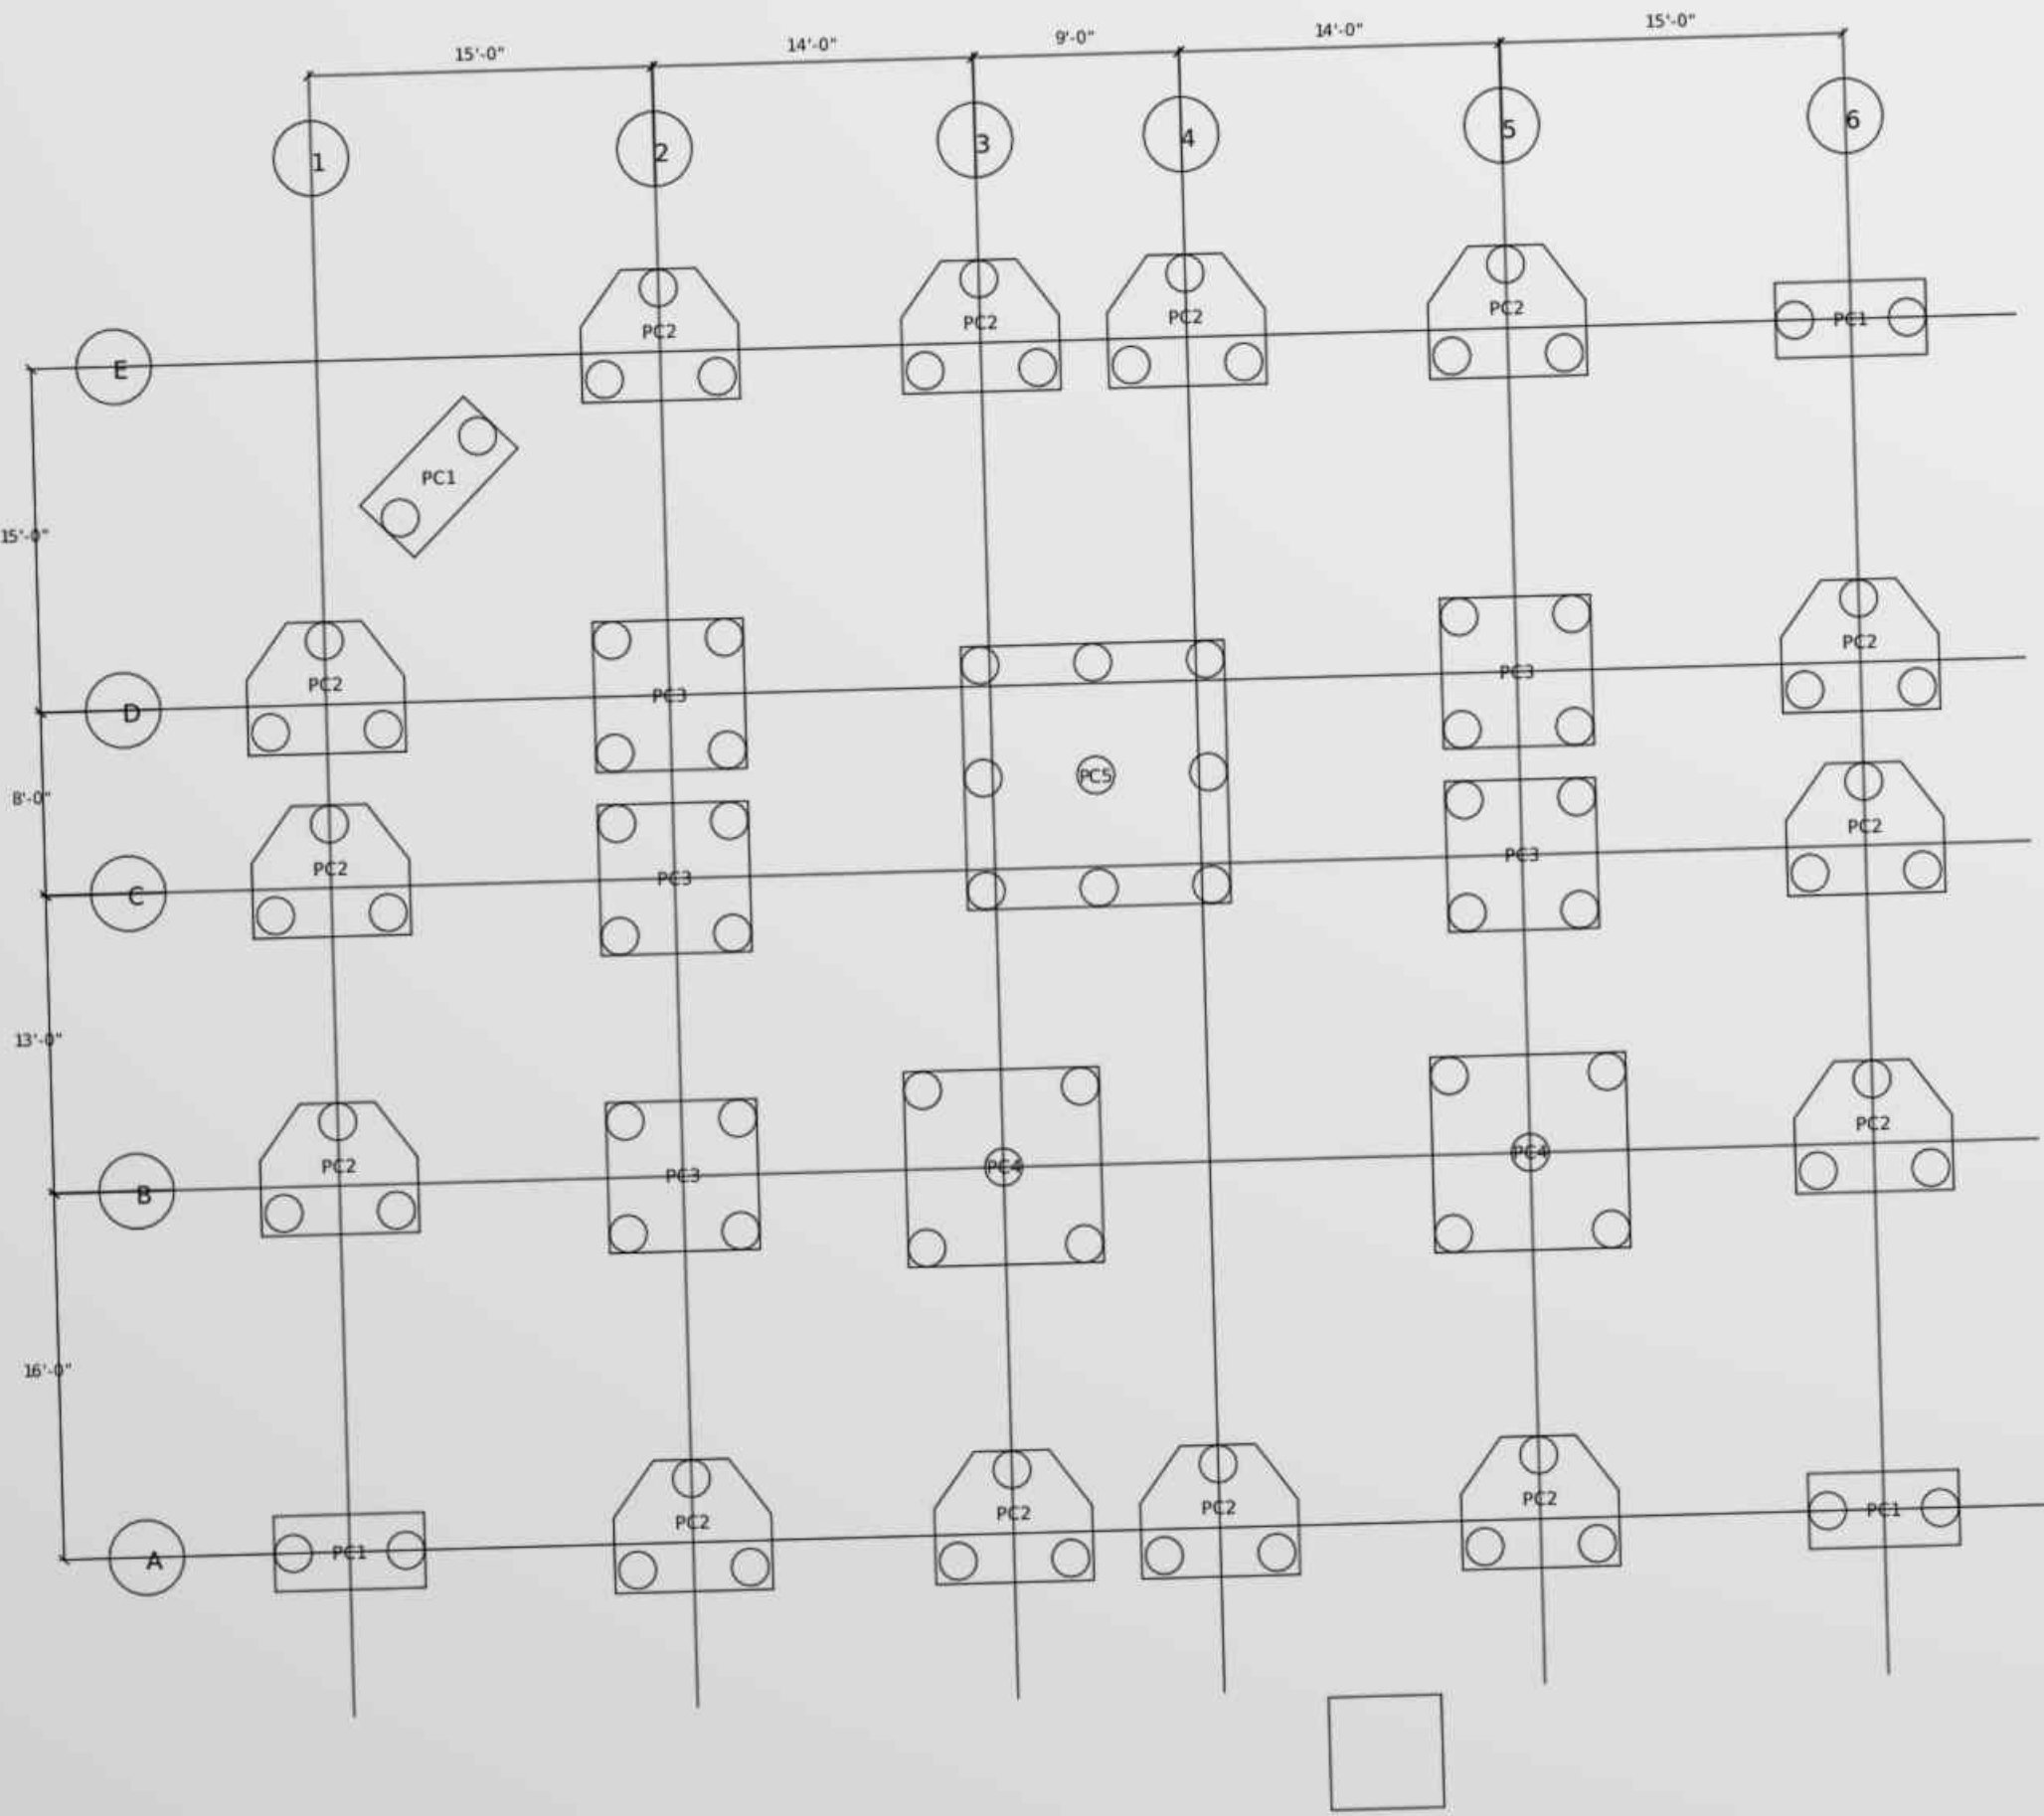

PILE CAP LAYOUT SCALE 1:100

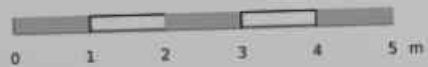


PILE CAP SCHEDULE

MARK SIZE DEPTH PILES BOTTOM MESH TOP MESH
PC1 2000x1000 1295

PC2	2100x1750	1295	2	16Ø @ 150 B/W	12Ø €
PC3	2000x2000	1295	3	16Ø @ 150 B/W	12Ø €
PC4	2600x2600	1295	4	16Ø @ 125 B/W	12Ø €
PC5	3500x3500	1295	5	20Ø @ 125 B/W	12Ø €
			9	20Ø @ 125 B/W	16Ø €

COUNTS ARE TAKEN FROM THE LAYOUT ABOVE
THIS OFFICE PRINTS NO NOS COLUMN

PILE CAP SCHEDULE SCALE 1:50

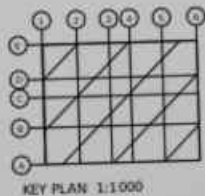

KEY PLAN 1:1000

MEGHNA STRUCTURAL CONSULTANT
S LTD.
HOUSE 12, ROAD 5, BLOCK B, BANANI, DHAKA-1213
TEL +880 2 5555 0000

CLIENT
M/S. PADMA HOMES LTD.

PROJECT
PROPOSED G+6 STORIED RESIDENTIAL BUILDING

SITE
PLOT 23, ROAD 7, BLOCK C, BASH
UNDHARA R/A, DHAKA

SHEET TITLE
PILE CAP DETAILS

DESIGNED S.R.	DRAWN M.H.	CHECKED A.K.	APPROVED T.I.
------------------	---------------	-----------------	------------------

RAJUK REF.
RAJUK/BAP/2026/0417

JOB NO.
MSC-2026-041

DATE
12-08-2026

SCALE
1:25


SHEET NO.
S-07

REV.
B

REVISIONS		
REV	DATE	DESCRIPTION
A	05-07-2026	ISSUED FOR RAJUK APPROVAL
B	12-08-2026	ON 3RD-4TH BARS REVISED; ISSUED FOR

ALL DIMENSIONS IN mm U.N.O.
DO NOT SCALE THIS DRAWING


PC1

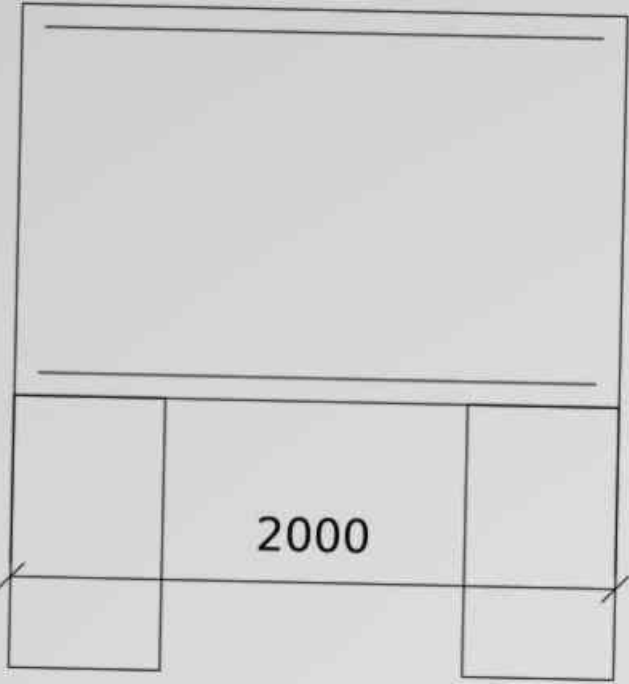

16Ø @ 150 B.W.


PC1 SECTION SCALE 1:25

PC2

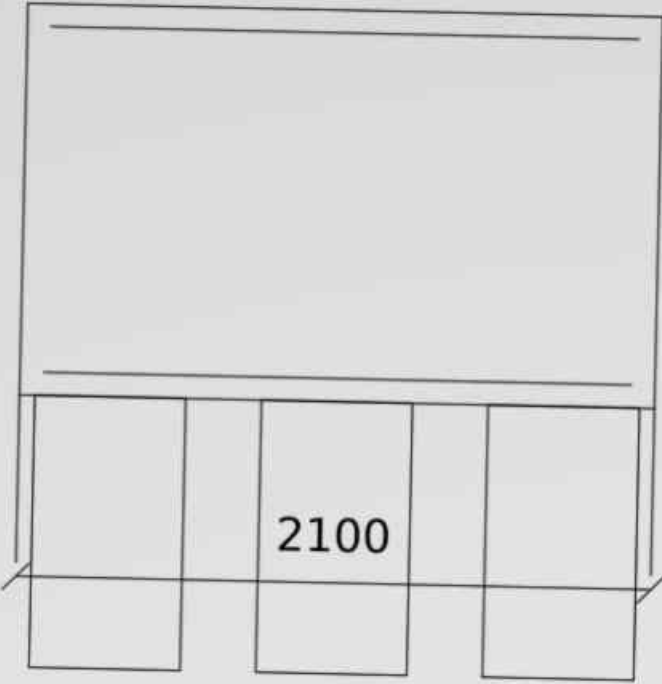


16Ø @ 150 B.W.

PC2 SECTION SCALE 1:25

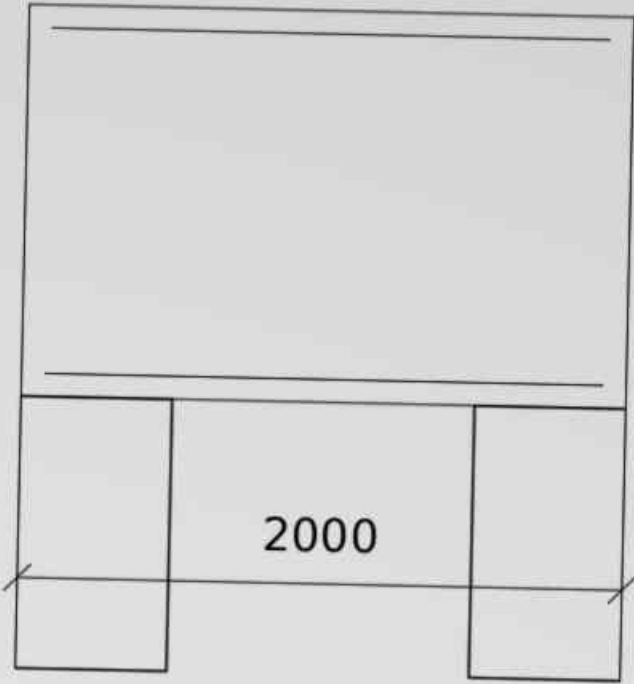


#5 @ 6" c/c B.W.

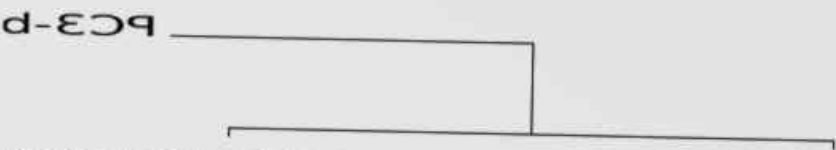


PC3 SECTION SCALE 1:25

PC4

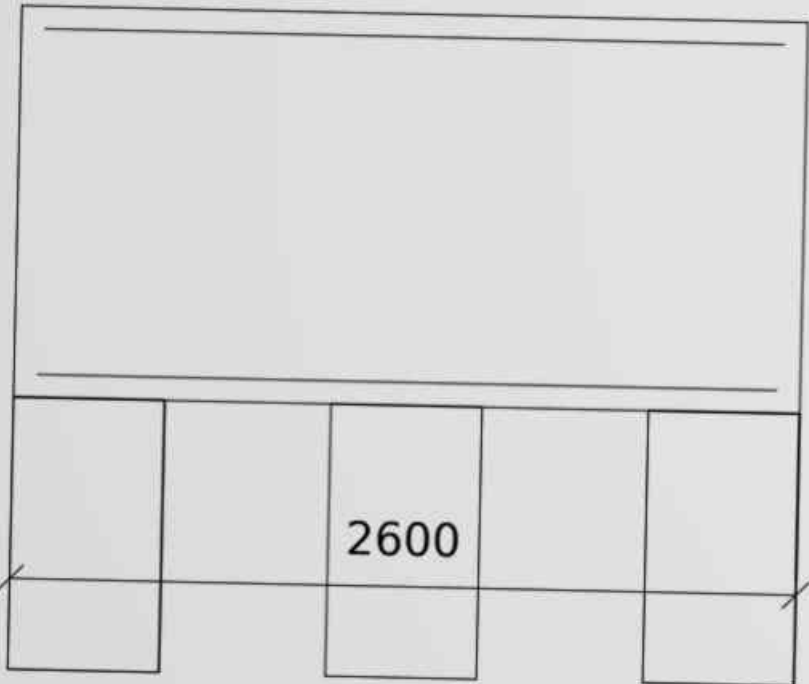


20Ø @ 125 B.W.

PC4 SECTION SCALE 1:25

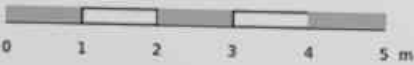


PC5

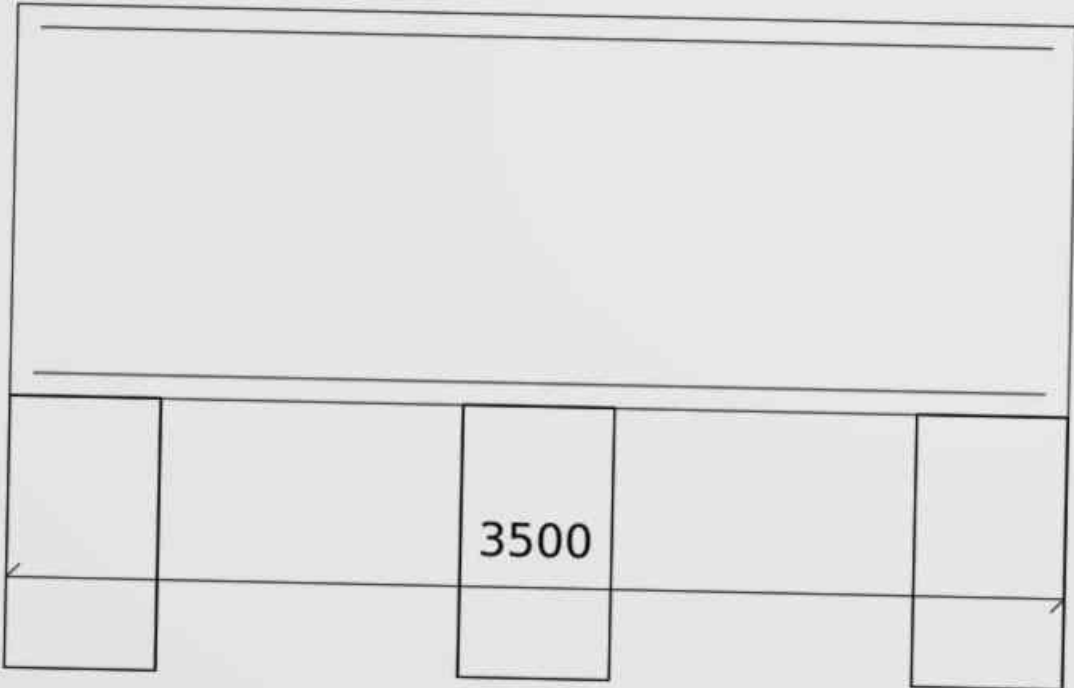

20Ø @ 125 B.W.

PC5 SECTION SCALE 1:25

F1

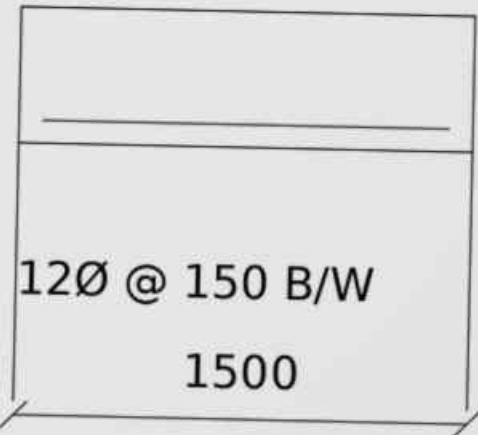

F1 ISOLATED FOOTING (RAMP WALL) SCALE 1:25



MEGHNA STRUCTURAL CONSULTANTS LTD.
HOUSE 12, ROAD 5, BLOCK B, BANANI, DHAKA-1213
TEL: +880 2 5555 0000

CIENT
MS. PADMA HOMES LTD.

PROJECT
PROPOSED G+6 STORIED RESIDENTIAL BUILDING


SITE
PLOT 23, ROAD 7, BLOCK C, BASHUNDHARA RA, DHAKA

SHEET TITLE
GRADE BEAM LAYOUT & GF SLAB-ON-GRADE


DESIGNED	DRAWN	CHECKED	APPROVED
S.R.	M.H.	A.K.	T.I.
RAJUK REF.		RAJUK/RAP/2026/0417	
JOB NO.		MSC-2026-041	
DATE		12-08-2026	
SCALE		1:100	
SHEET NO.		REV.	
S-08		B	


REV.	DATE	DESCRIPTION
A	05-07-2026	ISSUED FOR RAJUK APPROVAL
B	12-08-2026	GA 3RD-FTH BARE REVISED, ISSUED FOR

ALL DIMENSIONS IN mm U.S.D.
DO NOT SCALE THIS DRAWING

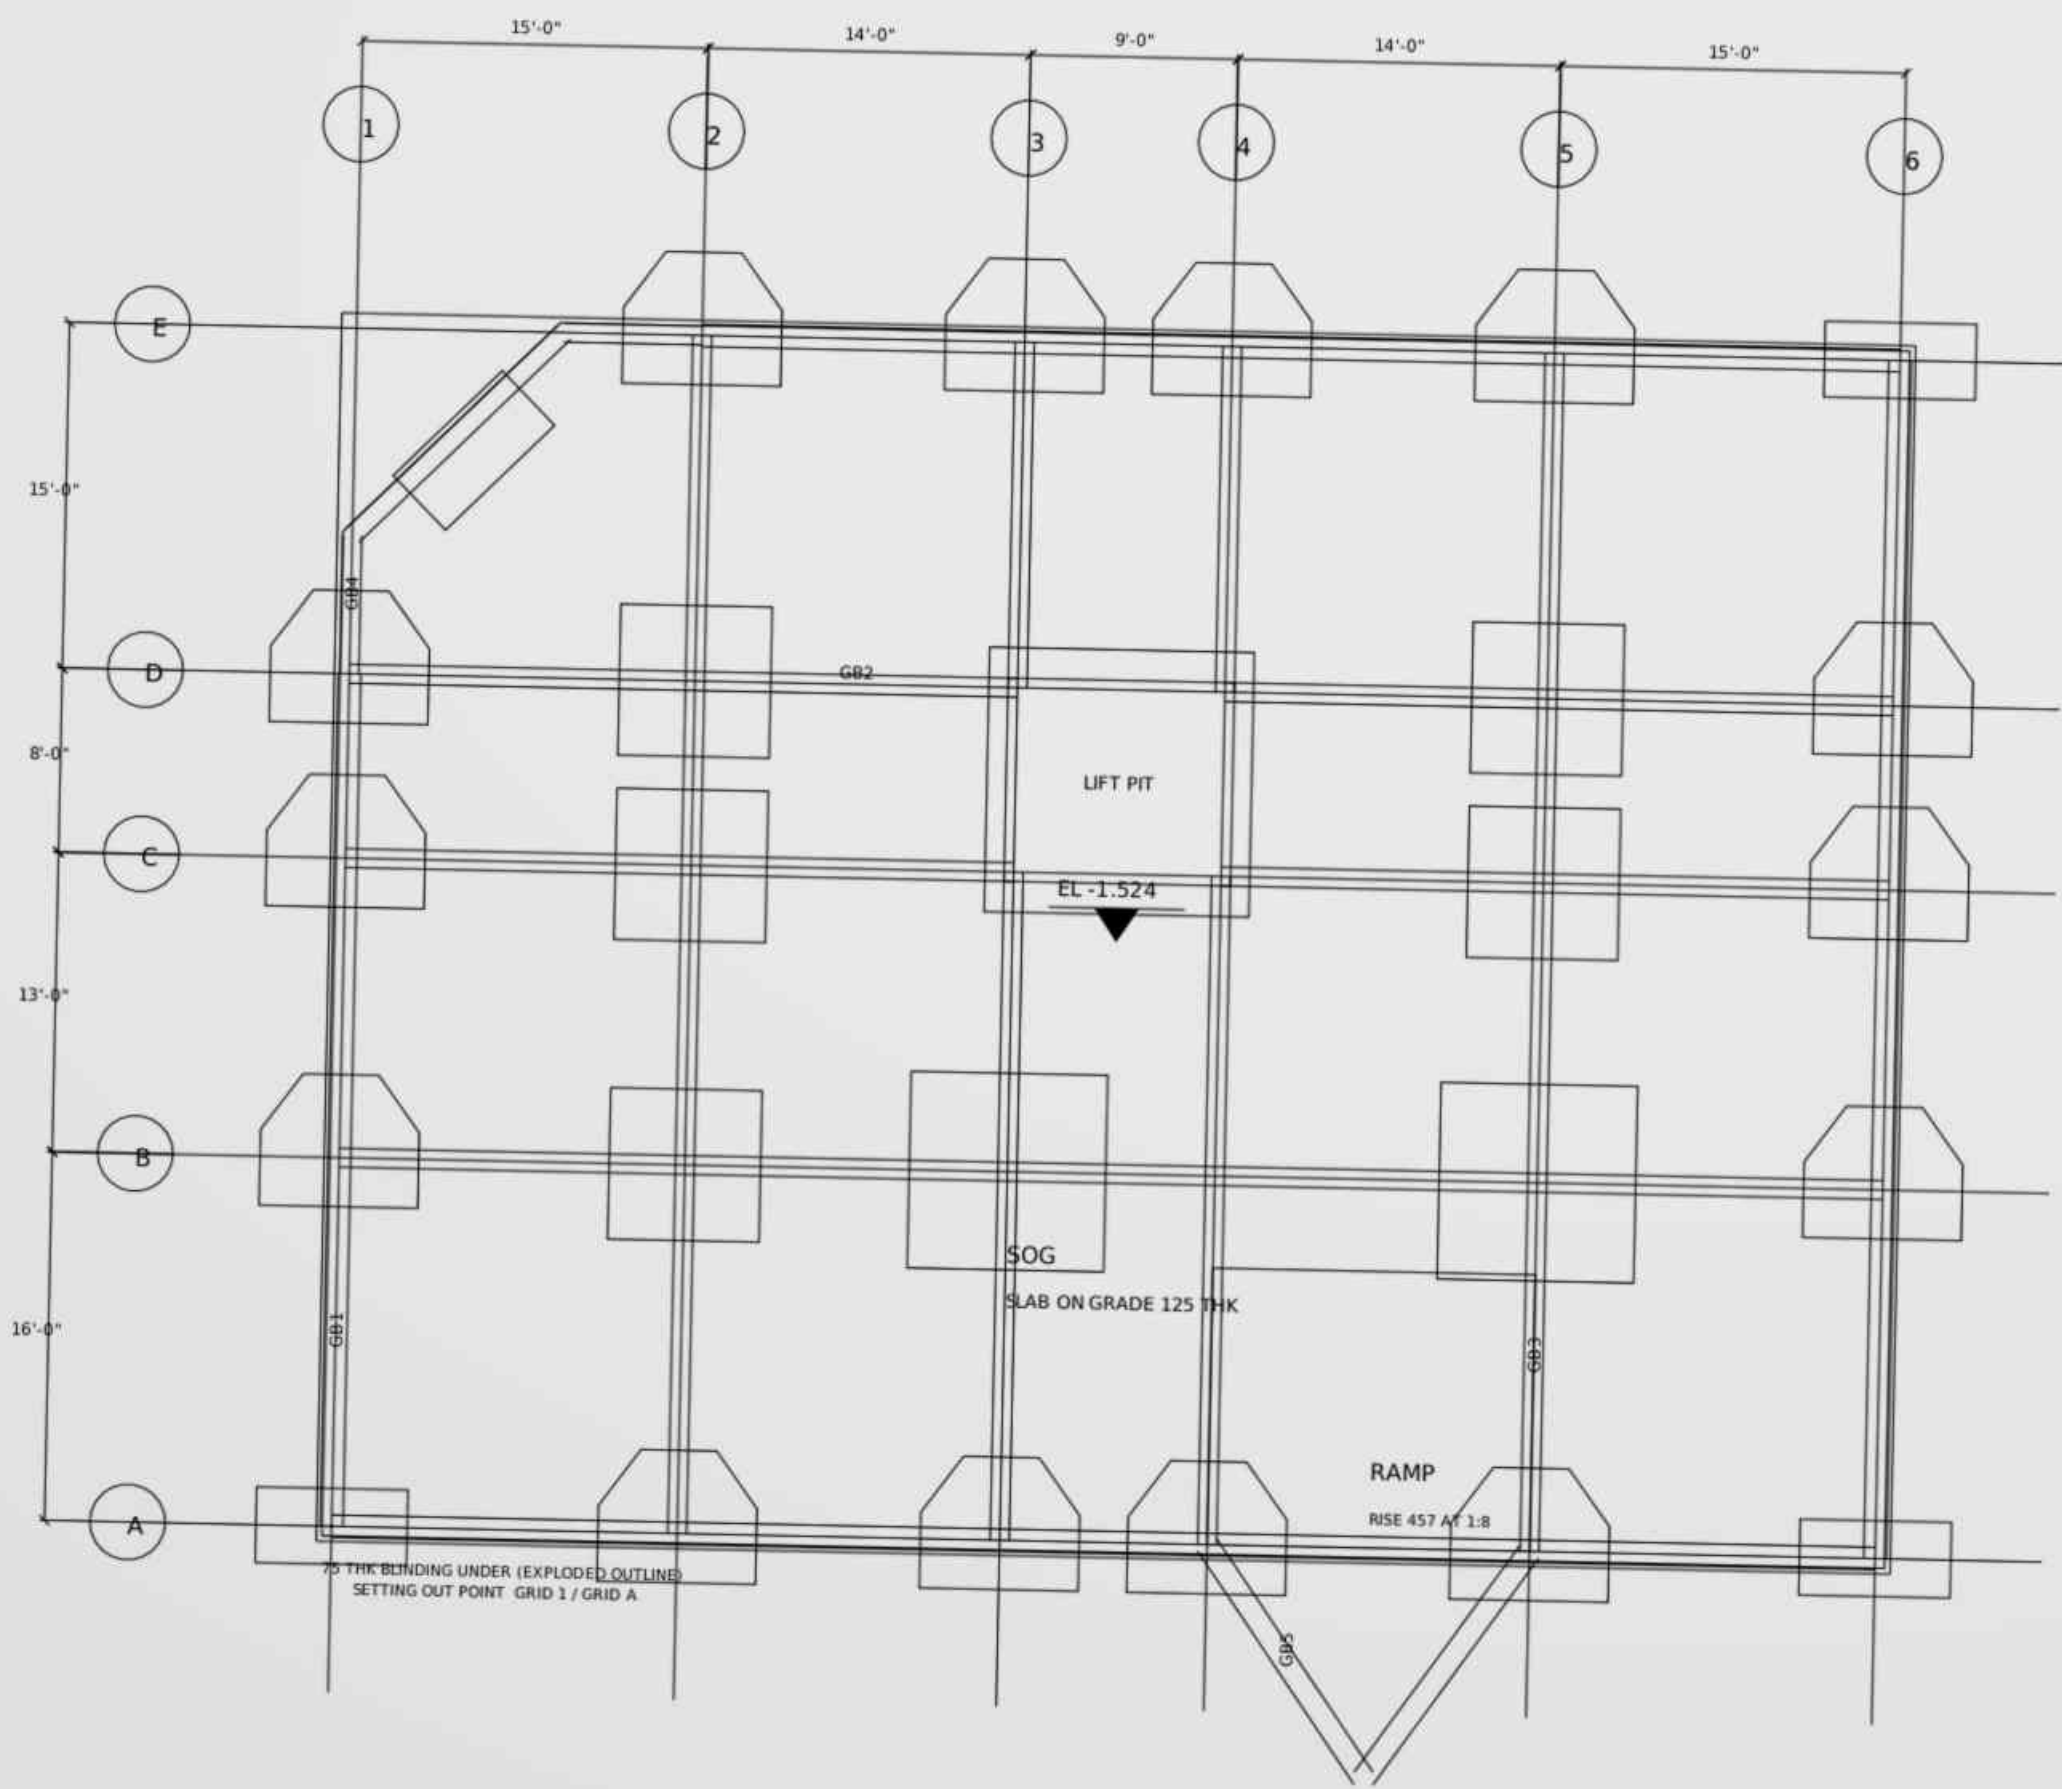


GRADE BEAM LAYOUT & GF SLAB ON GRADE SCALE 1:100

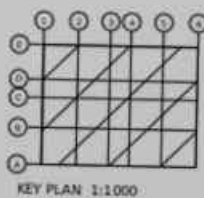


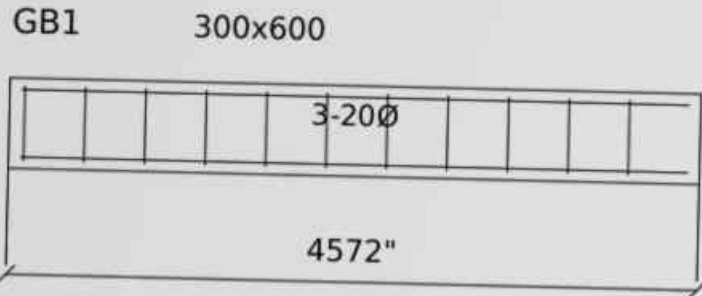


GB1 LONG SECTION SCALE 1:50

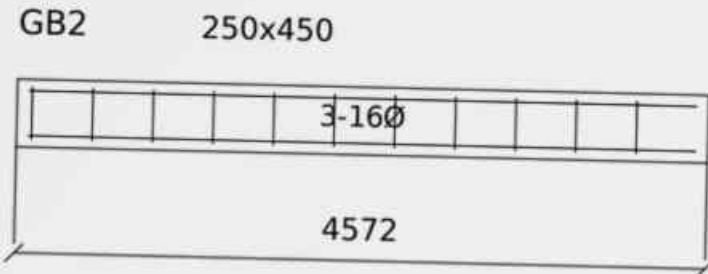


GB2 LONG SECTION SCALE 1:50

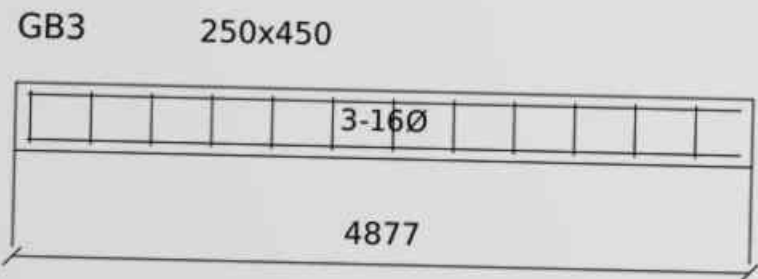


GB3 LONG SECTION SCALE 1:50

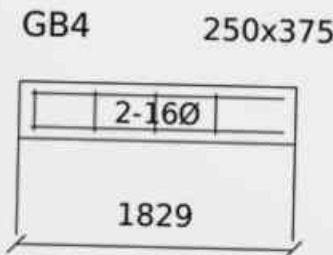

GB4 LONG SECTION SCALE 1:50

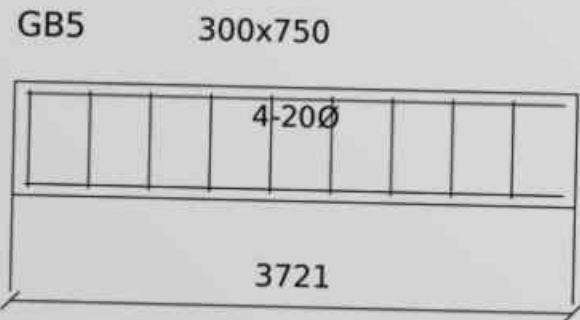

GB5 LONG SECTION SCALE 1:50

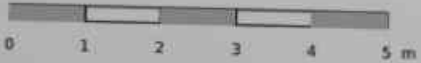

MEGHNA STRUCTURAL CONSULTANT

S LTD.

HOUSE 12, ROAD 5, BLOCK B, BANANI, DHAKA-1213

TEL: +880 2 5555 8880

CLIENT

M/S. PADMA HOMES LTD.

PROJECT

PROPOSED G+6 STORIED RESIDENTIAL BUILDING

SITE

PLOT 23, ROAD 7, BLOCK C, BASHUNDHARA RA, DHAKA

SHEET TITLE

GRADE BEAM DETAILS (LONG SECTIONS)

DESIGNED

DRAWN

CHECKED

APPROVED

S.R.

M.H.

A.K.

T.I.

RAJUK REF.

RAJUK/BAP/2026/0417

JOB NO.

MSC-2026-041

DATE

12-08-2026

SCALE

1:50

SHEET NO.

S-09

REV.

B

REVISIONS


REV	DATE	DESCRIPTION
A	05-07-2026	ISSUED FOR RAJUK APPROVAL
B	12-08-2026	1st 3RD-4TH RANKS REVISED. ISSUED FOR

ALL DIMENSIONS IN MM U.S.D.

DO NOT SCALE THIS DRAWING




MEGHNA STRUCTURAL CONSULTANT S. LTD. HOUSE 12, ROAD 1, BLOCK B, BANANI, DHAKA-1213 TEL: +880 2 5555 0000			
CLIENT M/S. PADMA HOMES LTD.			
PROJECT PROPOSED G+6 STORIED RESIDENTIAL BUILDING			
SITE PLOT 23, ROAD 7, BLOCK C, BASHUNDHARA RA, DHAKA			
SHEET TITLE COLUMN LAYOUT PLAN			
DESIGNED S.R.	DRAWN M.H.	CHECKED A.K.	APPROVED T.I.
RAJUK REF. RAJUK/BAP/2026/0417			
JOB NO. MSC-2026-041			
DATE 12-08-2026			
SCALE 1:100			
SHEET NO. S-10		REV. B	
REVISIONS			
REV.	DATE	DESCRIPTION	
A	05-07-2026	ISSUED FOR RAJUK APPROVAL	
B	12-08-2026	ON 3RD-FTH BARS REVISED, ISSUED FOR	






















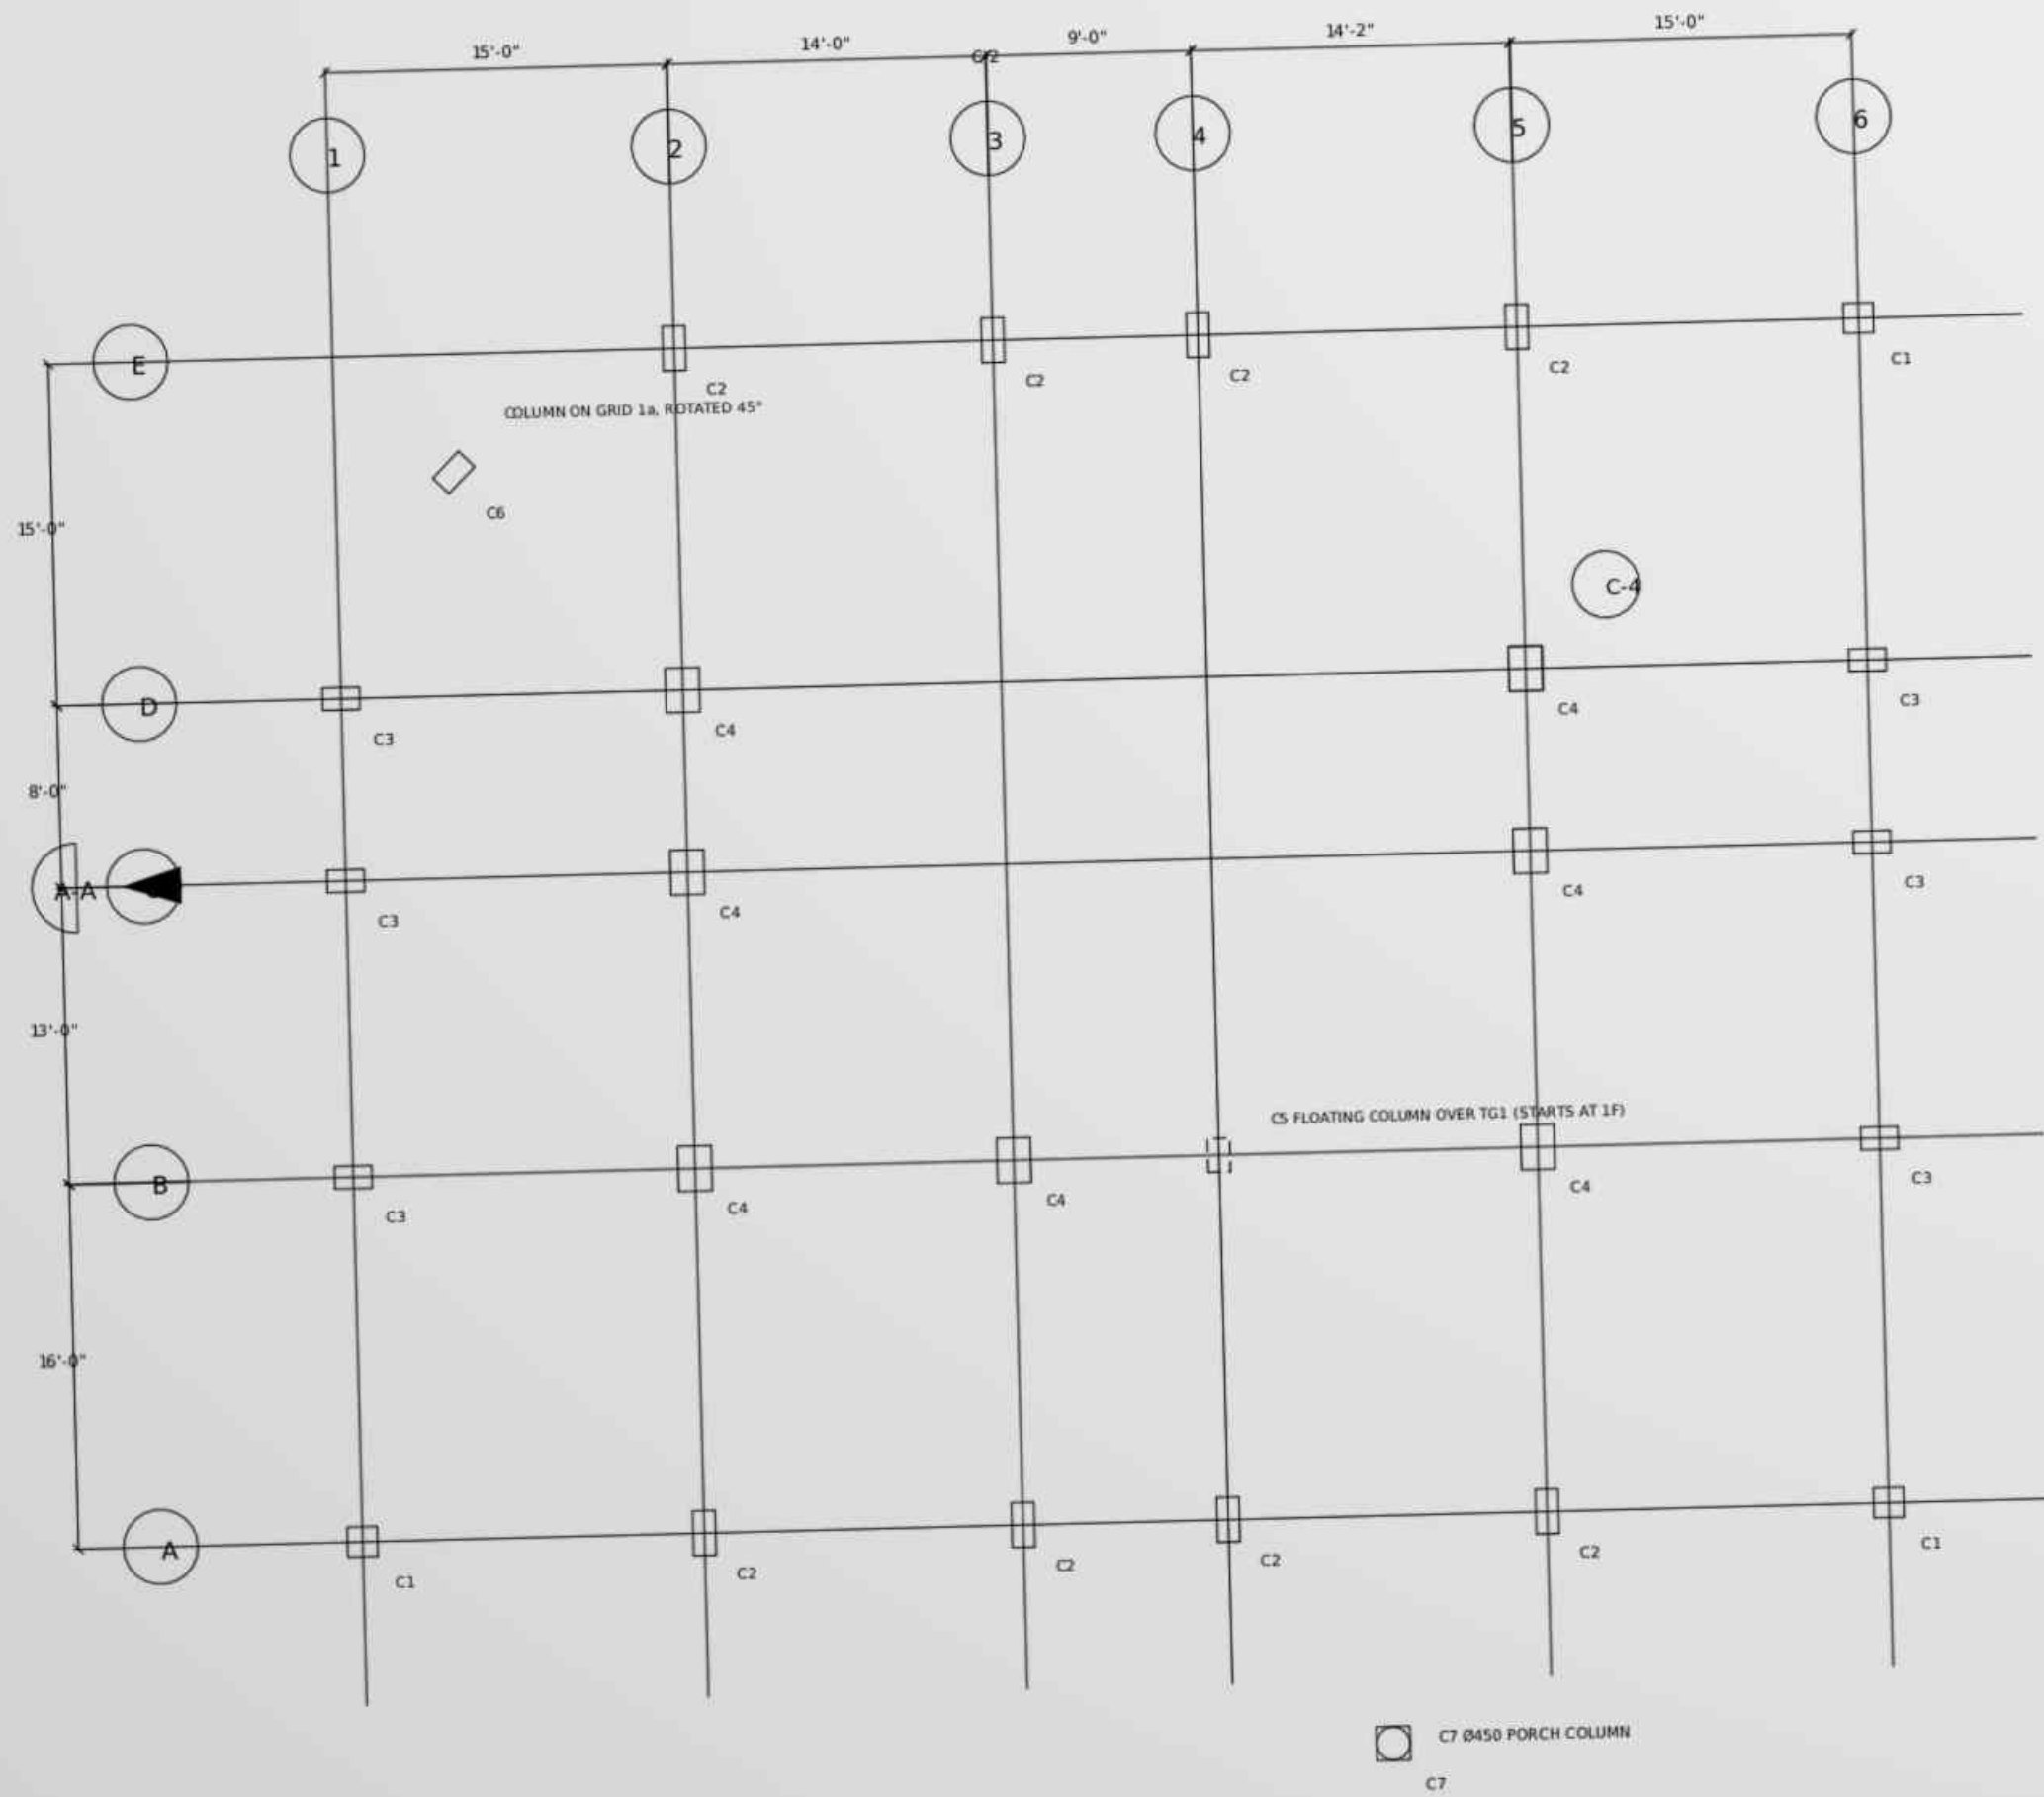


COLUMN POSITIONS ARE FACE-FLUSH ON THE OUTER FACE; SEE THE SCHEDULE ON S-11

COLUMN LAYOUT PLAN SCALE 1:100

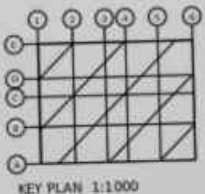

COLUMN SCHEDULE

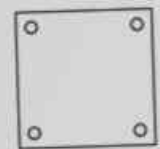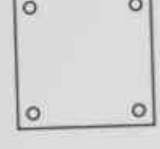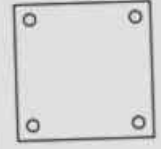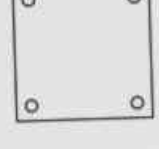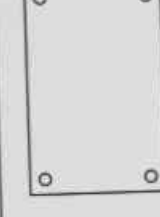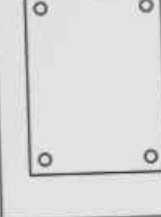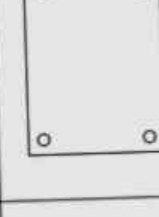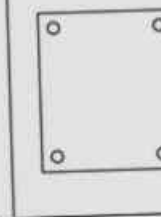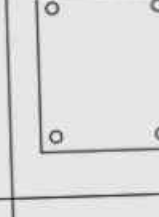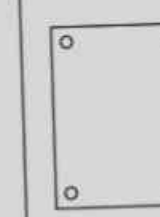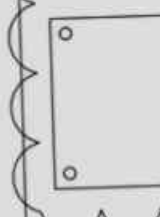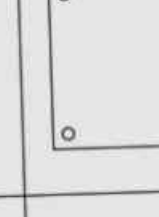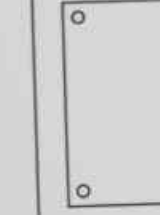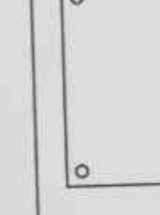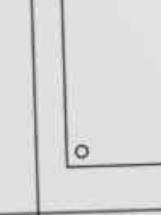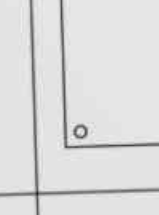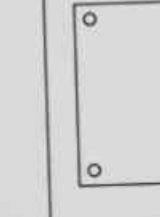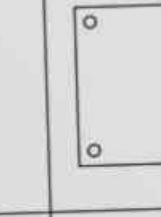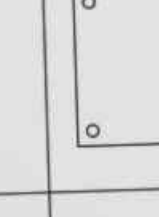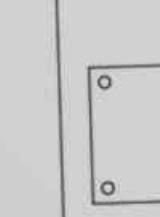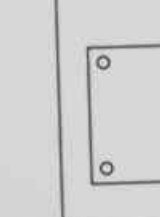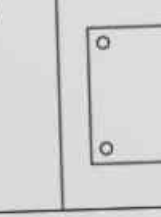MARK	GF TO 2ND	3RD & 4TH	5TH TO 6TH	ROOF-SRR
C1	400x400 8-16Ø 10Ø@100/150 (TIES) 	350x350 8-16Ø 10Ø@100/150 (TIES) 	300x300 8-16Ø 10Ø@100/150 (TIES) 	300x300 8-16Ø 10Ø@100/150 (TIES) 
C2	300x600 10-20Ø 10Ø@100/150 (TIES) 	300x500 8-20Ø 10Ø@100/150 (TIES) 	300x400 8-16Ø 10Ø@100/150 (TIES) 	300x400 8-16Ø 10Ø@100/150 (TIES) 
C3	300x500 8-20Ø TIES 10Ø@100/150 	300x400 8-16Ø 10Ø@100/150 (TIES) 	300x350 6-16Ø 10Ø@100/150 (TIES) 	300x350 6-16Ø 10Ø@100/150 (TIES) 
C4	450x600 12-25Ø 10Ø@100/150 (TIES) 	400x500 10-25Ø 10Ø@100/150 (TIES) 2-20Ø EXTRA  REV B	350x450 8-20Ø 10Ø@100/150 (TIES) 	300x375 6-16Ø 10Ø@100/150 (TIES) 
C5	300x450 8-20Ø 10Ø@100/150 (TIES) 	300x450 8-20Ø 10Ø@100/150 (TIES) 	300x450 6-20Ø 10Ø@100/150 (TIES) 	300x450 6-20Ø 10Ø@100/150 (TIES) 
C6	300x500 8-20Ø 10Ø@100/150 (TIES) 	300x400 8-16Ø 10Ø@100/150 (TIES) 	300x350 6-16Ø 10Ø@100/150 (TIES) 	300x350 6-16Ø 10Ø@100/150 (TIES) 
C7	450x450 8-20Ø 10Ø@100/100 (TIES) 	450x450 8-20Ø 10Ø@100/100 (TIES) 	450x450 8-20Ø 10Ø@100/100 (TIES) 	450x450 8-20Ø 10Ø@100/100 (TIES) 

C2 GF TO 2ND: 12"X24" 12" x 24" 300x600
THE MILLIMETRE CELL GOVERNS; THE INCH CAPTION IS A ROUNDED RESTATEMENT
ALL COLUMNS f'c = 3500 psi, fy = 500 MPa, 40 mm CLEAR COVER



MEGHNA STRUCTURAL CONSULTANTS LTD.
HOUSE 12, ROAD 5, BLOCK 6, BANARI, DHAKA-1213
TEL: +880 2 5555 0000

CIENT
M.S. PADMA HOMES LTD.

PROJECT
PROPOSED G+6 STORIED RESIDENTIAL BUILDING

SITE
PLOT 23, ROAD 7, BLOCK C, BASH
URDHARA R/A, DHAKA

SHEET TITLE
COLUMN SCHEDULE

DESIGNED
S.R.

DRAWN
M.H.

CHECKED
A.K.

APPROVED
T.I.

RAJUK REF. RAJUK/RAP/2026/0417

JOB NO. MSC-2026-041

DATE 12-08-2026

SCALE N.T.S.


SHEET NO. S-11


REV. B

REVISIONS


REV	DATE	DESCRIPTION
A	05-07-2026	ISSUED FOR RAJUK APPROVAL
B	12-08-2026	ON 100-4TH FLOOR REVISED: ISSUED FOR

ALL DIMENSIONS IN mm U.N.O.
DO NOT SCALE THIS DRAWING

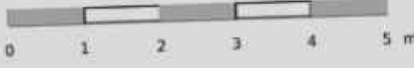


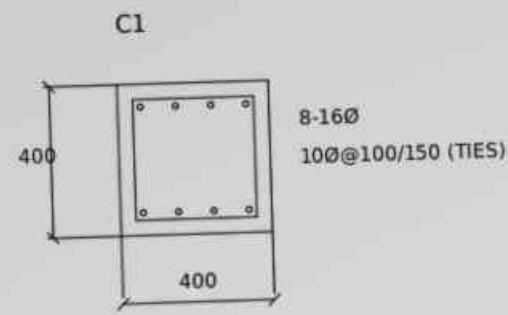


C1 SECTION SCALE 1:20 (DRAWN x5, DIMLFAC 0.2)

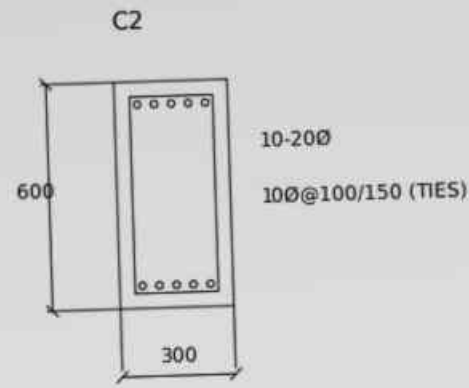


C2 SECTION SCALE 1:20 (DRAWN x5, DIMLFAC 0.2)

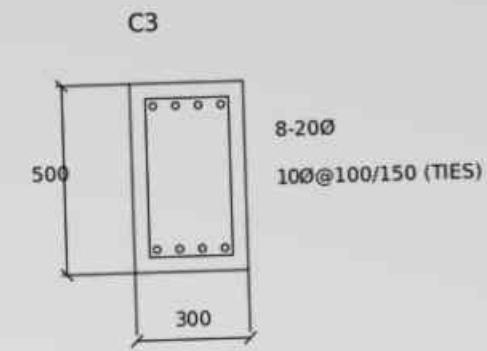


C3 SECTION SCALE 1:20 (DRAWN x5, DIMLFAC 0.2)

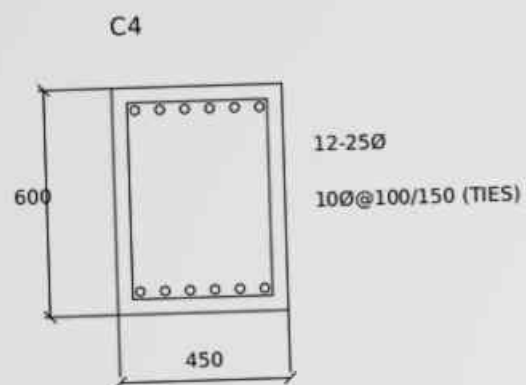


C4 SECTION SCALE 1:20 (DRAWN x5, DIMLFAC 0.2)

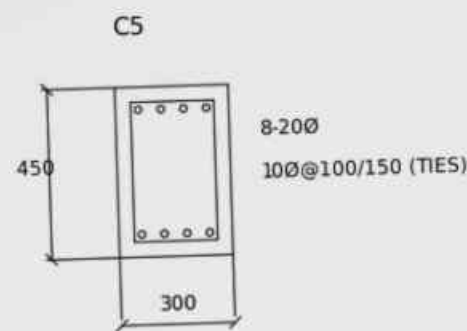

C5 SECTION SCALE 1:20 (DRAWN x5, DIMLFAC 0.2)

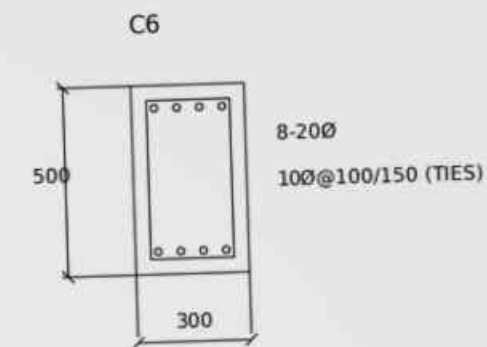


C6 SECTION SCALE 1:20 (DRAWN x5, DIMLFAC 0.2)

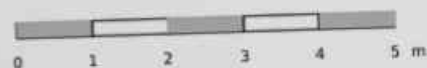




MEGHNA STRUCTURAL CONSULTANT S LTD.			
HOUSE 12, ROAD 5, BLOCK B, BANANI, DHAKA 1213 TEL: +880 2 5555 0000			
CLIENT M/S. PADMA HOMES LTD.			
PROJECT PROPOSED G+6 STORIED RESIDENTIAL BUILDING			
SITE PLOT 23, ROAD 7, BLOCK C, BASH UNDHARA R/A, DHAKA			
SHEET TITLE 1ST FLOOR BEAM LAYOUT			
DESIGNED S.R.	DRAWN M.H.	CHECKED A.K.	APPROVED T.I.
RAJUK REF. RAJUK/BAP/2026/0417			
JOB NO. MSC-2026-041			
DATE 12-08-2026			
SCALE 1:100			
SHEET NO. S-13			REV. B
REVISIONS			
REV	DATE	DESCRIPTION	
A	08-07-2026	ISSUED FOR RAJUK APPROVAL	
B	12-08-2026	ON 3RD-FTH BARS REVISED. ISSUED FOR	

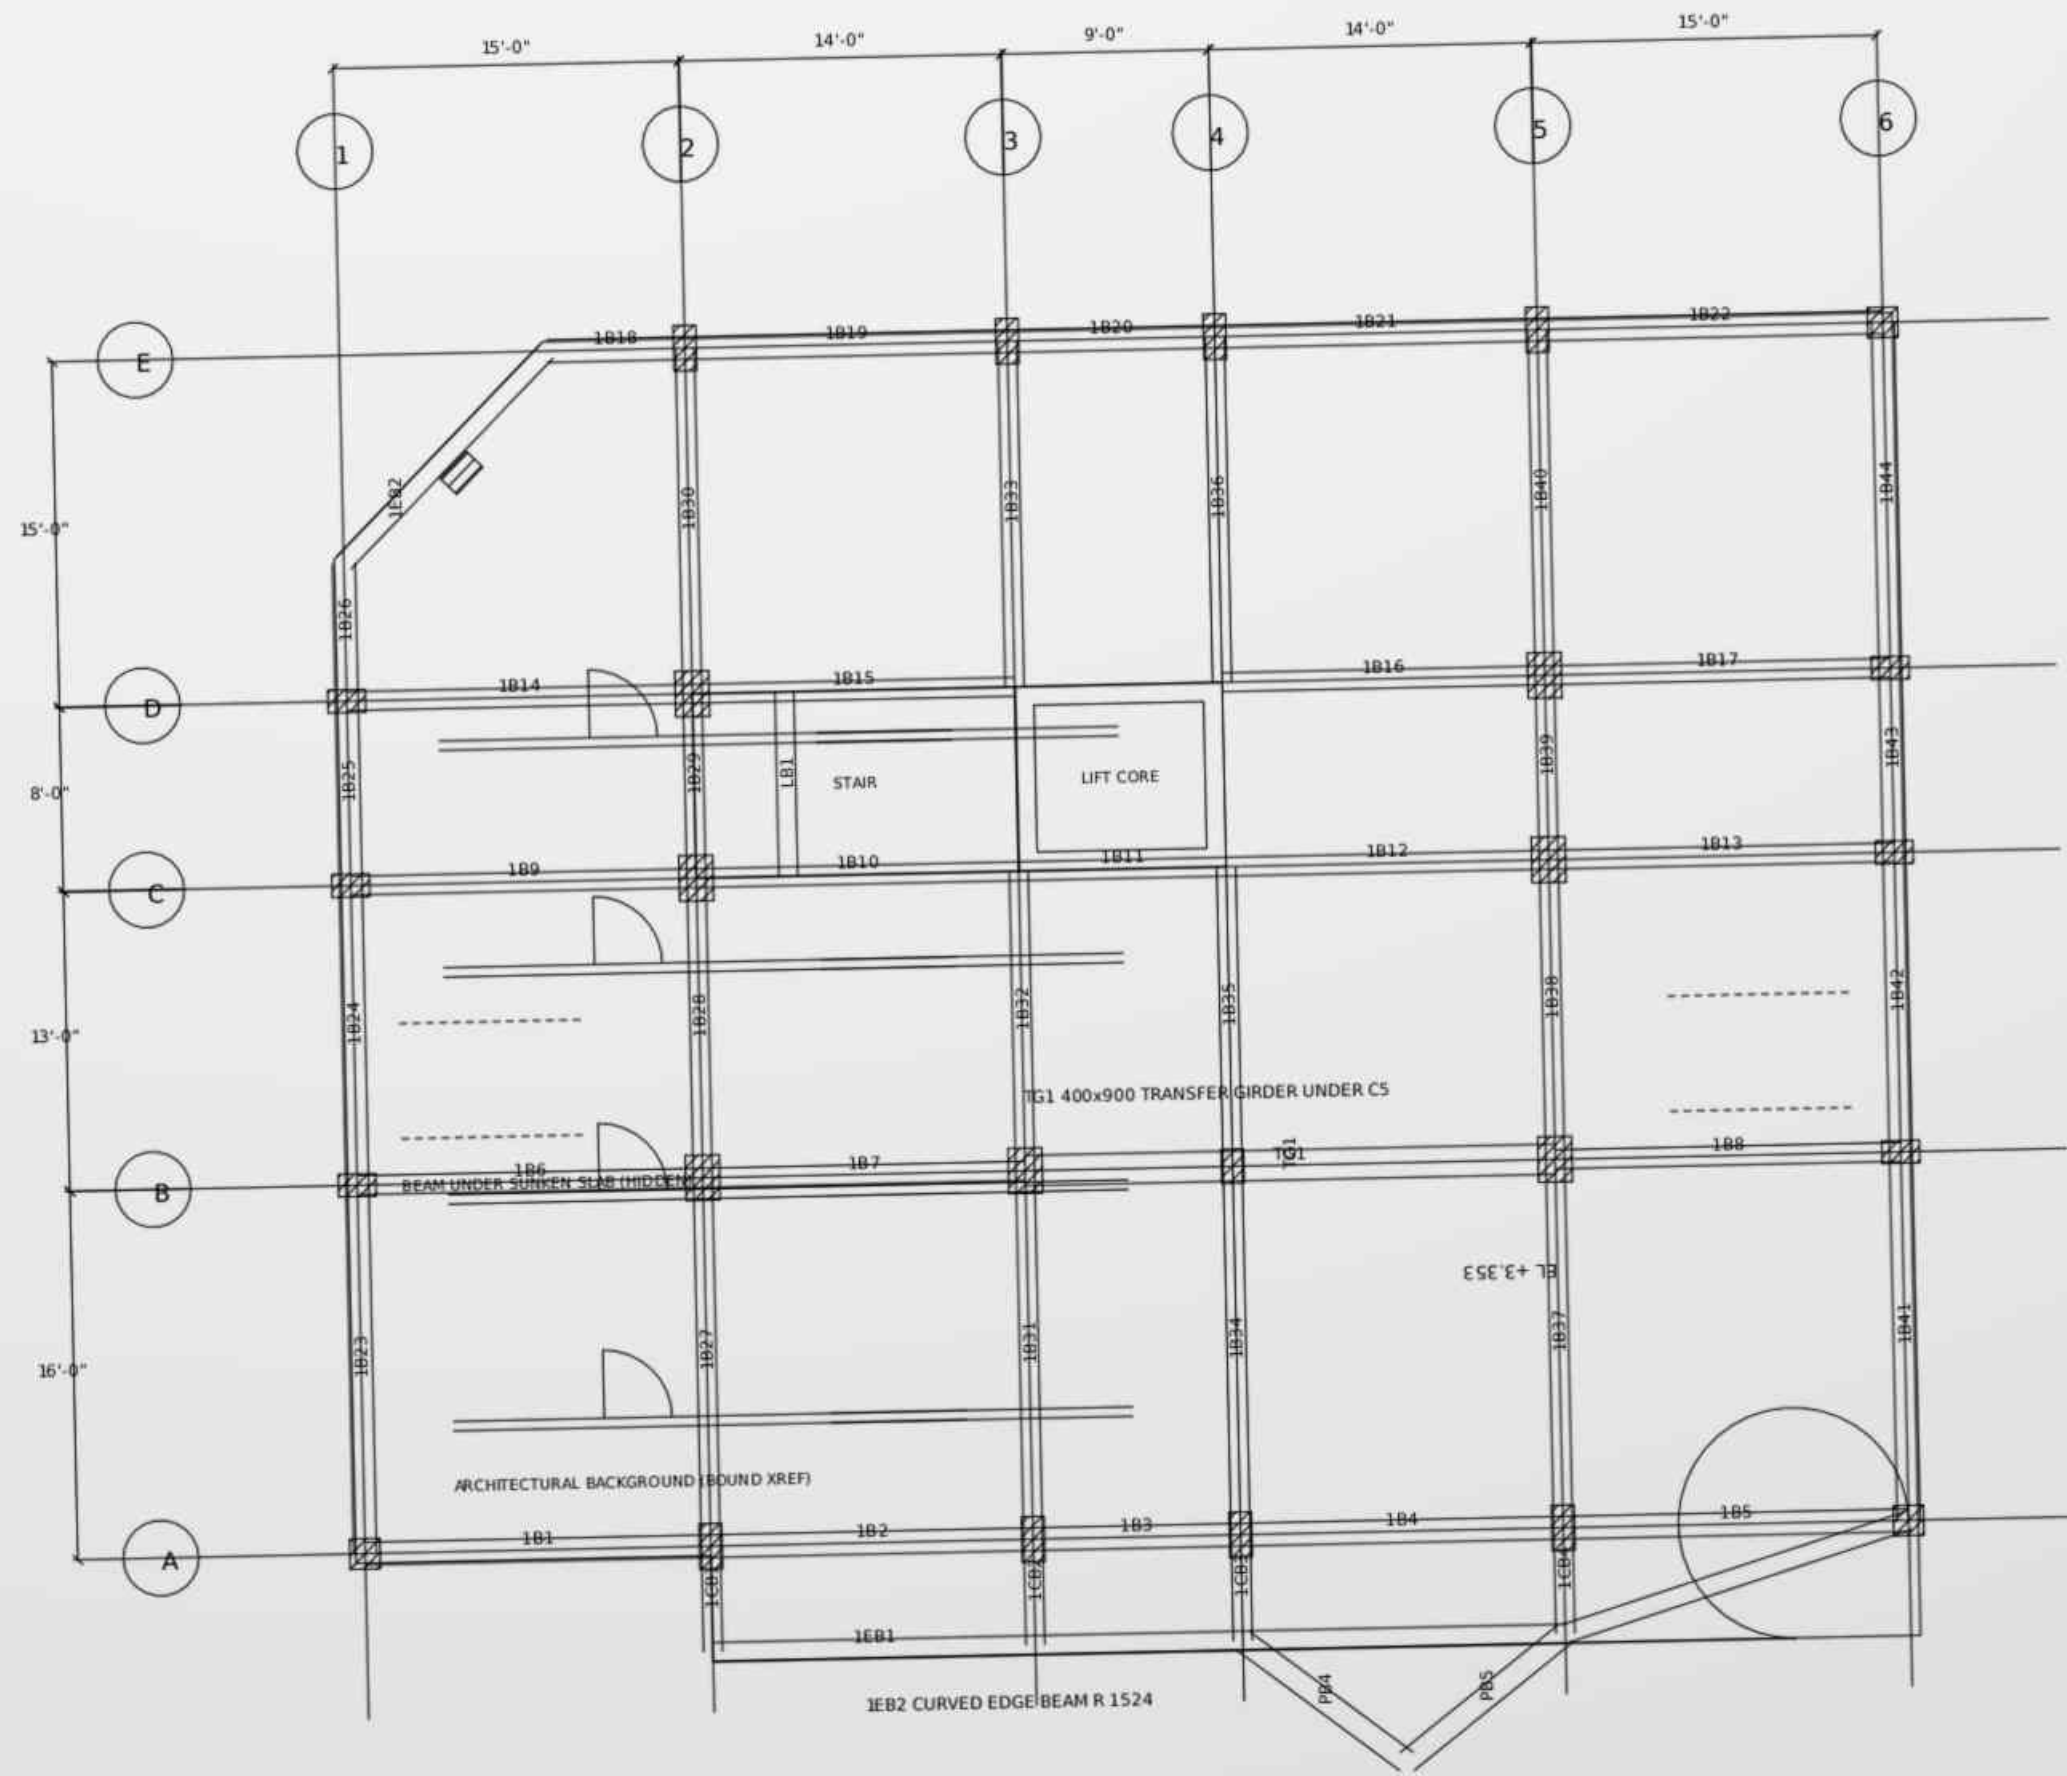


1ST FLOOR BEAM LAYOUT SCALE 1:100

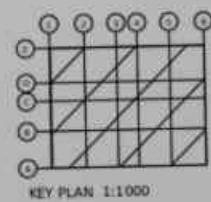




MEGHNA STRUCTURAL CONSULTANT S LTD.			
HOUSE 12, ROAD 9, BLOCK R, BANANI, DHAKA-1213			
TEL: +880 2 5553 0000			
CLIENT			
M/S. PADMA HOMES LTD.			
PROJECT			
PROPOSED G+6 STORED RESIDENTI AL BUILDING			
SITE			
PLOT 23, ROAD 7, BLOCK C, BASH UNDHARA RA, DHAKA			
SHEET TITLE			
TYPICAL FLOOR BEAM LAYOUT (2ND TO 6TH FLOOR)			
DESIGNED	DRAWN	CHECKED	APPROVED
S.R.	M.H.	A.K.	T.I.
RAJUK REF.		RAJUK/BAP/2026/0417	
JOB NO.		MSC-2026-041	
DATE		12-08-2026	
SCALE		1:100	
SHEET NO.		REV.	
S-14		B	
REVISIONS			
DATE	DESCRIPTION		
05-07-2026	ISSUED FOR RAJUK APPROVAL		
12-08-2026	G+6TH BARS REVISED, ISSUED FO		

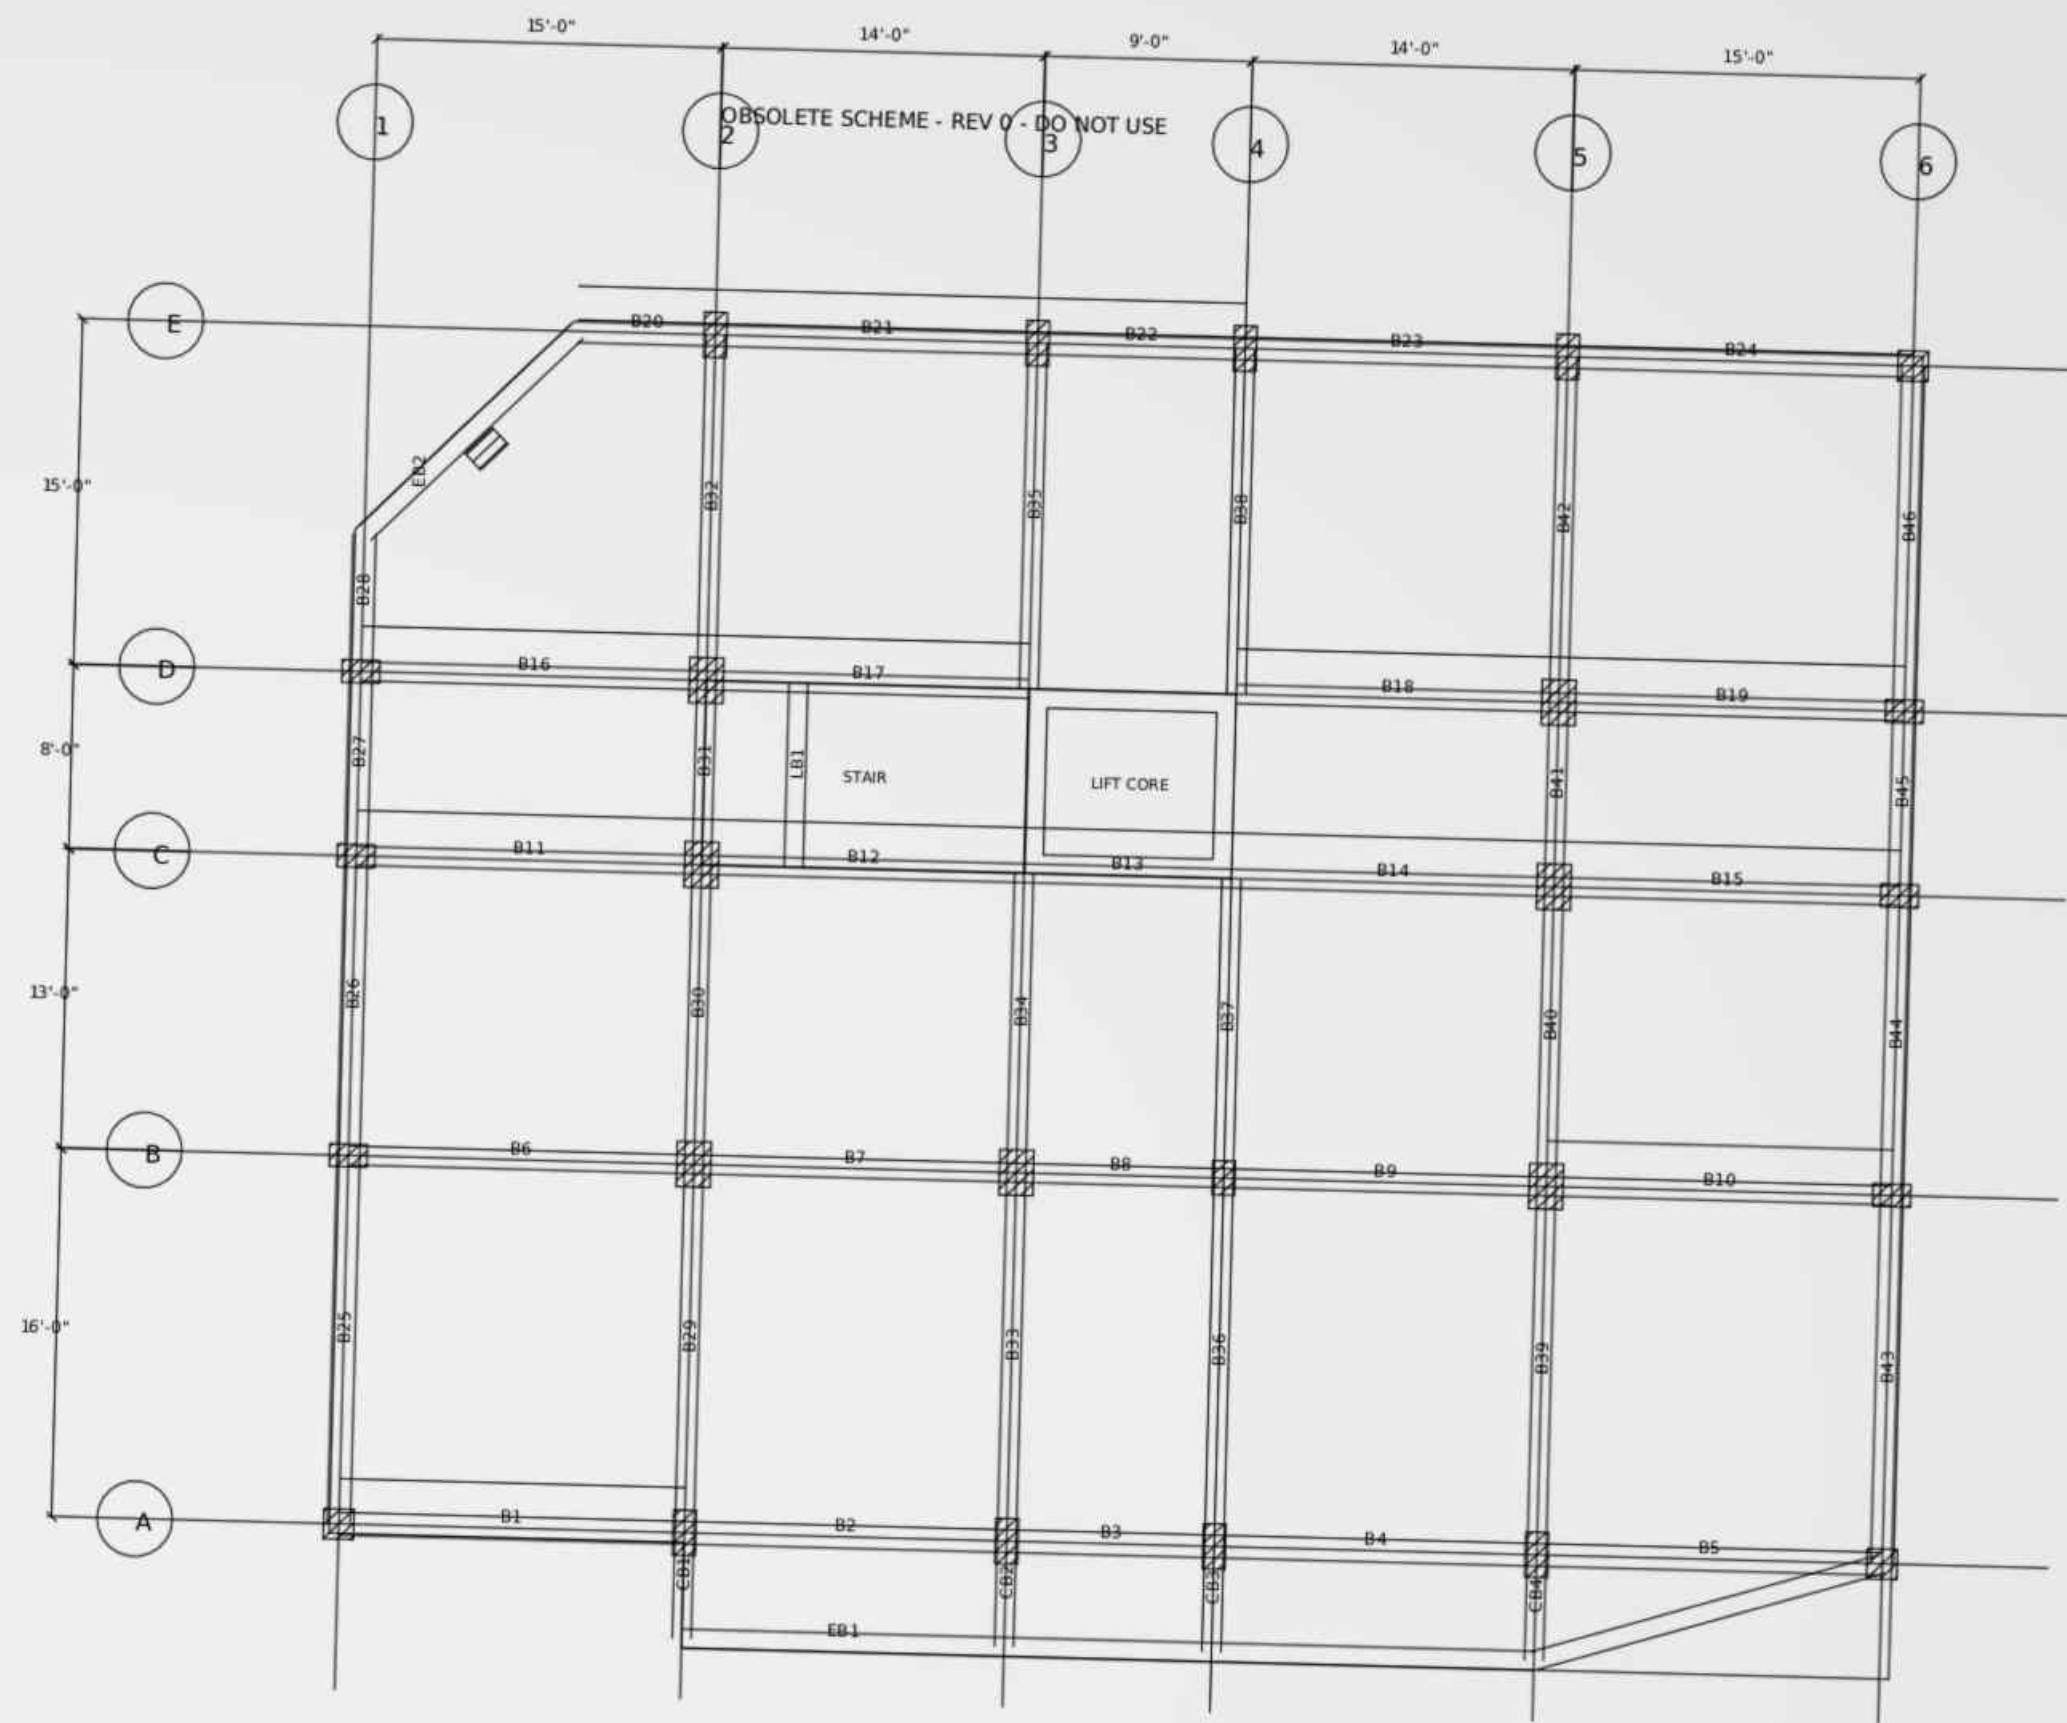

TYPICAL FLOOR BEAM LAYOUT
(2ND TO 6TH FLOOR)

TYPICAL FLOOR BEAM LAYOUT SCALE 1:100

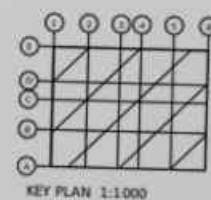


S-14 TYPICAL FLOOR BEAM LAYOUT (2ND TO 6TH FLOOR)

KEY PLAN 1:1000




MEGHNA STRUCTURAL CONSULTANT S LTD.			
HOUSE 12, ROAD 5, BLOCK B, BARIADI, DHAKA-1213 TEL: +880 2 5555 9999			
CLIENT M/S. PADMA HOMES LTD.			
PROJECT PROPOSED G+6 STORIED RESIDENTIAL BUILDING			
SITE PLOT 23, ROAD 7, BLOCK C, BASH UNDHARA N/A, DHAKA			
SHEET TITLE ROOF & STAIR ROOF BEAM LAYOUT			
DESIGNED S.R.	DRAWN M.H.	CHECKED A.K.	APPROVED T.I.
RAJUK REF. RAJUK/BAP/2026/0417			
JOB NO. MSC-2026-041			
DATE 12-08-2026			
SCALE 1:100			
SHEET NO. S-15			REV. B
REVISIONS			
REV	DATE	DESCRIPTION	
A	08-07-2026	REVISION FOR RAJUK APPROVAL	
B	12-08-2026	EX 3RD-FTH BARS REVISED. ISSUED FOR	

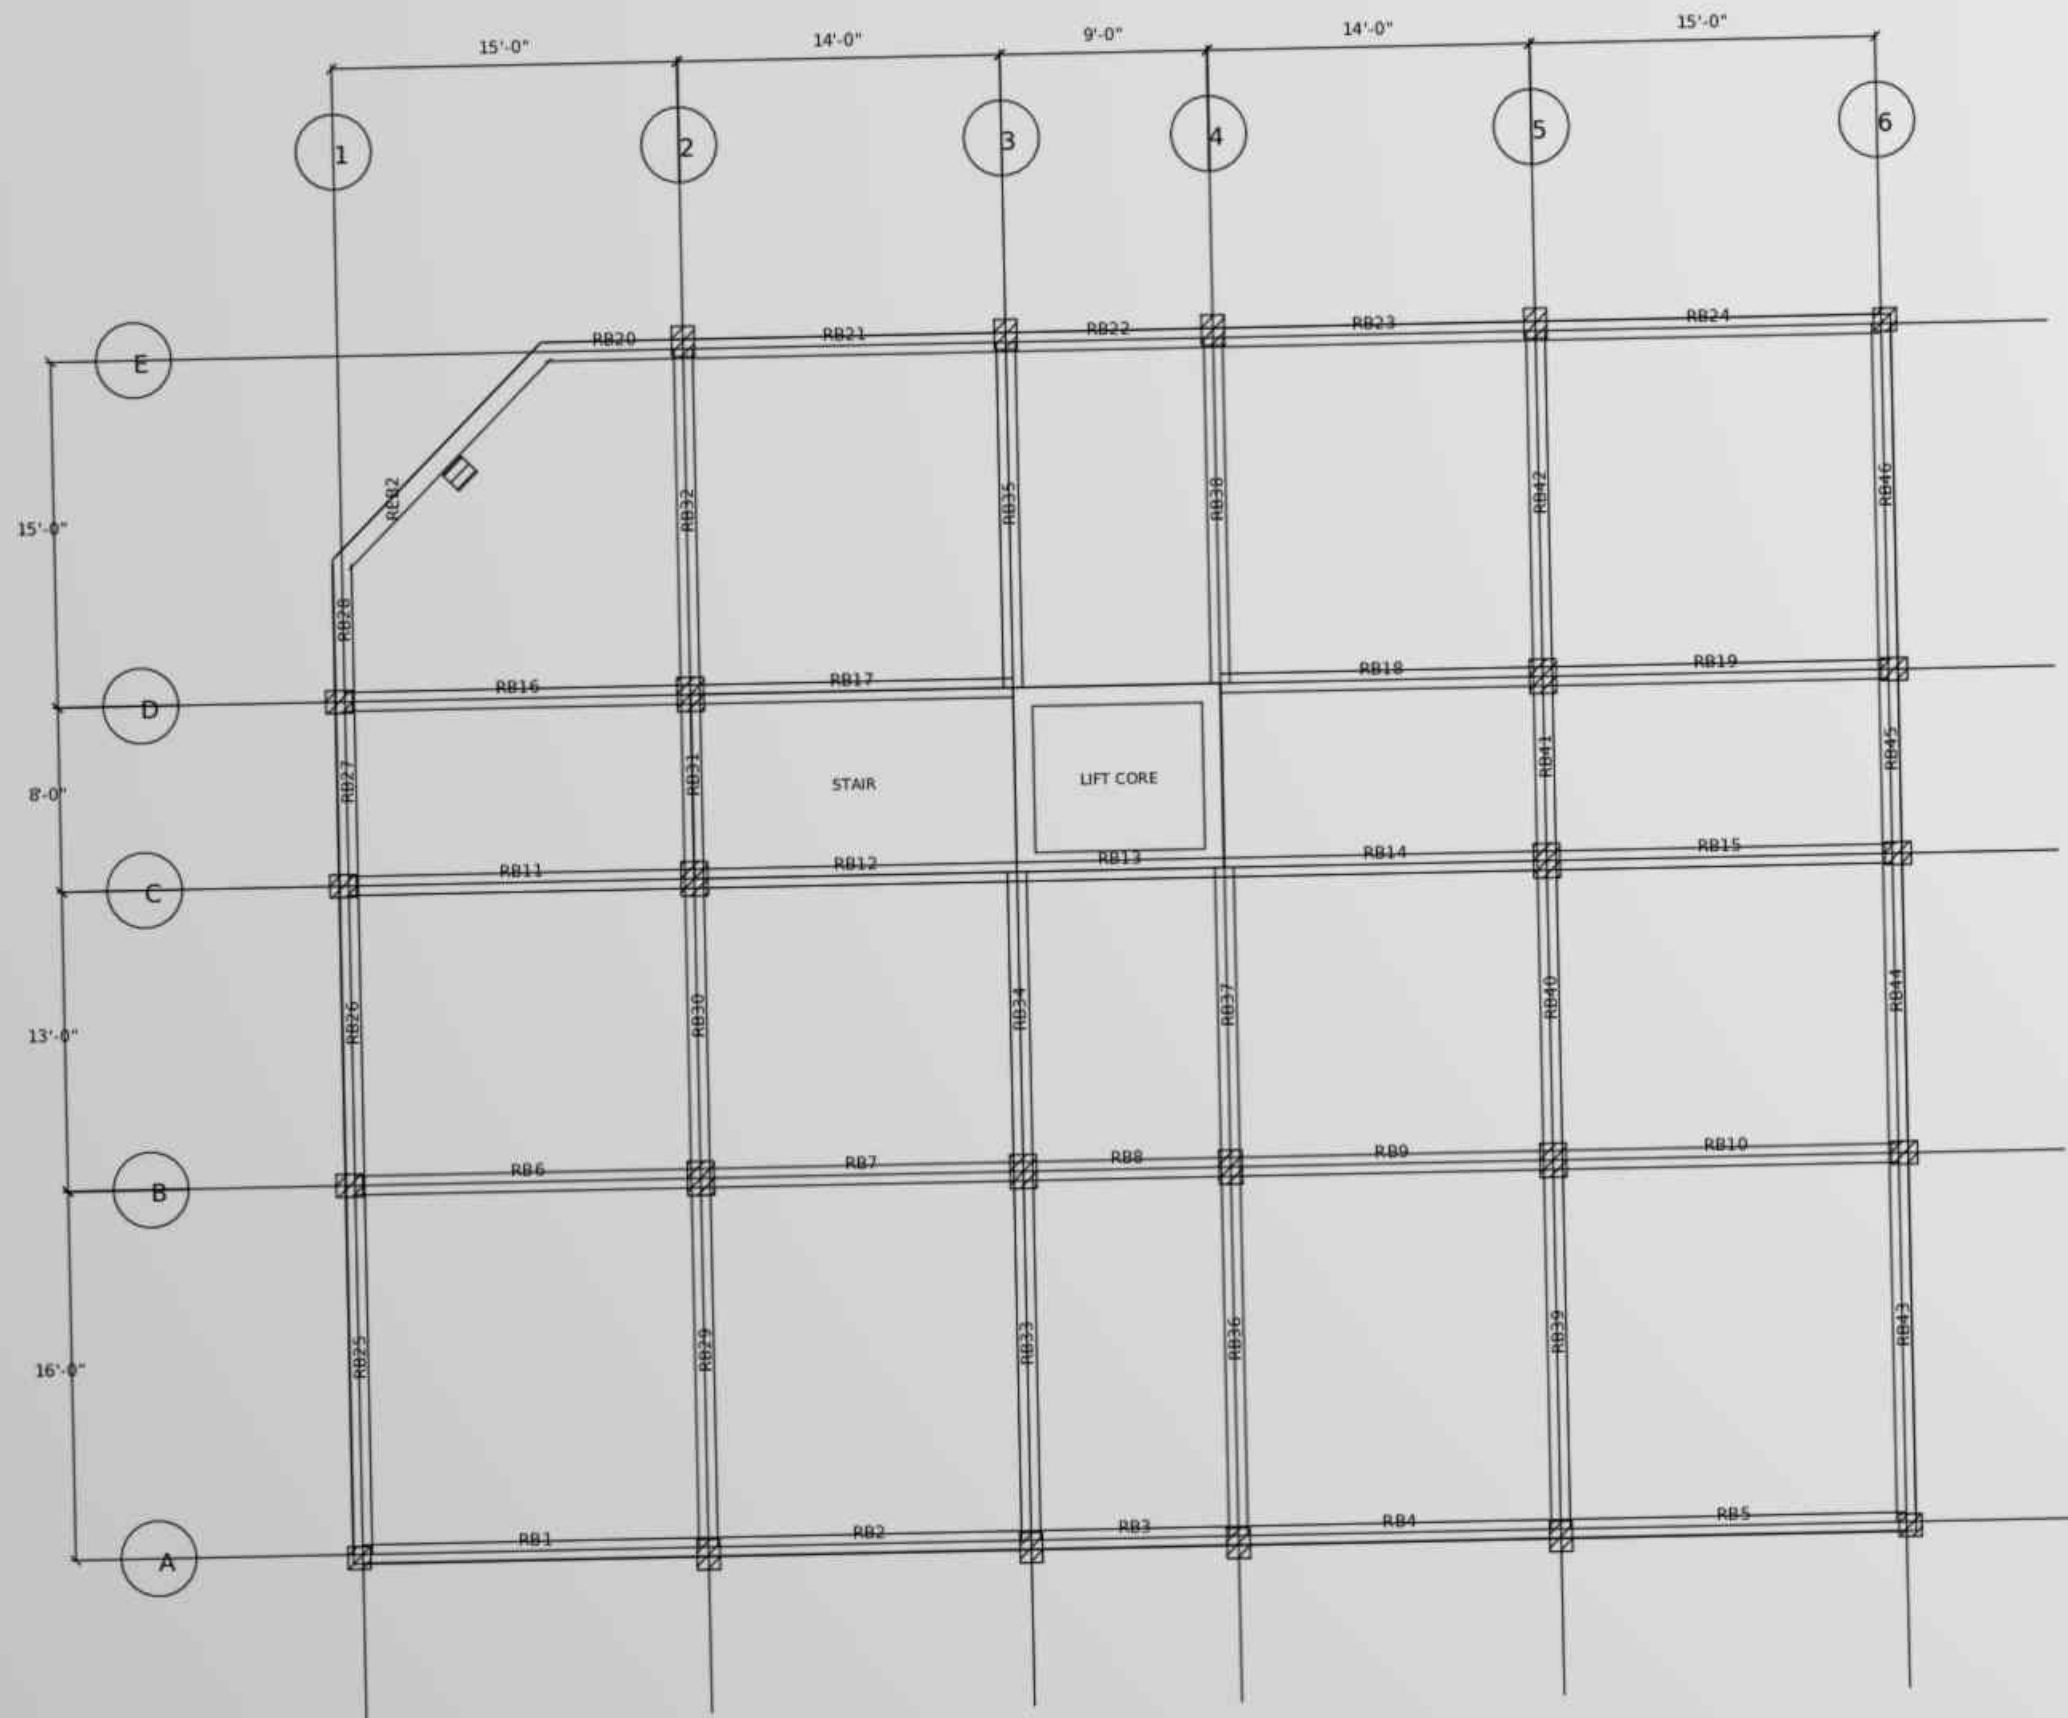


ROOF BEAM LAYOUT (AT ROOF LEVEL)

ROOF BEAM LAYOUT SCALE 1:100

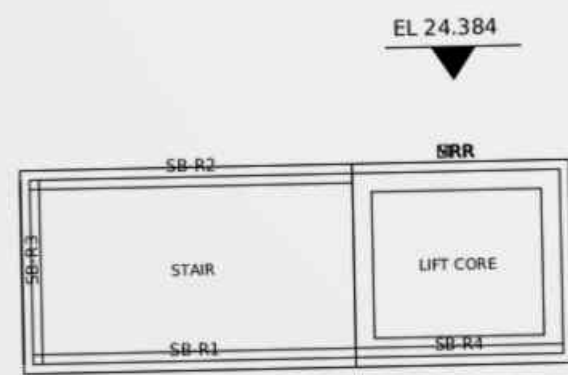


STAIR ROOF & MACHINE ROOM ROOF (5TH TO ROOF)

STAIR ROOF BEAM LAYOUT SCALE 1:100

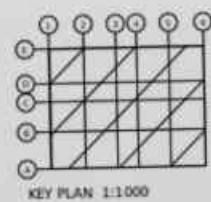

KEY PLAN 1:1000

1ST FLOOR BEAM LONG SECTIONS - TOP, BOTTOM AND EXTRA BARS





















































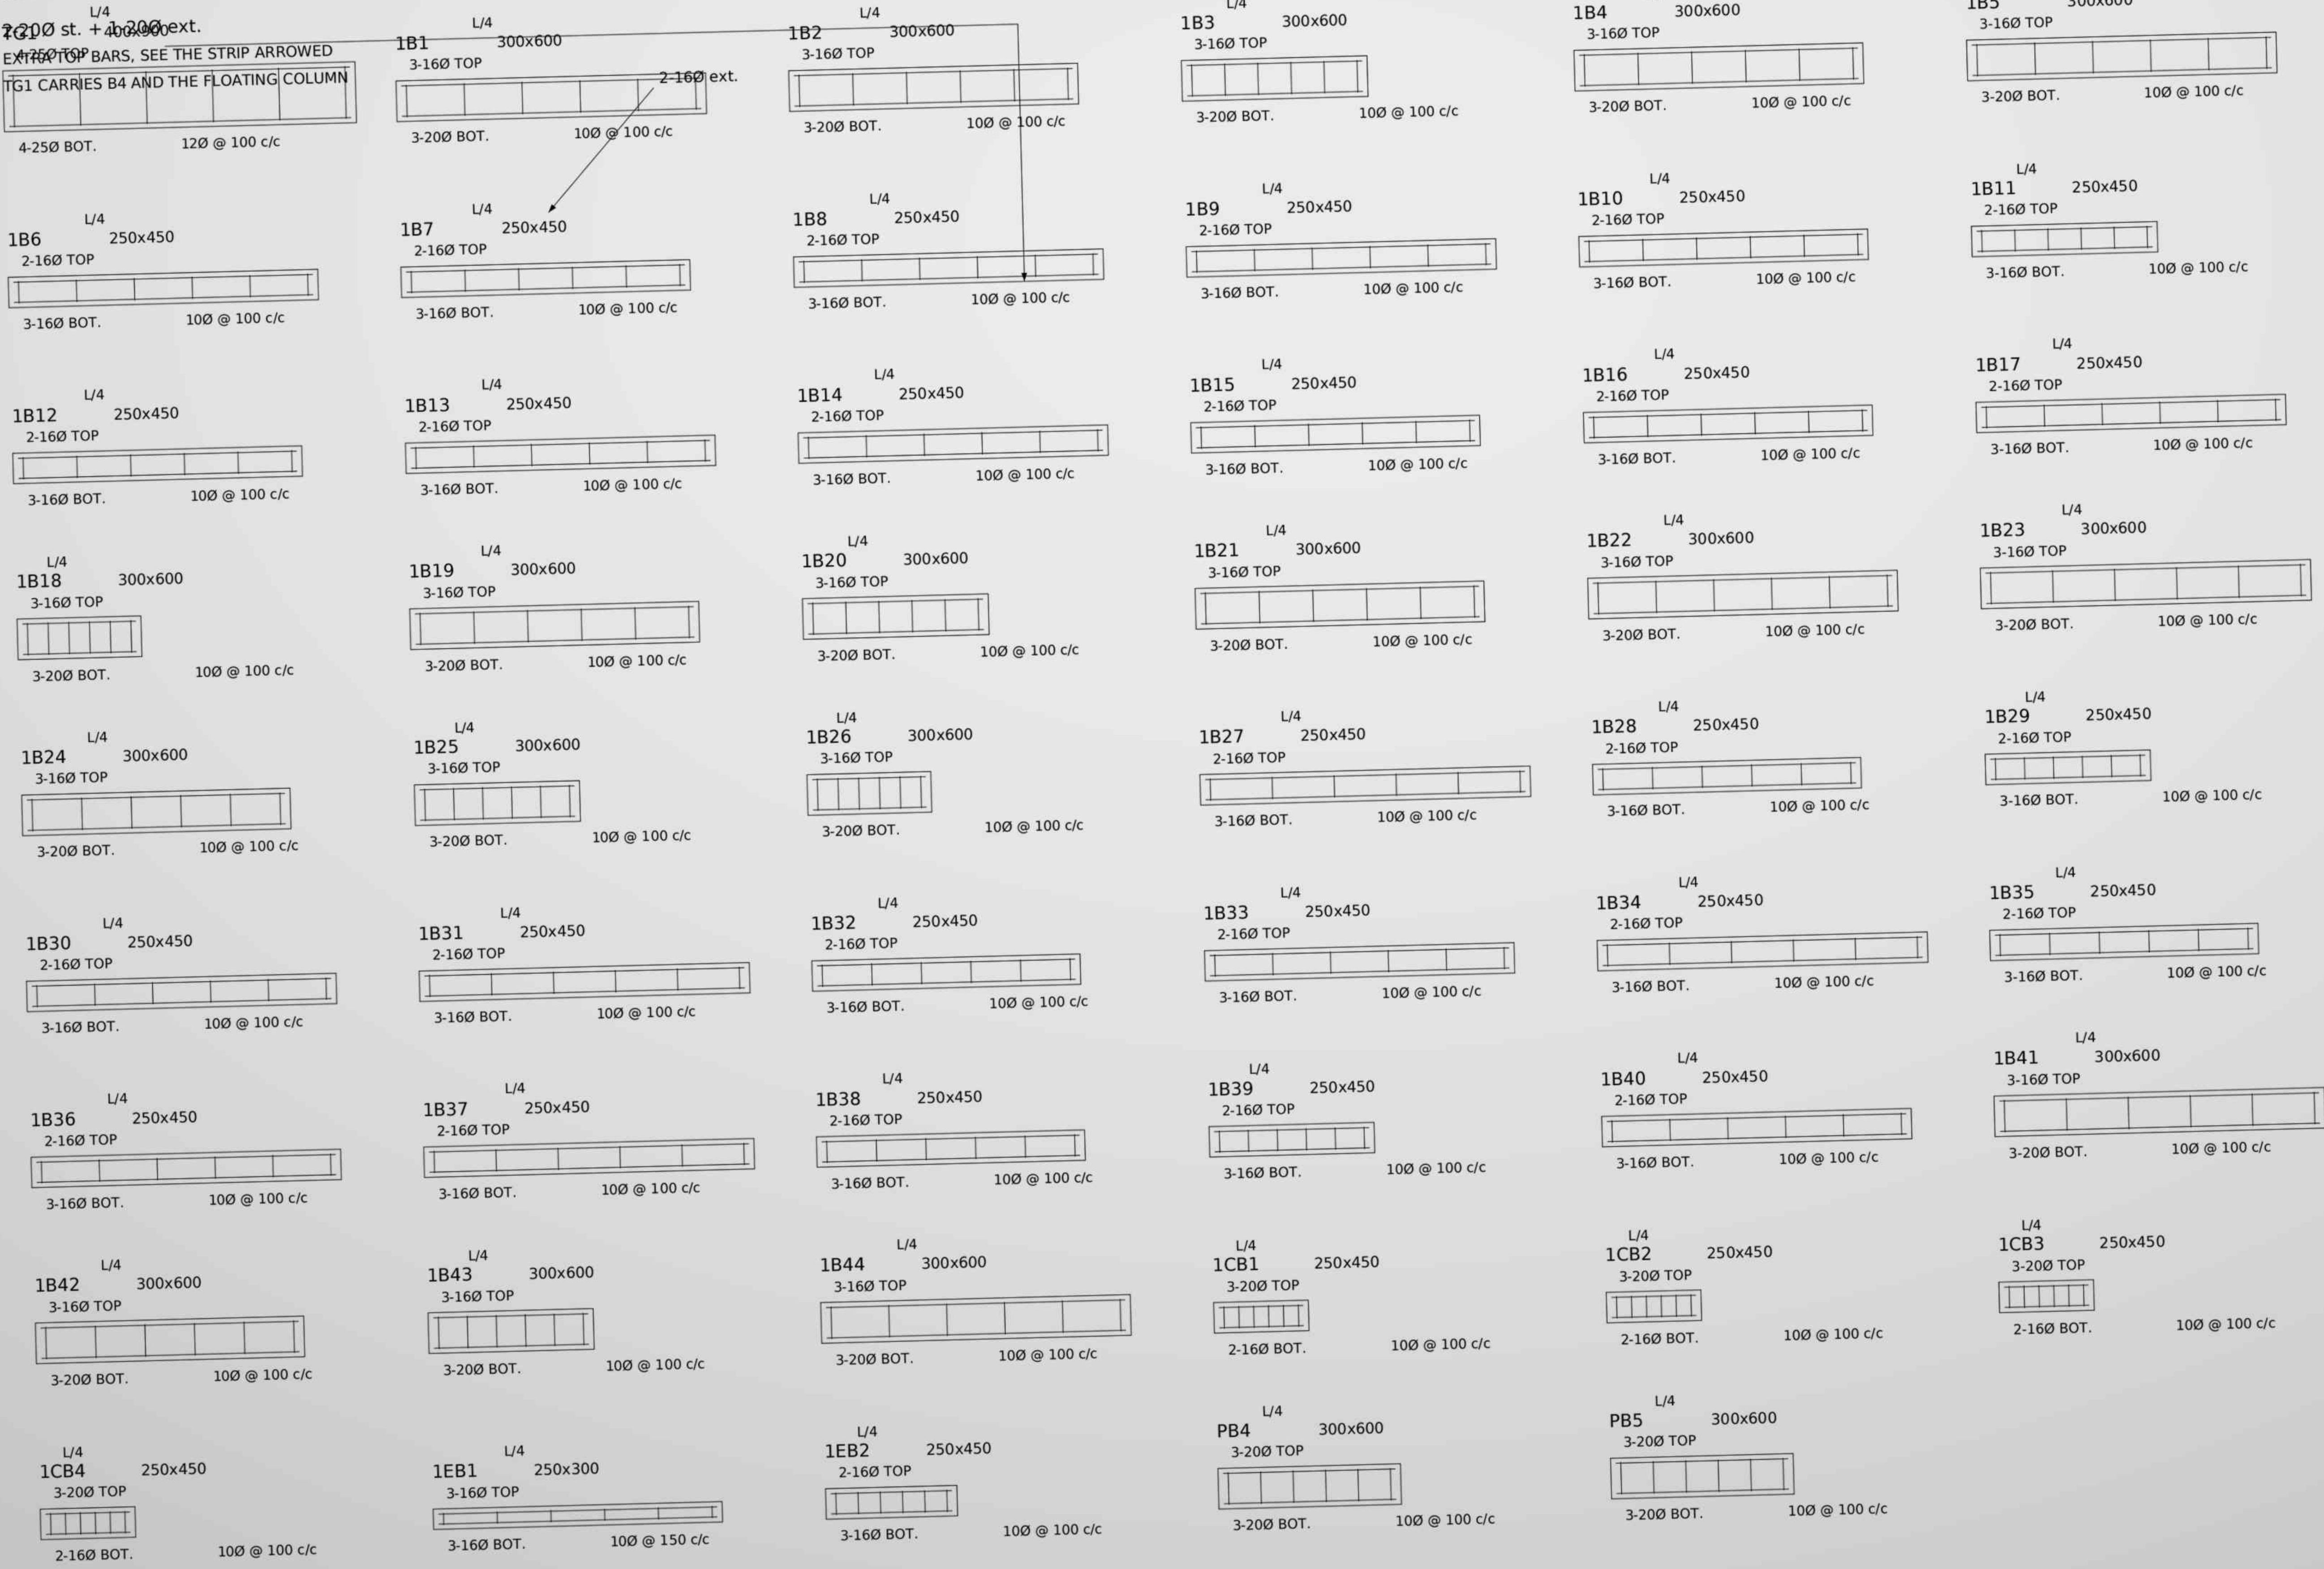


1ST FLOOR BEAM DETAILS SCALE 1:50


MEGHNA STRUCTURAL CONSULTANT S. LTD. HOUSE 12, ROAD 5, BLOCK B, BANANI, DHAKA-1213 TEL: +880 2 5555 0000			
CLIENT M/S. PADMA HOMES LTD.			
PROJECT PROPOSED G+6 STORIED RESIDENTI AL BUILDING			
SITE PLOT 23, ROAD 7, BLOCK C, BASH UNDHARA R/A, DHAKA			
SHEET TITLE BEAM DETAILS (1 OF 3) - 1ST FL OOR			
DESIGNED	DRAWN	CHECKED	APPROVED
S.R.	M.H.	A.K.	T.I.
RAJUK REF. RAJUK/BAP/2026/0417			
JOB NO. MSC-2026-041			
DATE 12-08-2026			
SCALE 1:50			
SHEET NO. S-16			REV. B
REVISIONS			
REV	DATE	DESCRIPTION	
A	05-07-2026	ISSUED FOR RAJUK APPROVAL	
B	12-08-2026	ON 3RD-4TH BARS REVISED, ISSUED PD	

ALL DIMENSIONS IN mm U.N.O.
DO NOT SCALE THIS DRAWING

TYPICAL FLOOR BEAM LONG SECTIONS (2ND TO 6TH FLOOR)

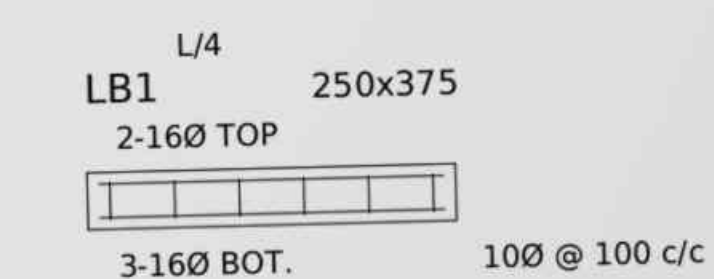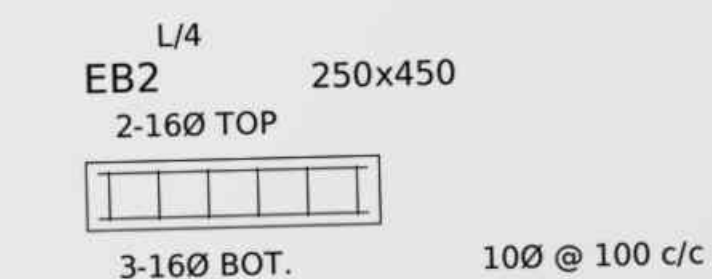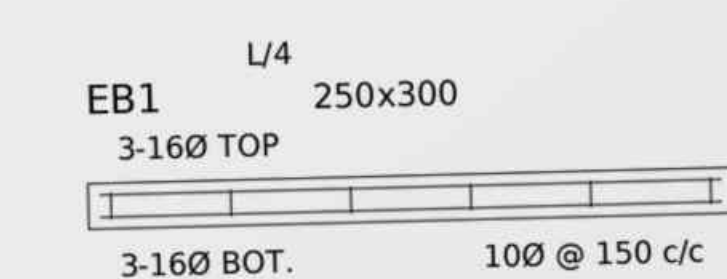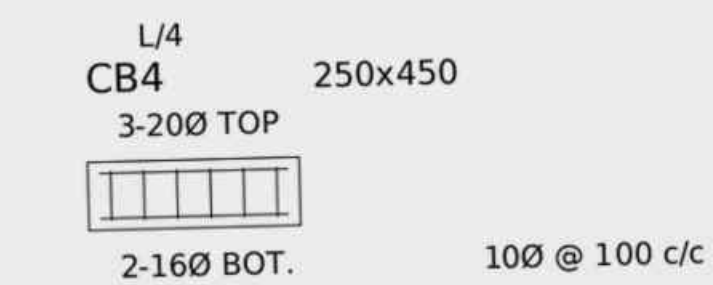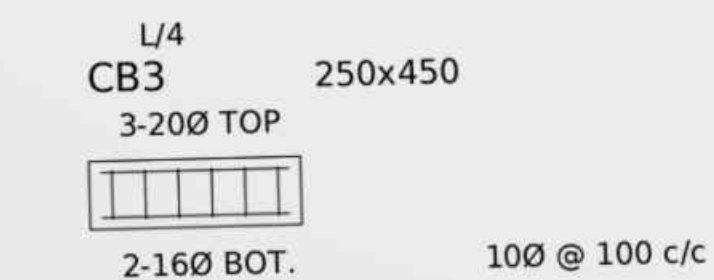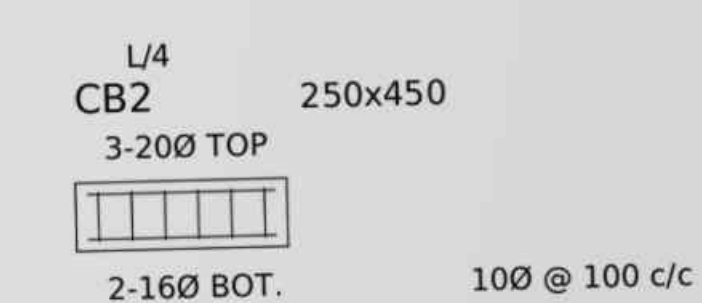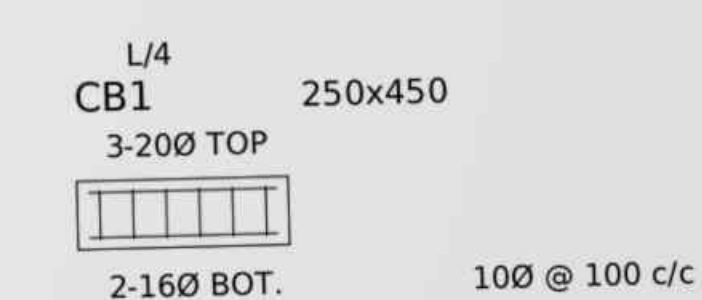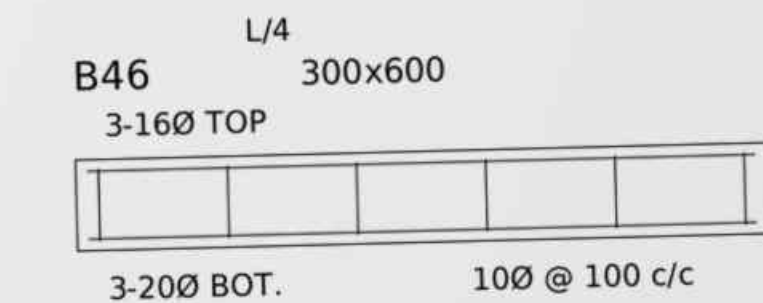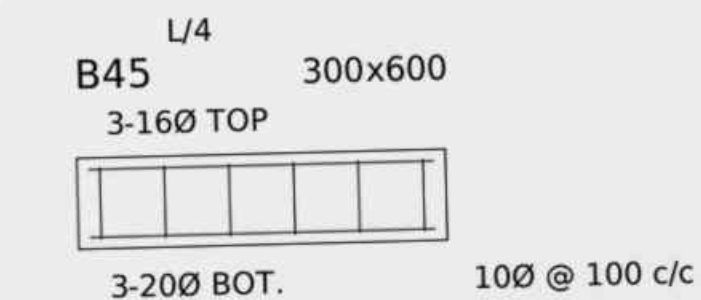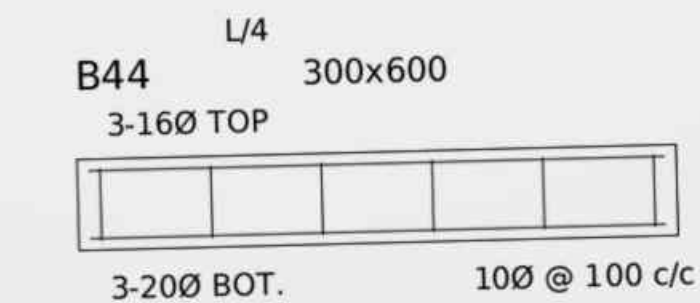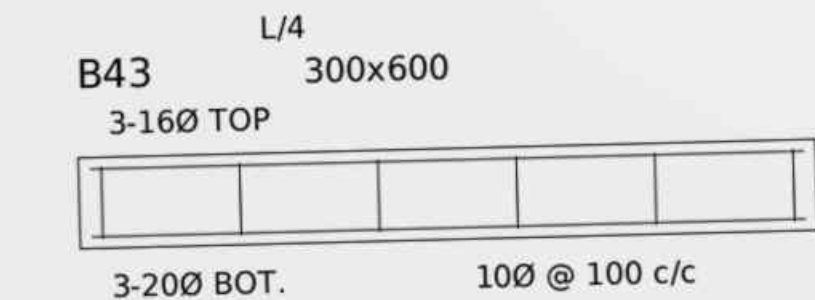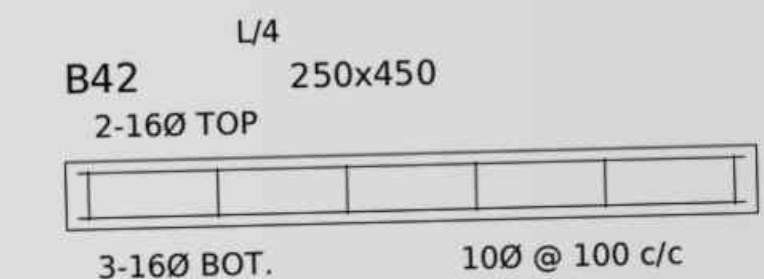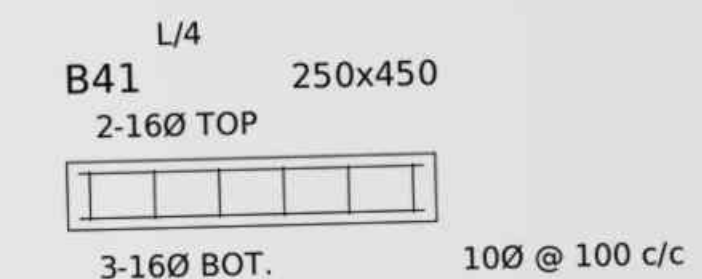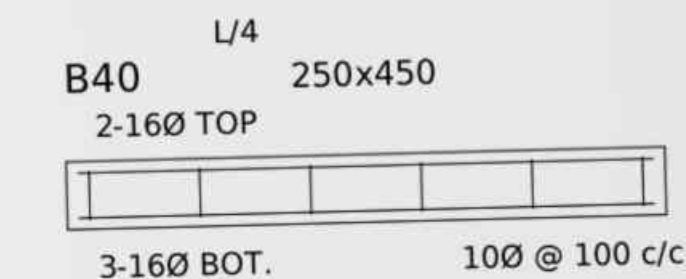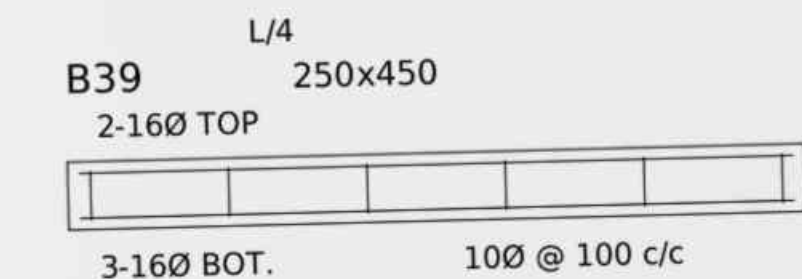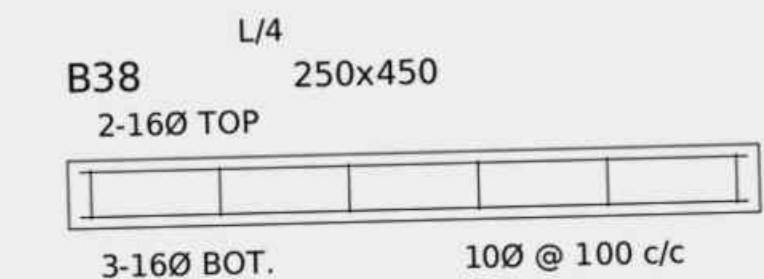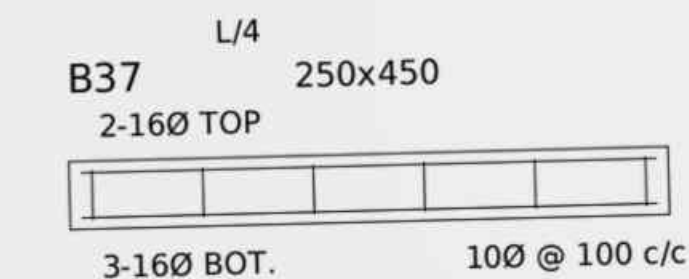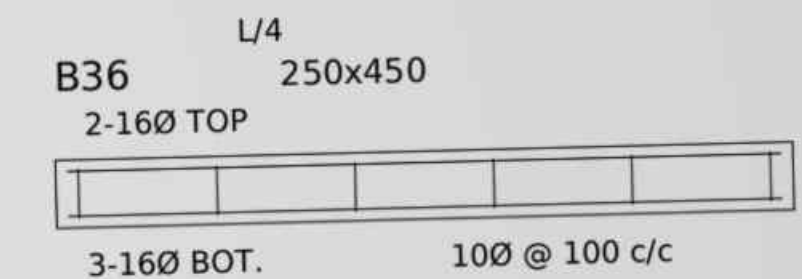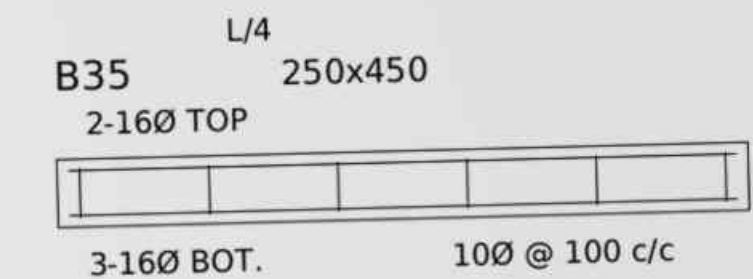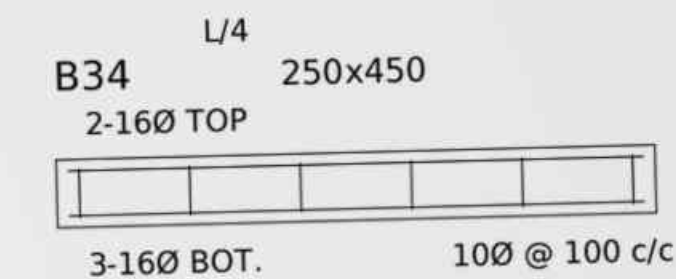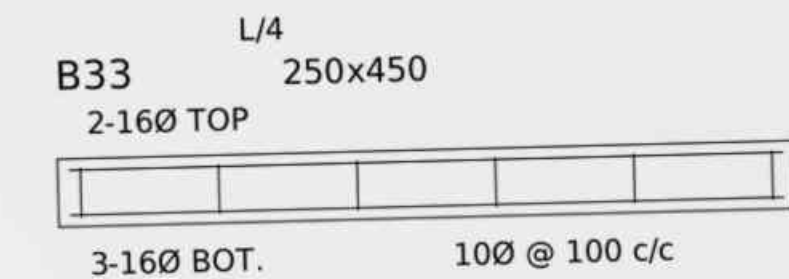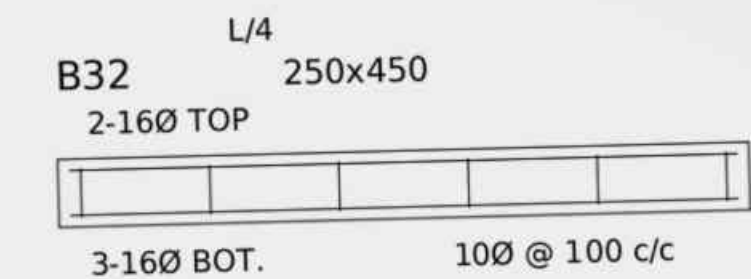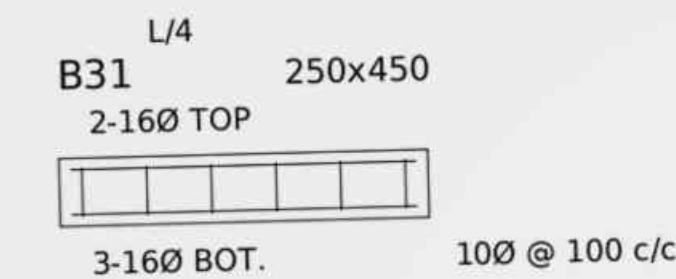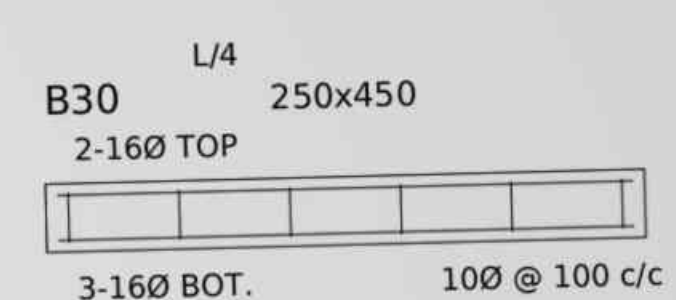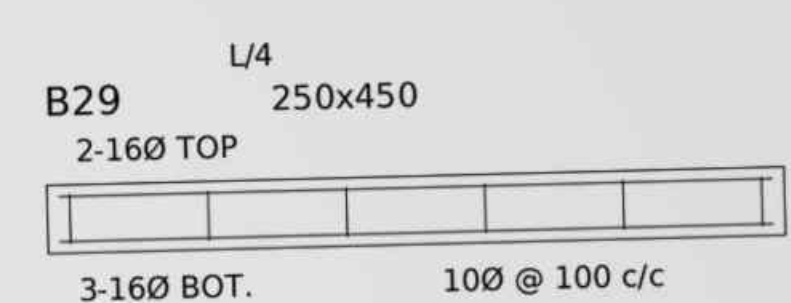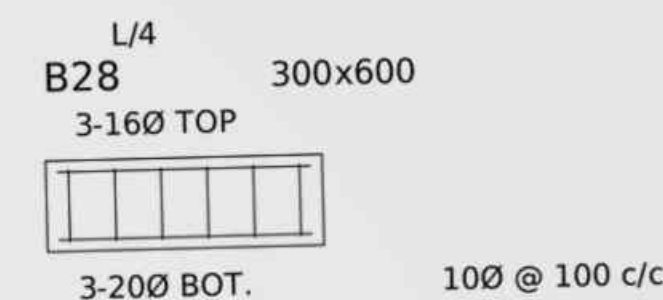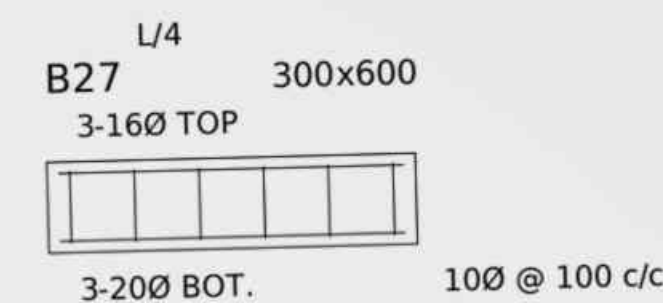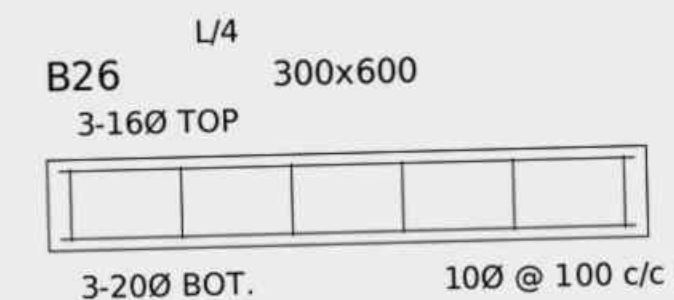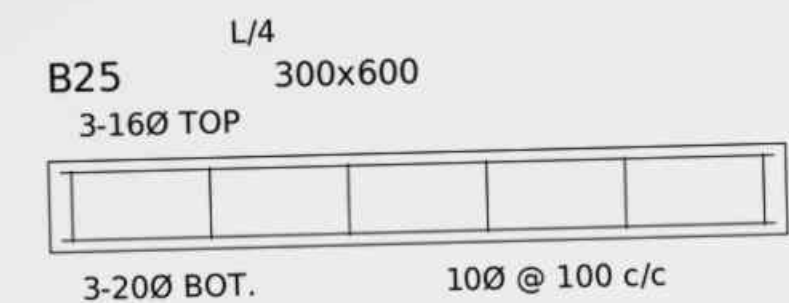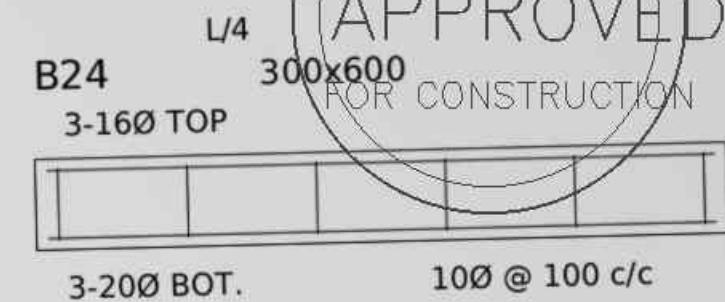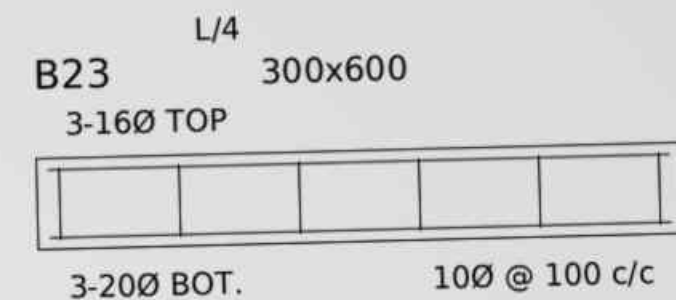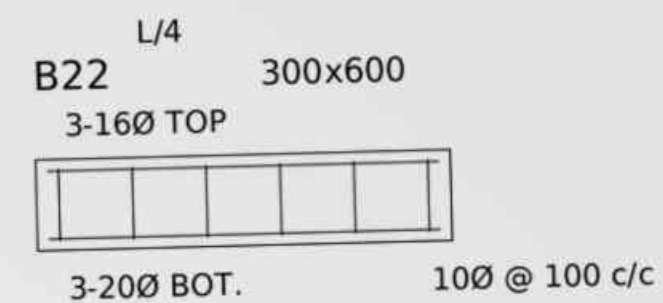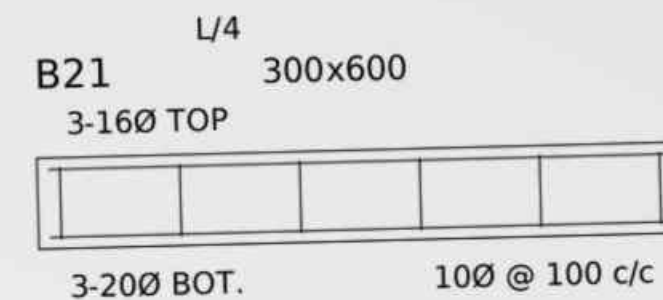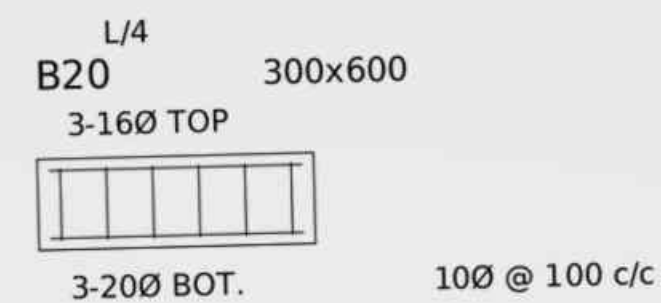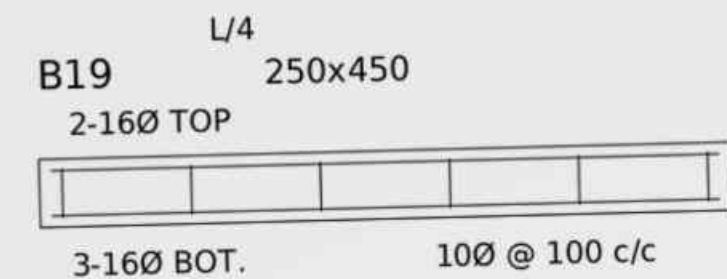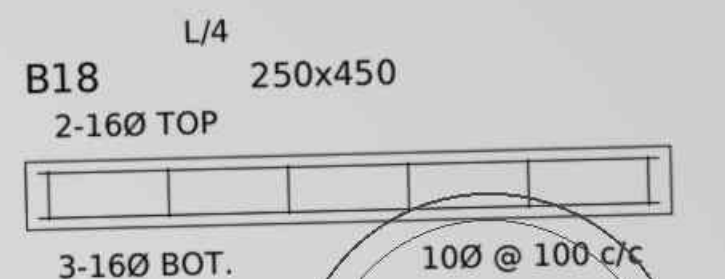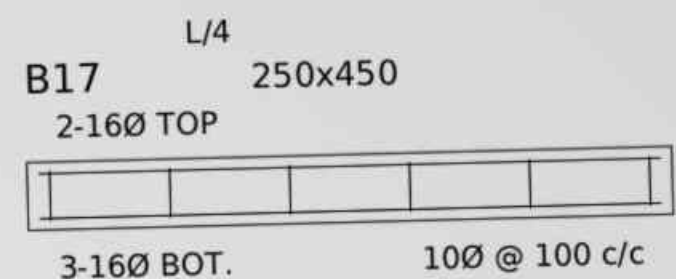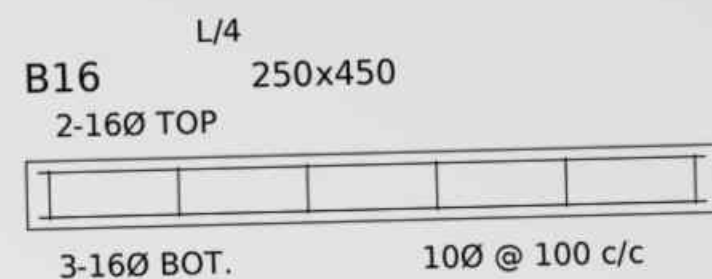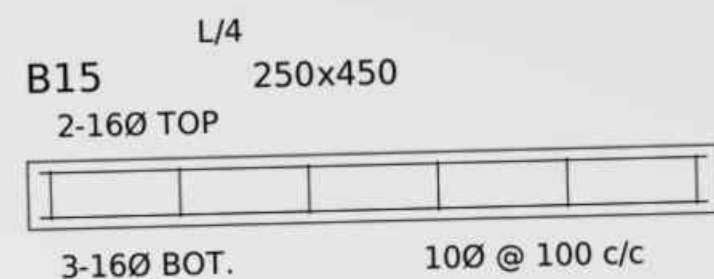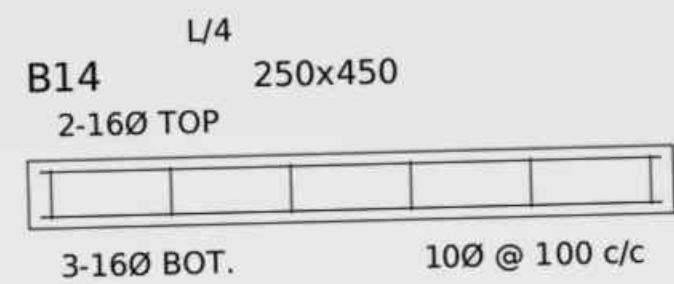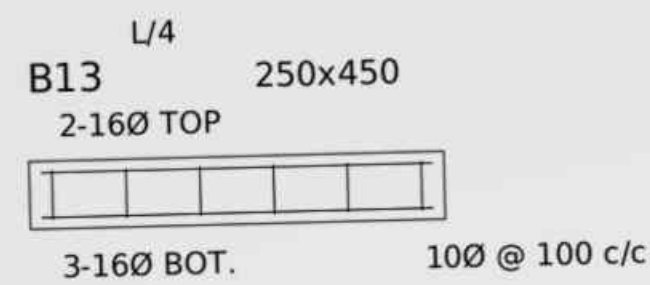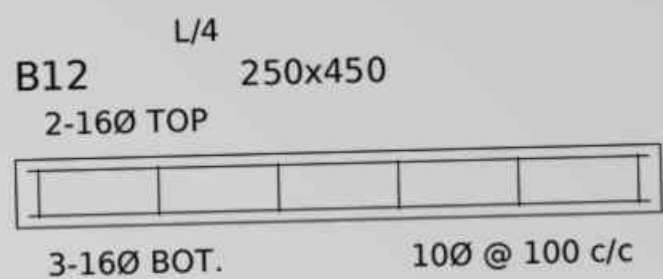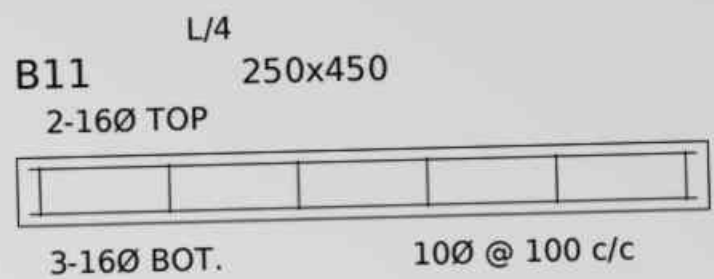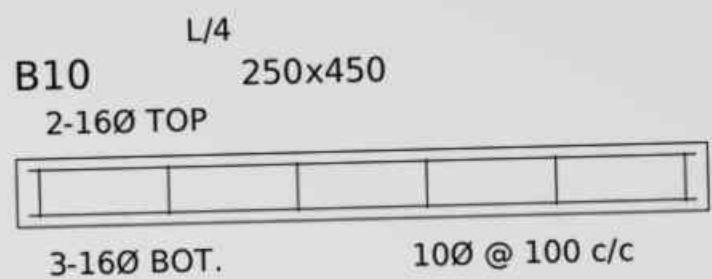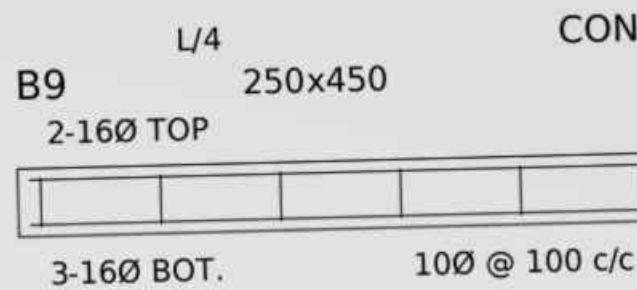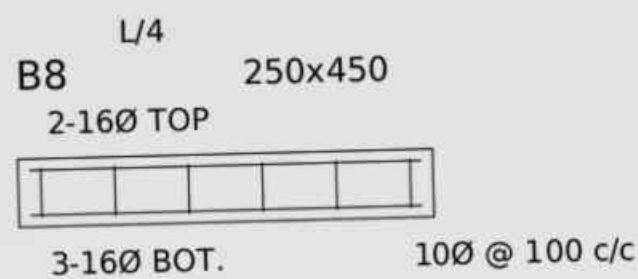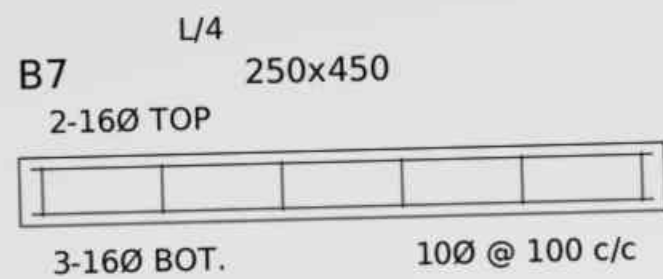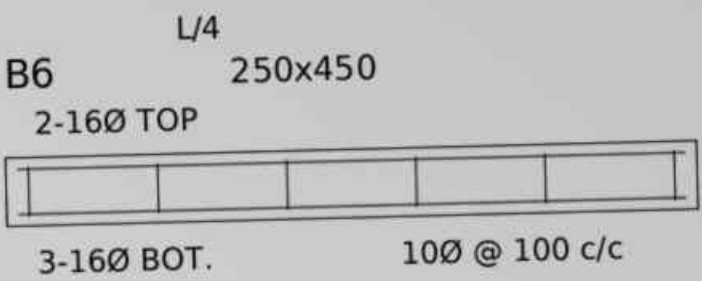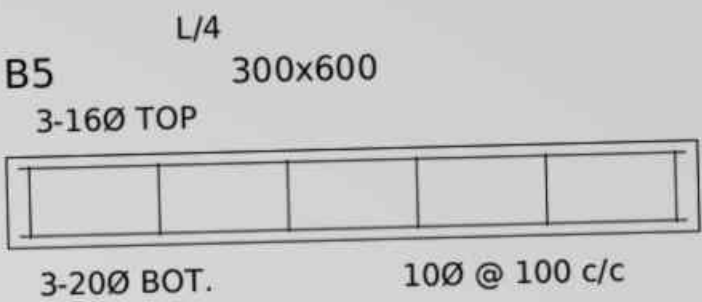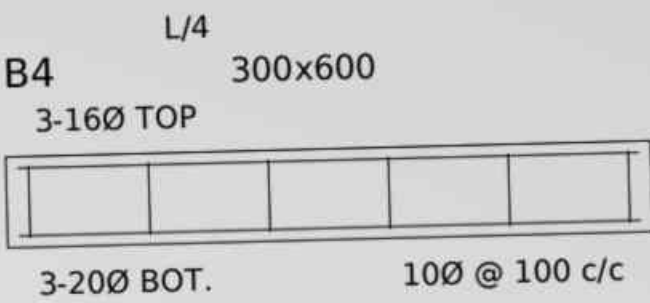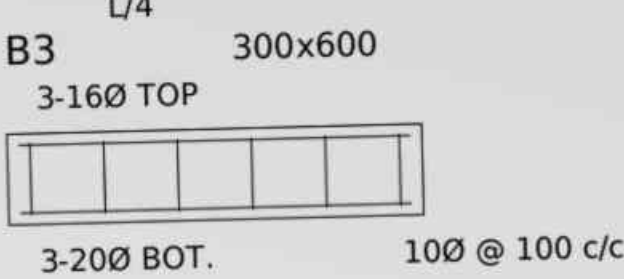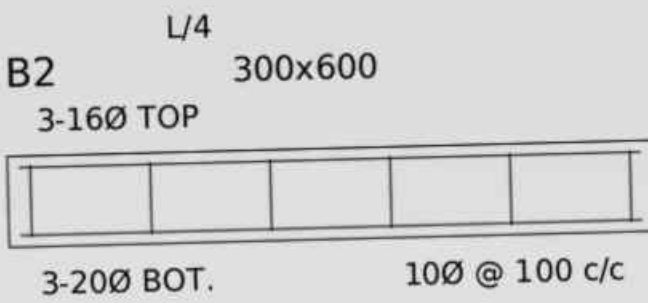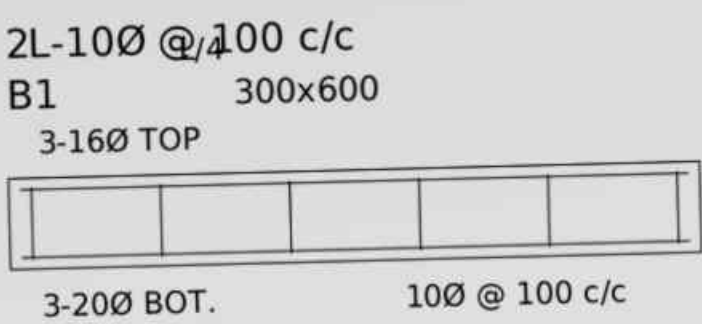

TYPICAL FLOOR BEAM DETAILS SCALE 1:50

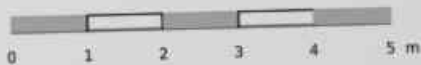

MEGHNA STRUCTURAL CONSULTANT
S LTD.
HOUSE 12, ROAD 5, BLOCK B, BANANI, DHAKA-1213
TEL: +880 2 5555 9000

CLIENT
M/S. PADMA HOMES LTD.

PROJECT
PROPOSED G+6 STORIED RESIDENTIAL BUILDING

SITE
PLOT 23, ROAD 7, BLOCK C, BASH
UNDHARA RA, DHAKA

SHEET TITLE
BEAM DETAILS (2 OF 3) - TYPICAL

DESIGNED	DRAWN	CHECKED	APPROVED
S.R.	M.H.	A.K.	T.I.

RAJUK REF. RAJUK/BAP/2026/0417

JOB NO. MSC-2026-041

DATE 12-08-2026

SCALE 1:50

SHEET NO. S-17

REV. B

REV.	DATE	DESCRIPTION
A	05-07-2026	ISSUED FOR RAJUK APPROVAL
B	12-08-2026	ON 160-4TH BARS REVISION, ISSUED FOR CONSTRUCTION

ALL DIMENSIONS IN mm U.N.O.
DO NOT SCALE THIS DRAWING

ROOF BEAM SCHEDULE (1 OF 2)

MARK	SIZE	SPAN (mm)	TOP	BOTTOM	STIRRUPS
RB1	250x400	4572	2-16Ø	3-16Ø	10Ø@100
RB2	250x400	4267	2-16Ø	3-16Ø	10Ø@100
RB3	250x400	2743	2-16Ø	3-16Ø	10Ø@100
RB4	250x400	4267	2-16Ø	3-16Ø	10Ø@100
RB5	250x400	4572	2-16Ø	3-16Ø	10Ø@100
RB6	250x400	4572	2-16Ø	3-16Ø	10Ø@100
RB7	250x400	4267	2-16Ø	3-16Ø	10Ø@100
RB8	250x400	2743	2-16Ø	3-16Ø	10Ø@100
RB9	250x400	4267	2-16Ø	3-16Ø	10Ø@100
RB10	250x400	4572	2-16Ø	3-16Ø	10Ø@100
RB11	250x400	4572	2-16Ø	3-16Ø	10Ø@100
RB12	250x400	4267	2-16Ø	3-16Ø	10Ø@100
RB13	250x400	2743	2-16Ø	3-16Ø	10Ø@100
RB14	250x400	4267	2-16Ø	3-16Ø	10Ø@100
RB15	250x400	4572	2-16Ø	3-16Ø	10Ø@100
RB16	250x400	4572	2-16Ø	3-16Ø	10Ø@100
RB17	250x400	4267	2-16Ø	3-16Ø	10Ø@100
RB18	250x400	4267	2-16Ø	3-16Ø	10Ø@100
RB19	250x400	4572	2-16Ø	3-16Ø	10Ø@100
RB20	250x400	1829	2-16Ø	3-16Ø	10Ø@100
RB21	250x400	4267	2-16Ø	3-16Ø	10Ø@100
RB22	250x400	2743	2-16Ø	3-16Ø	10Ø@100
RB23	250x400	4267	2-16Ø	3-16Ø	10Ø@100
RB24	250x400	4572	2-16Ø	3-16Ø	10Ø@100
RB25	250x400	4877	2-16Ø	3-16Ø	10Ø@100
RB26	250x400	3962	2-16Ø	3-16Ø	10Ø@100

ROOF BEAM SCHEDULE 1 SCALE 1:50

3T16 + 2Y16

(T AND Y BOTH MEAN A DEFORM

ROOF BEAM SCHEDULE (2 OF 2)


MARK	SIZE	SPAN (mm)	TOP	BOTTOM	STIRRUPS
RB27	250x400	2438	2-16Ø	3-16Ø	10Ø@100
RB28	250x400	1829	2-16Ø	3-16Ø	10Ø@100
RB29	250x400	4877	2-16Ø	3-16Ø	10Ø@100
RB30	250x400	3962	2-16Ø	3-16Ø	10Ø@100
RB31	250x400	2438	2-16Ø	3-16Ø	10Ø@100
RB32	250x400	4572	2-16Ø	3-16Ø	10Ø@100
RB33	250x400	4877	2-16Ø	3-16Ø	10Ø@100
RB34	250x400	3962	2-16Ø	3-16Ø	10Ø@100
RB35	250x400	4572	2-16Ø	3-16Ø	10Ø@100
RB36	250x400	4877	2-16Ø	3-16Ø	10Ø@100
RB37	250x400	3962	2-16Ø	3-16Ø	10Ø@100
RB38	250x400	4572	2-16Ø	3-16Ø	10Ø@100
RB39	250x400	4877	2-16Ø	3-16Ø	10Ø@100
RB40	250x400	3962	2-16Ø	3-16Ø	10Ø@100
RB41	250x400	2438	2-16Ø	3-16Ø	10Ø@100
RB42	250x400	4572	2-16Ø	3-16Ø	10Ø@100
RB43	250x400	4877	2-16Ø	3-16Ø	10Ø@100
RB44	250x400	3962	2-16Ø	3-16Ø	10Ø@100
RB45	250x400	2438	2-16Ø	3-16Ø	10Ø@100
RB46	250x400	4572	2-16Ø	3-16Ø	10Ø@100
REB2	250x400	1940	2-16Ø	3-16Ø	10Ø@100
SB-R1	250x375	4267	2-16Ø	3-16Ø	10Ø@100
SB-R2	250x375	4267	2-16Ø	3-16Ø	10Ø@100
SB-R3	250x375	2438	2-16Ø	3-16Ø	10Ø@100
SB-R4	250x375	2743	2-16Ø	3-16Ø	10Ø@100

ALL ROOF BEAM STIRRUPS 10Ø@150 U.N.O.

10Ø@100 (ends)

B9 (CONTD. FROM S-17)

ROOF BEAM SCHEDULE 2 SCALE 1:50

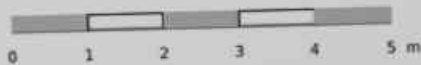

MEGHNA STRUCTURAL CONSULTANT

S LTD.

HOUSE 12, ROAD 5, BLOCK B, BANANI, DHAKA-1213

TEL +880 2 5555 9000

CLIENT

M/S. PADMA HOMES LTD.

PROJECT

PROPOSED G+6 STORIED RESIDENTIAL BUILDING

SITE

PLOT 23, ROAD 7, BLOCK C, BASHUNDHARA RA, DHAKA

SHEET TITLE

BEAM DETAILS (3 OF 3) - ROOF & SCHEDULE

DESIGNED

DRAWN

CHECKED

APPROVED

S.R.

M.H.

A.K.

T.I.

RAJUK REF.

RAJUK/RAP/2026/0417

JOB NO.

MSC-2026-041

DATE

12-08-2026

SCALE

1:50

SHEET NO.

S-18

REV.

B

REVISIONS

REV.	DATE	DESCRIPTION
A	05-07-2026	ISSUED FOR RAJUK APPROVAL
B	12-08-2026	CE 3RD-FTH BARS REVISED, ISSUED FOR

ALL DIMENSIONS IN mm U.N.O.

DO NOT SCALE THIS DRAWING



MEGHNA STRUCTURAL CONSULTANT
S LTD.
HOUSE 12, ROAD 1, BLOCK R, BANANI, DHAKA-1213
TEL: +880 2 5555 9000


CLIENT
M/S. PADMA HOMES LTD.

PROJECT
PROPOSED G+6 STORIED RESIDENTIAL BUILDING


SITE
PLOT 23, ROAD 7, BLOCK C, BASH
UNDHARA RA, DHAKA

SHEET TITLE
1ST FLOOR SLAB REINFORCEMENT PLAN

DESIGNED S.R.	DRAWN M.H.	CHECKED A.K.	APPROVED T.I.
RAJUK REF. RAJUK/RAP/2026/0417			
JOB NO. MSC-2026-041			
DATE 12-08-2026			
SCALE 1:100			
SHEET NO. S-19		REV. B	
REVISIONS			
REV.	DATE	DESCRIPTION	
A	05-07-2026	ISSUED FOR RAJUK APPROVAL	
B	12-08-2026	CE 3RD-FTH BARS REVISED, RESUBMITTED	

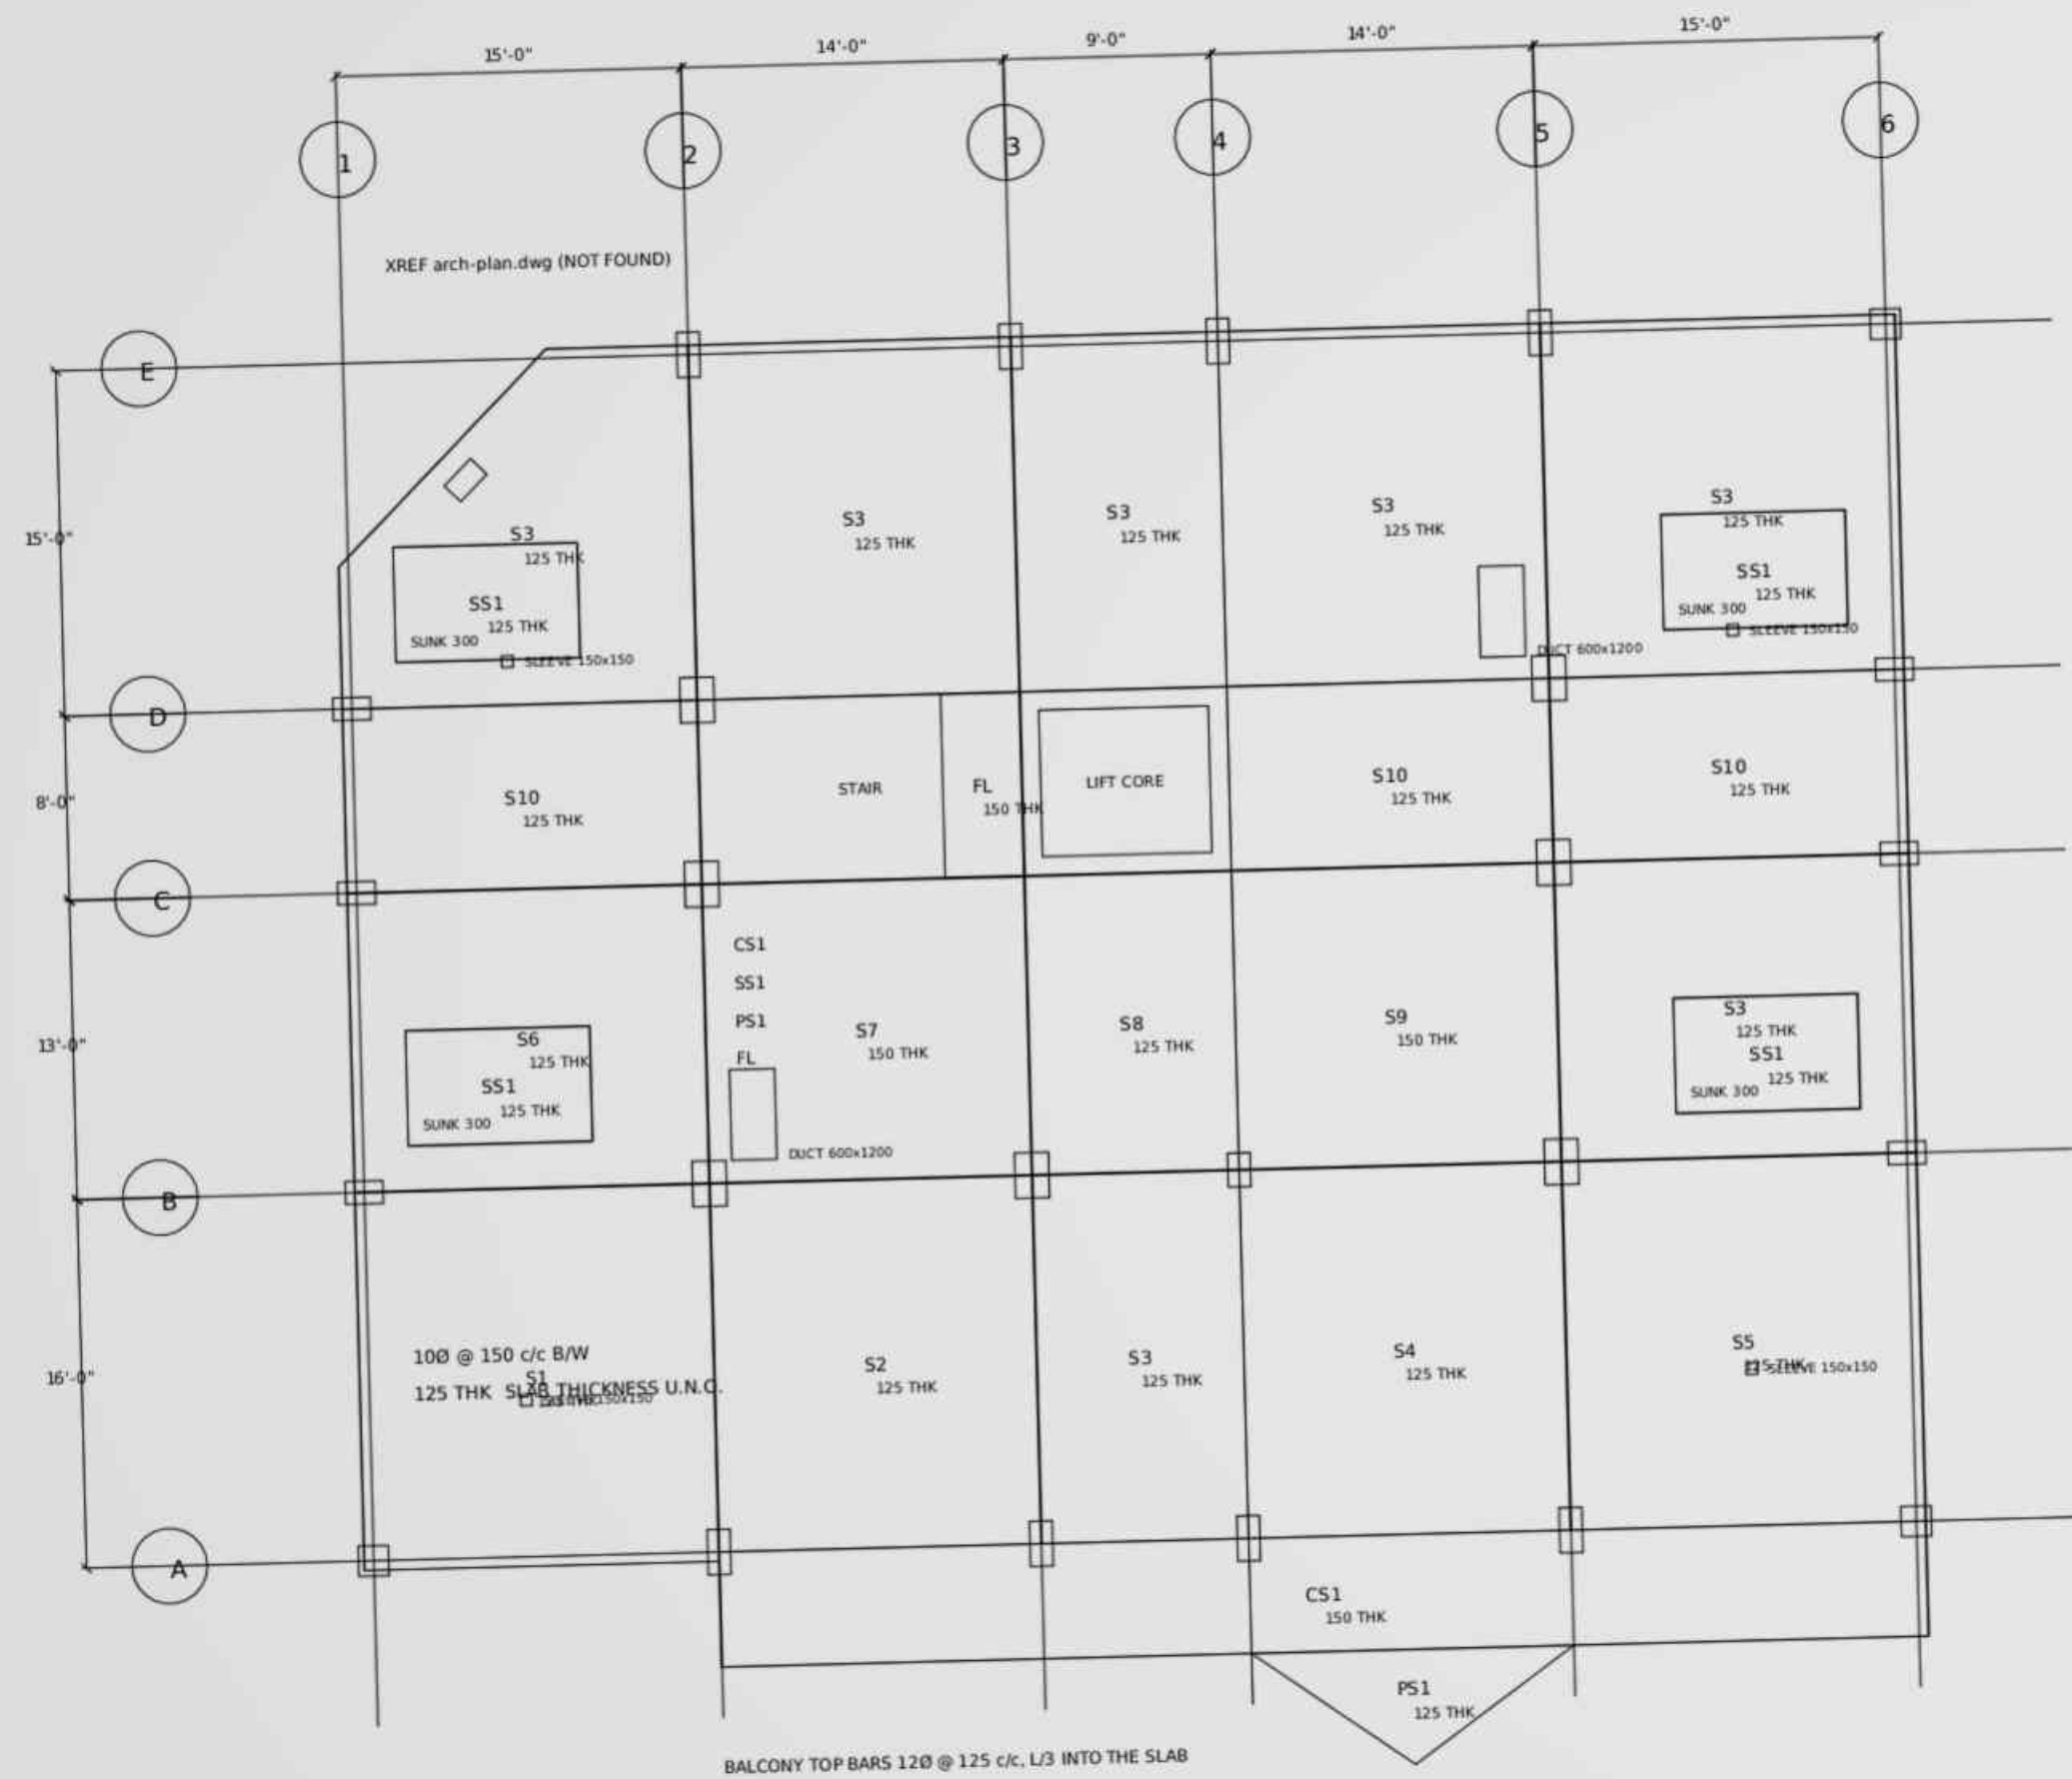


1ST FLOOR SLAB REINFORCEMENT PLAN SCALE 1:100

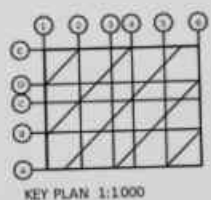





MEGHNA STRUCTURAL CONSULTANT S LTD. HOUSE 12, ROAD 5, BLOCK B, BANANI, DHAKA-1213 TEL +880 2 555 9000			
CLIENT MS. PADMA HOMES LTD.			
PROJECT PROPOSED G+6 STORIED RESIDENTIAL BUILDING			
SITE PLOT 23, ROAD 7, BLOCK C, BASH UNDHARA RA, DHAKA			
SHEET TITLE TYPICAL SLAB REINFORCEMENT PLAN			
DESIGNED S.R.	DRAWN M.H.	CHECKED A.K.	APPROVED T.I.
RAJUK REF. RAJUK/BAP/2026/0417			
JOB NO. MSC-2026-041			
DATE 12-08-2026			
SCALE 1:100			
SHEET NO. S-20		REV. B	
REVISIONS			
REV.	DATE	DESCRIPTION	
A	05-07-2026	ISSUED FOR RAJUK APPROVAL	
B	12-08-2026	CS AND 4TH BARS REVISED; ISSUED FOR	

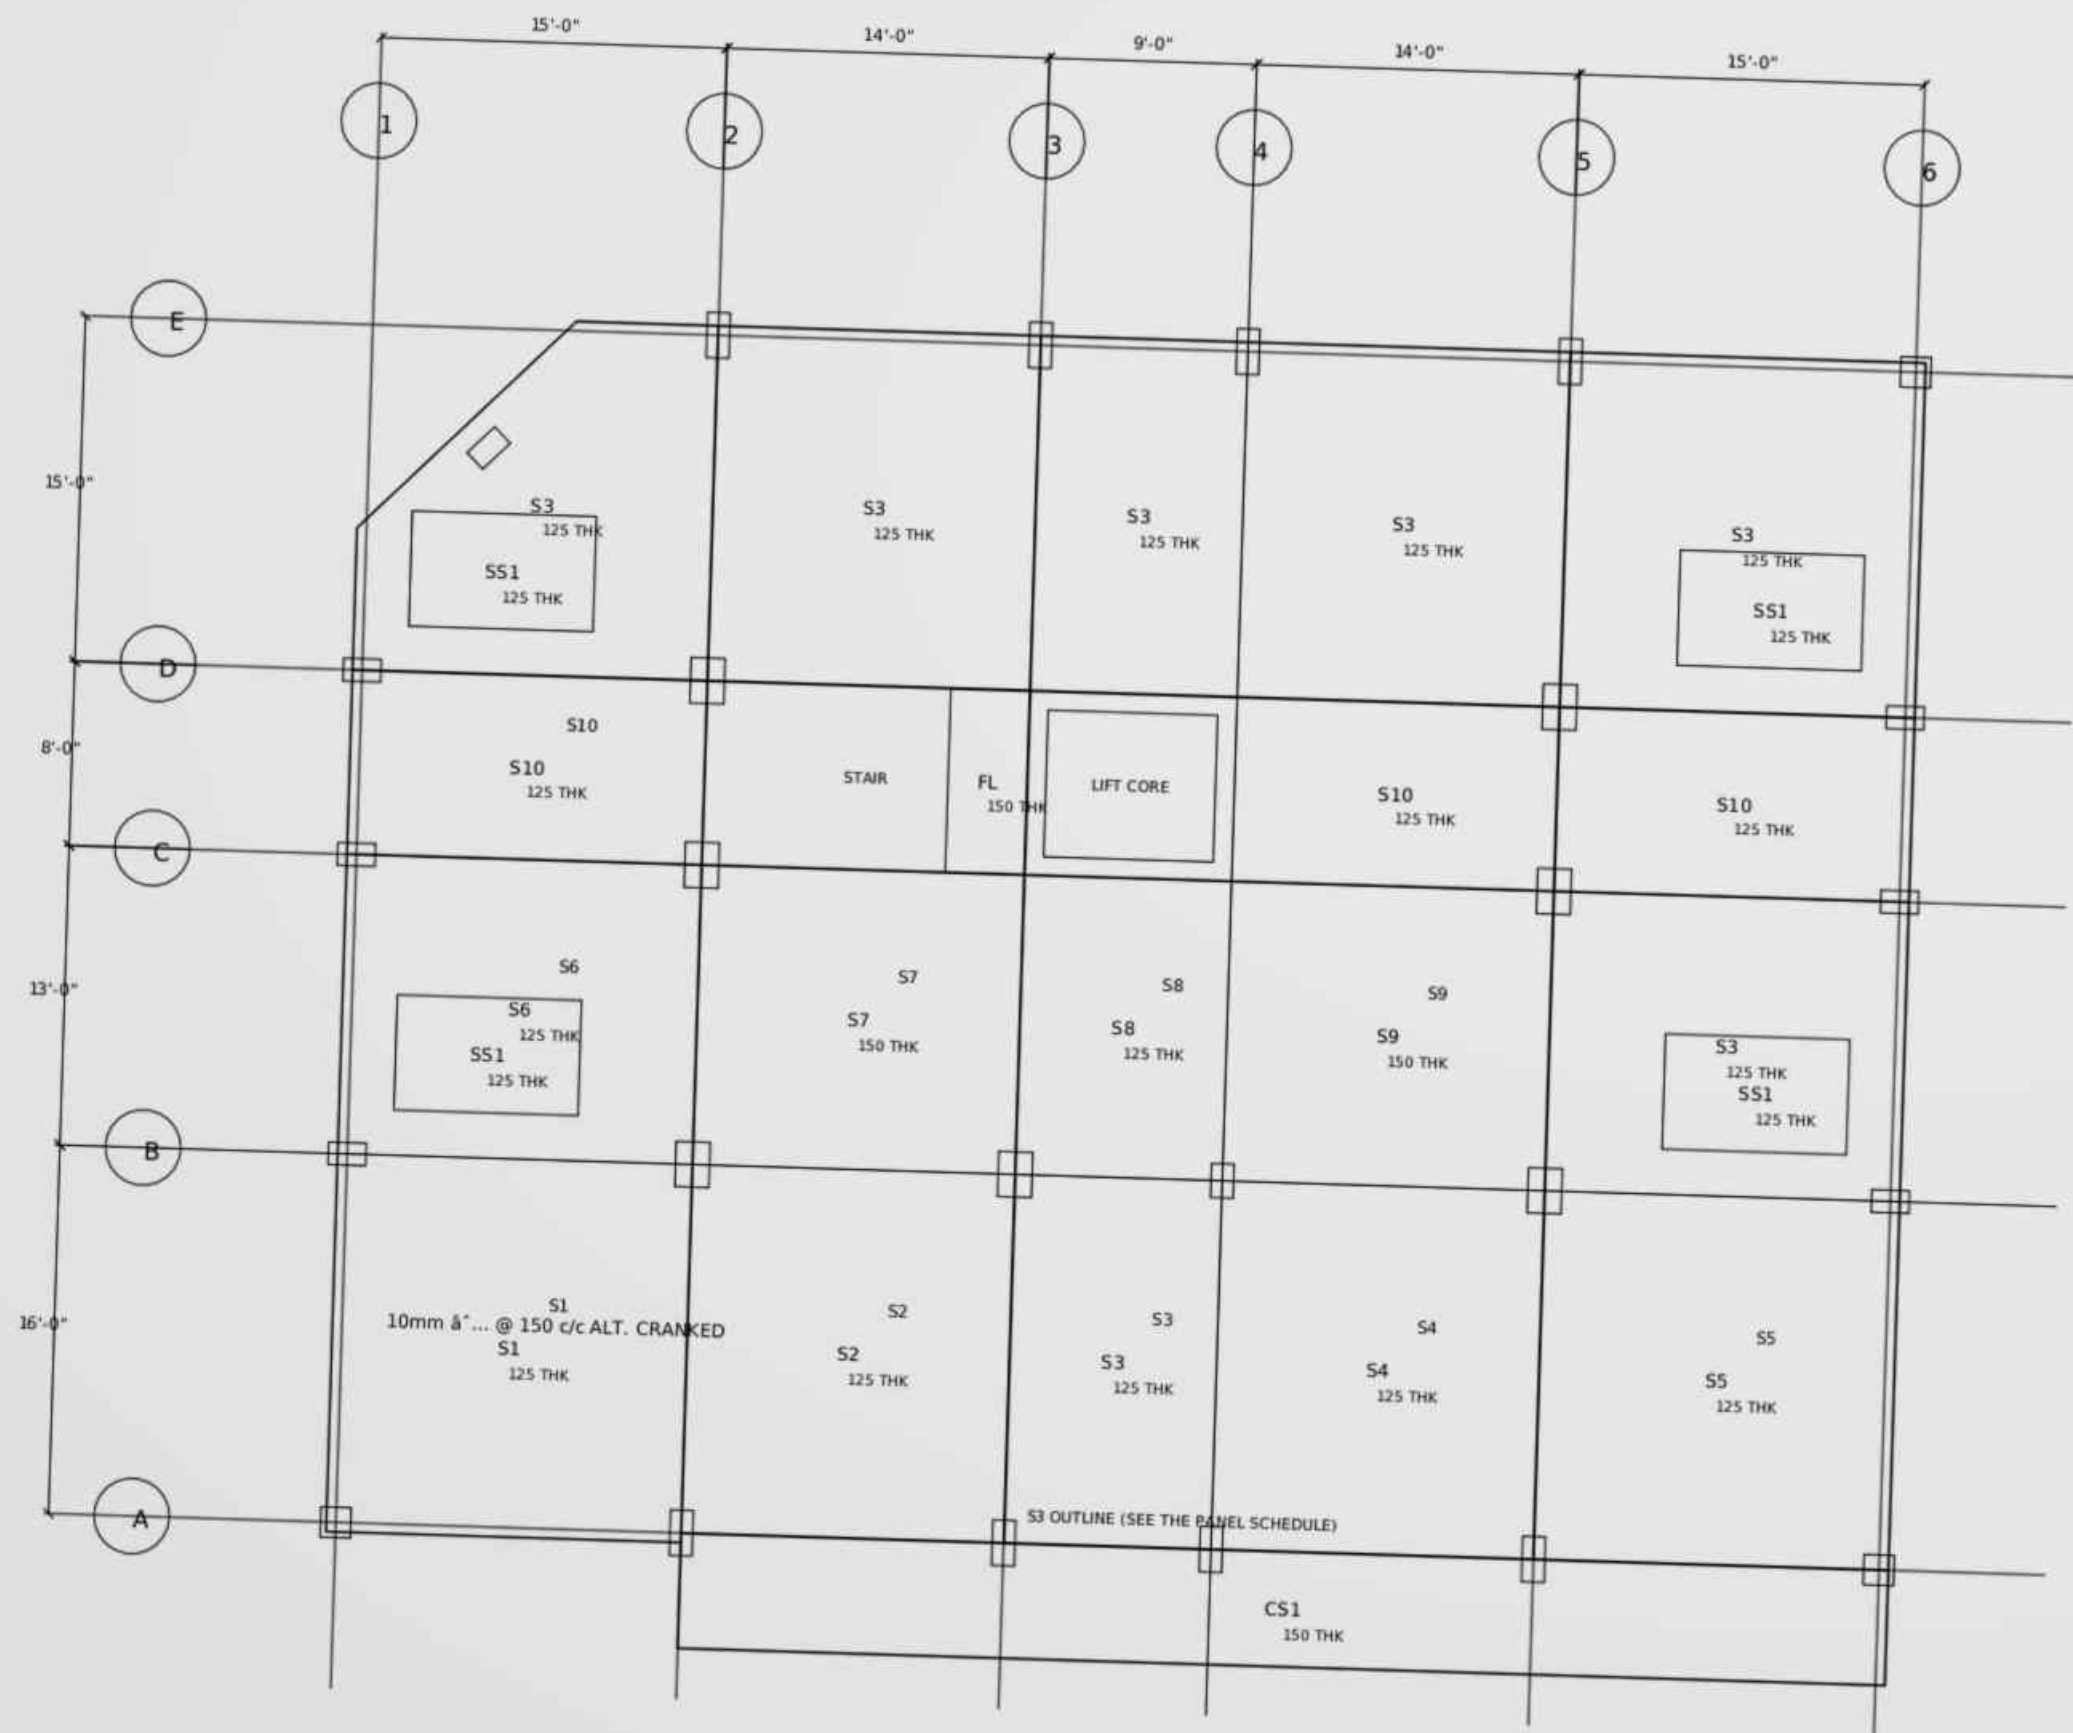


TYPICAL SLAB REINFORCEMENT PLAN

TYPICAL SLAB REINFORCEMENT PLAN SCALE 1:100

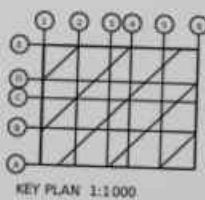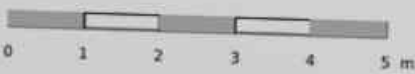





MEGHNA STRUCTURAL CONSULTANT S LTD. HOUSE 12, ROAD 5, BLOCK B, BANARI, DHAKA-1212 TEL: +880 2 5555 0000			
CLIENT M/S. PADMA HOMES LTD.			
PROJECT PROPOSED G+6 STORIED RESIDENTIAL BUILDING			
SITE PLOT 23, ROAD 7, BLOCK C, BASH UNIONHARA R/A, DHAKA			
SHEET TITLE ROOF, STAIR ROOF & PARAPET			
DESIGNED S.R.	DRAWN M.H.	CHECKED A.K.	APPROVED T.I.
RAJUK REF. RAJUK/RAP/2026/0417			
JOB NO. MSC-2026-041			
DATE 12-08-2026			
SCALE 1:100, 1:20			
SHEET NO. S-21			REV. B
REVISIONS			
REV	DATE	DESCRIPTION	
A	05-07-2026	ISSUED FOR RAJUK APPROVAL	
B	12-08-2026	ON 100-10% BASIS REVIEWED, ISSUED FOR	

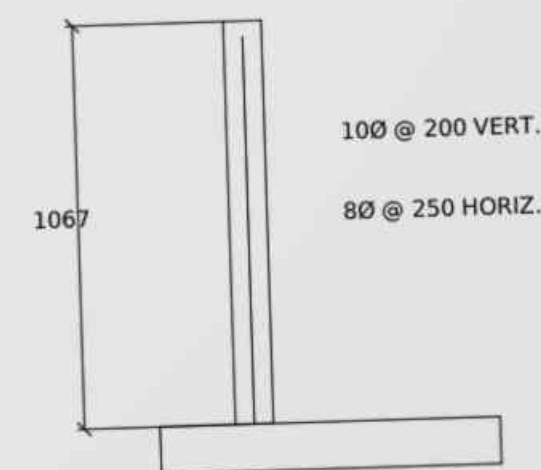

PARAPET DETAIL SCALE 1:20


ROOF & STAIR ROOF PLAN SCALE 1:100

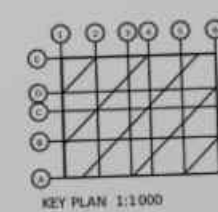

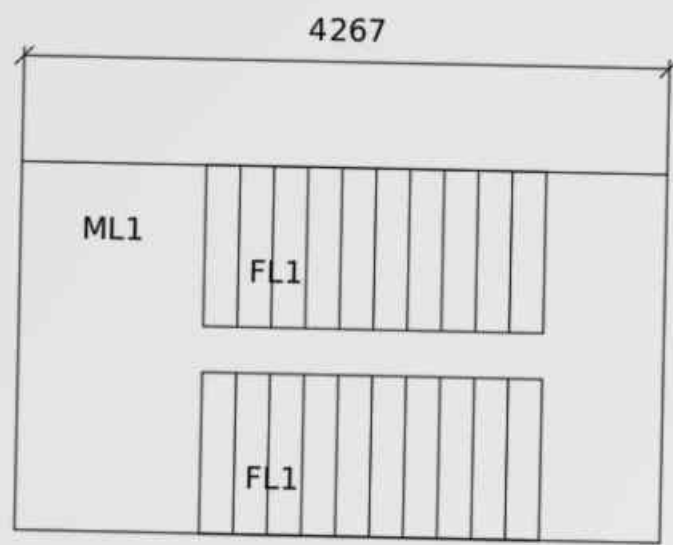


20 R @ 167.64 GOING 250

STAIR PLAN AT GROUND FLOOR SCALE 1:50

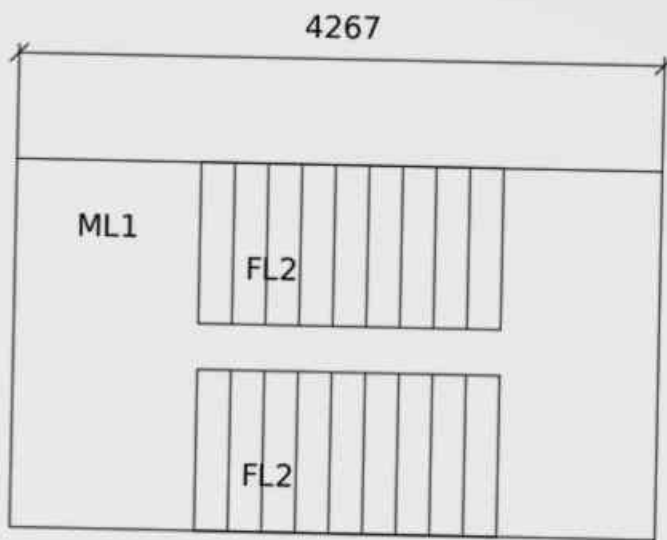

18 R @ 169.33 GOING 250

STAIR PLAN AT 1ST FLOOR (TYPICAL) SCALE 1:50

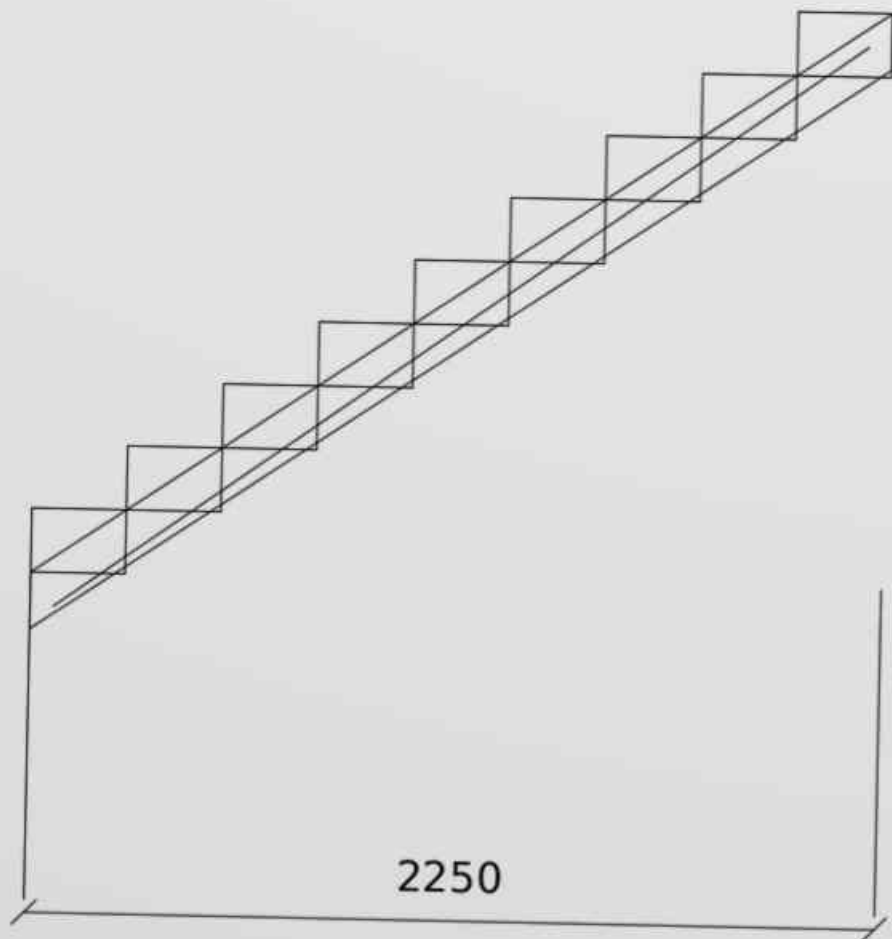

12Ø @ 125 c/c MAIN


8Ø @ 200 c/c DIST.

WAIST 150

FLIGHT WIDTH 3'-6½"

WELL 304 LANDING 1219

STAIR SECTION SCALE 1:20

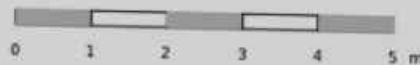

MEGHNA STRUCTURAL CONSULTANTS LTD.
HOUSE 12, ROAD 7, BLOCK B, BANAH, DHAKA-1213
TEL +880 2 5555 0000

CIENT
MS. PADMA HOMES LTD.

PROJECT
PROPOSED G+6 STORIED RESIDENTIAL BUILDING

SITE
PLOT 23, ROAD 7, BLOCK C, BASH
URDHARA RA, DHAKA

SHEET TITLE
STAIR DETAILS

DESIGNED
S.R.

DRAWN
M.H.

CHECKED
A.K.

APPROVED
T.I.

RAJUK REF. RAJUK/BAP/2026/0417

JOB NO. MSC-2026-041

DATE 12-08-2026

SCALE 1:50, 1:20

SHEET NO.
S-22

REV.
B

REVISIONS

REV

DATE

DESCRIPTION

A

05-07-2026

ISSUED FOR RAJUK APPROVAL


B

12-08-2026


ON JAG-RTM RARE REVISED ISSUED FOR

ALL DIMENSIONS IN mm U.S.D.
DO NOT SCALE THIS DRAWING


SHEAR WALL 250 THK (LOWER), 200 THK ABOVE 4F

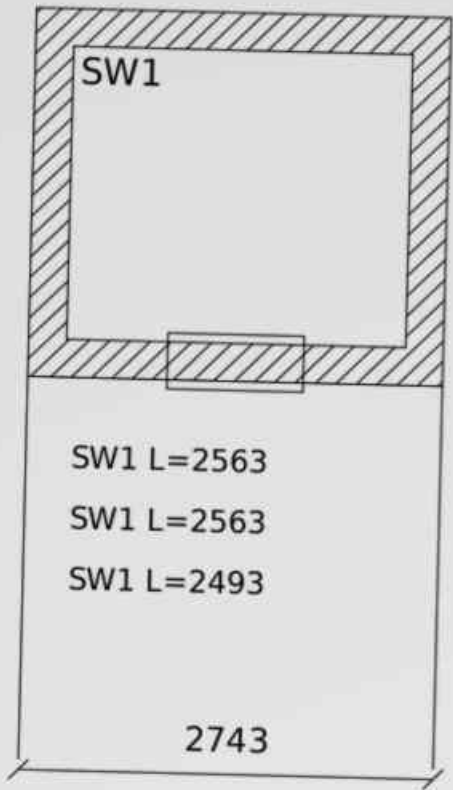

LIFT CORE PLAN SCALE 1:50

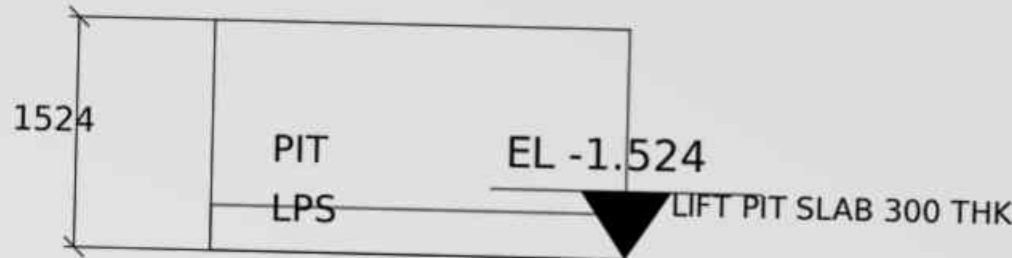


LIFT PIT SECTION SCALE 1:50

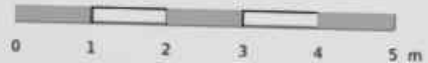

MEGHNA STRUCTURAL CONSULTANTS LTD. HOUSE 12, ROAD 6, BLOCK B, BANARI, DHAKA-1213 TEL: +880 2 5555 0000			
CLIENT M/S. PADMA HOMES LTD.			
PROJECT PROPOSED G+6 STORIED RESIDENTIAL BUILDING			
SITE PLOT 23, ROAD 7, BLOCK C, BASHUNDHARA RA, DHAKA			
SHEET TITLE LIFT CORE & SHEAR WALL DETAILS			
DESIGNED S.R.	DRAWN M.H.	CHECKED A.K.	APPROVED T.I.
RAJUK REF. RAJUK/BAP/2026/0417			
JOB NO. MSC-2026-041			
DATE 12-08-2026			
SCALE 1:50			
SHEET NO. S-23		REV. B	
REVISIONS			
REV.	DATE	DESCRIPTION	
A	05-07-2026	ISSUED FOR RAJUK APPROVAL	
B	12-08-2026	G+6 RD-THK RABD REVISION, ISSUED FOR	
ALL DIMENSIONS IN mm U.N.D. DO NOT SCALE THIS DRAWING			


OVERHEAD WATER TANK

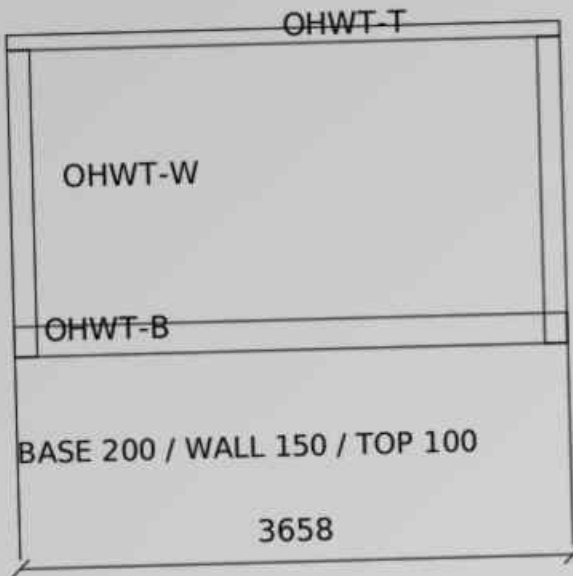

MANHOLE 600x600


OVERHEAD WATER TANK SCALE 1:50

UNDERGROUND WATER RESERVOIR

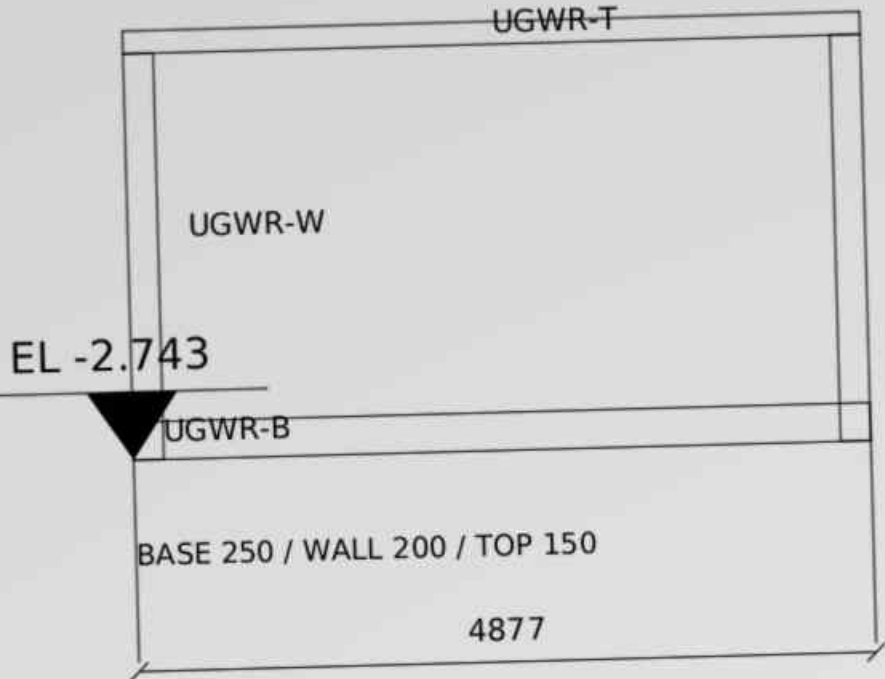

UNDERGROUND WATER RESERVOIR SCALE 1:50

SEPTIC TANK

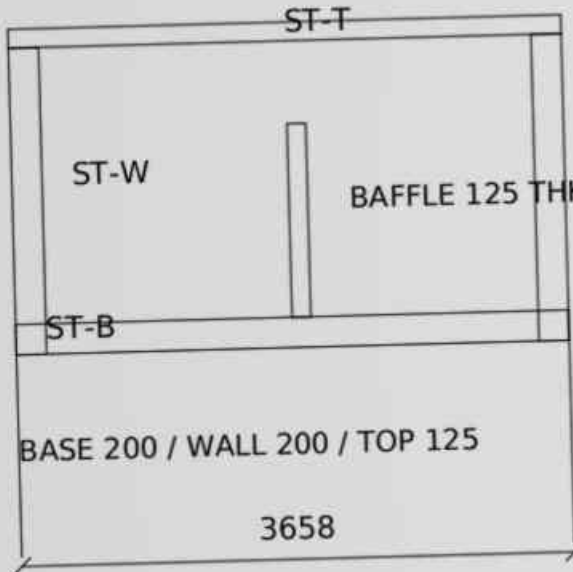

BAFFLE 125 THK, 2 CHAMBERS

SEPTIC TANK SCALE 1:50



MEGHNA STRUCTURAL CONSULTANT
S LTD.
HOUSE 12, ROAD 5, BLOCK B, BANANI, DHAKA 1213
TEL +880 2 5555 0000

CLIENT
M/S. PADMA HOMES LTD.

PROJECT
PROPOSED G+6 STORIED RESIDENTIAL BUILDING

SITE
PLOT 23, ROAD 7, BLOCK C, BASH
UNDHARA RA, DHAKA

SHEET TITLE
OVERHEAD WATER TANK & UGWR / SEPTIC TANK

DESIGNED
S.R.

DRAWN
M.H.

CHECKED
A.K.

APPROVED
T.I.

RAJUK REF. RAJUK/RAP/2026/0417

JOB NO. MSC-2026-041

DATE 12-08-2026

SCALE 1:50

SHEET NO.
S-24

REV.
B

REVISIONS

REV

DATE

DESCRIPTION

A

05-07-2026

ISSUED FOR RAJUK APPROVAL

B

12-08-2026

CO 2ND-4TH RANKS REVISED; ISSUED TO

ALL DIMENSIONS IN mm U.N.O.
DO NOT SCALE THIS DRAWING

LINTEL & SUNSHADE SCHEDULE

MARK	SIZE	BARS	OPENING (mm)		
L1	250x150	2-12%%C T&B + 8%%C @ 150	1000	L1	OVEF
L2	250x200	2-12%%C T&B + 8%%C @ 150	1200	L2	OVEF
LS1	250x200	2-12%%C T&B + 8%%C @ 150	1500	LS1	OVEF


BW250 BRICK WALL 250 THK
BW125 BRICK WALL 125 THK

BW250
BW125

LINTEL & SUNSHADE SCHEDULE SCALE 1:50



BUILDING SECTION A-A SCALE 1:100

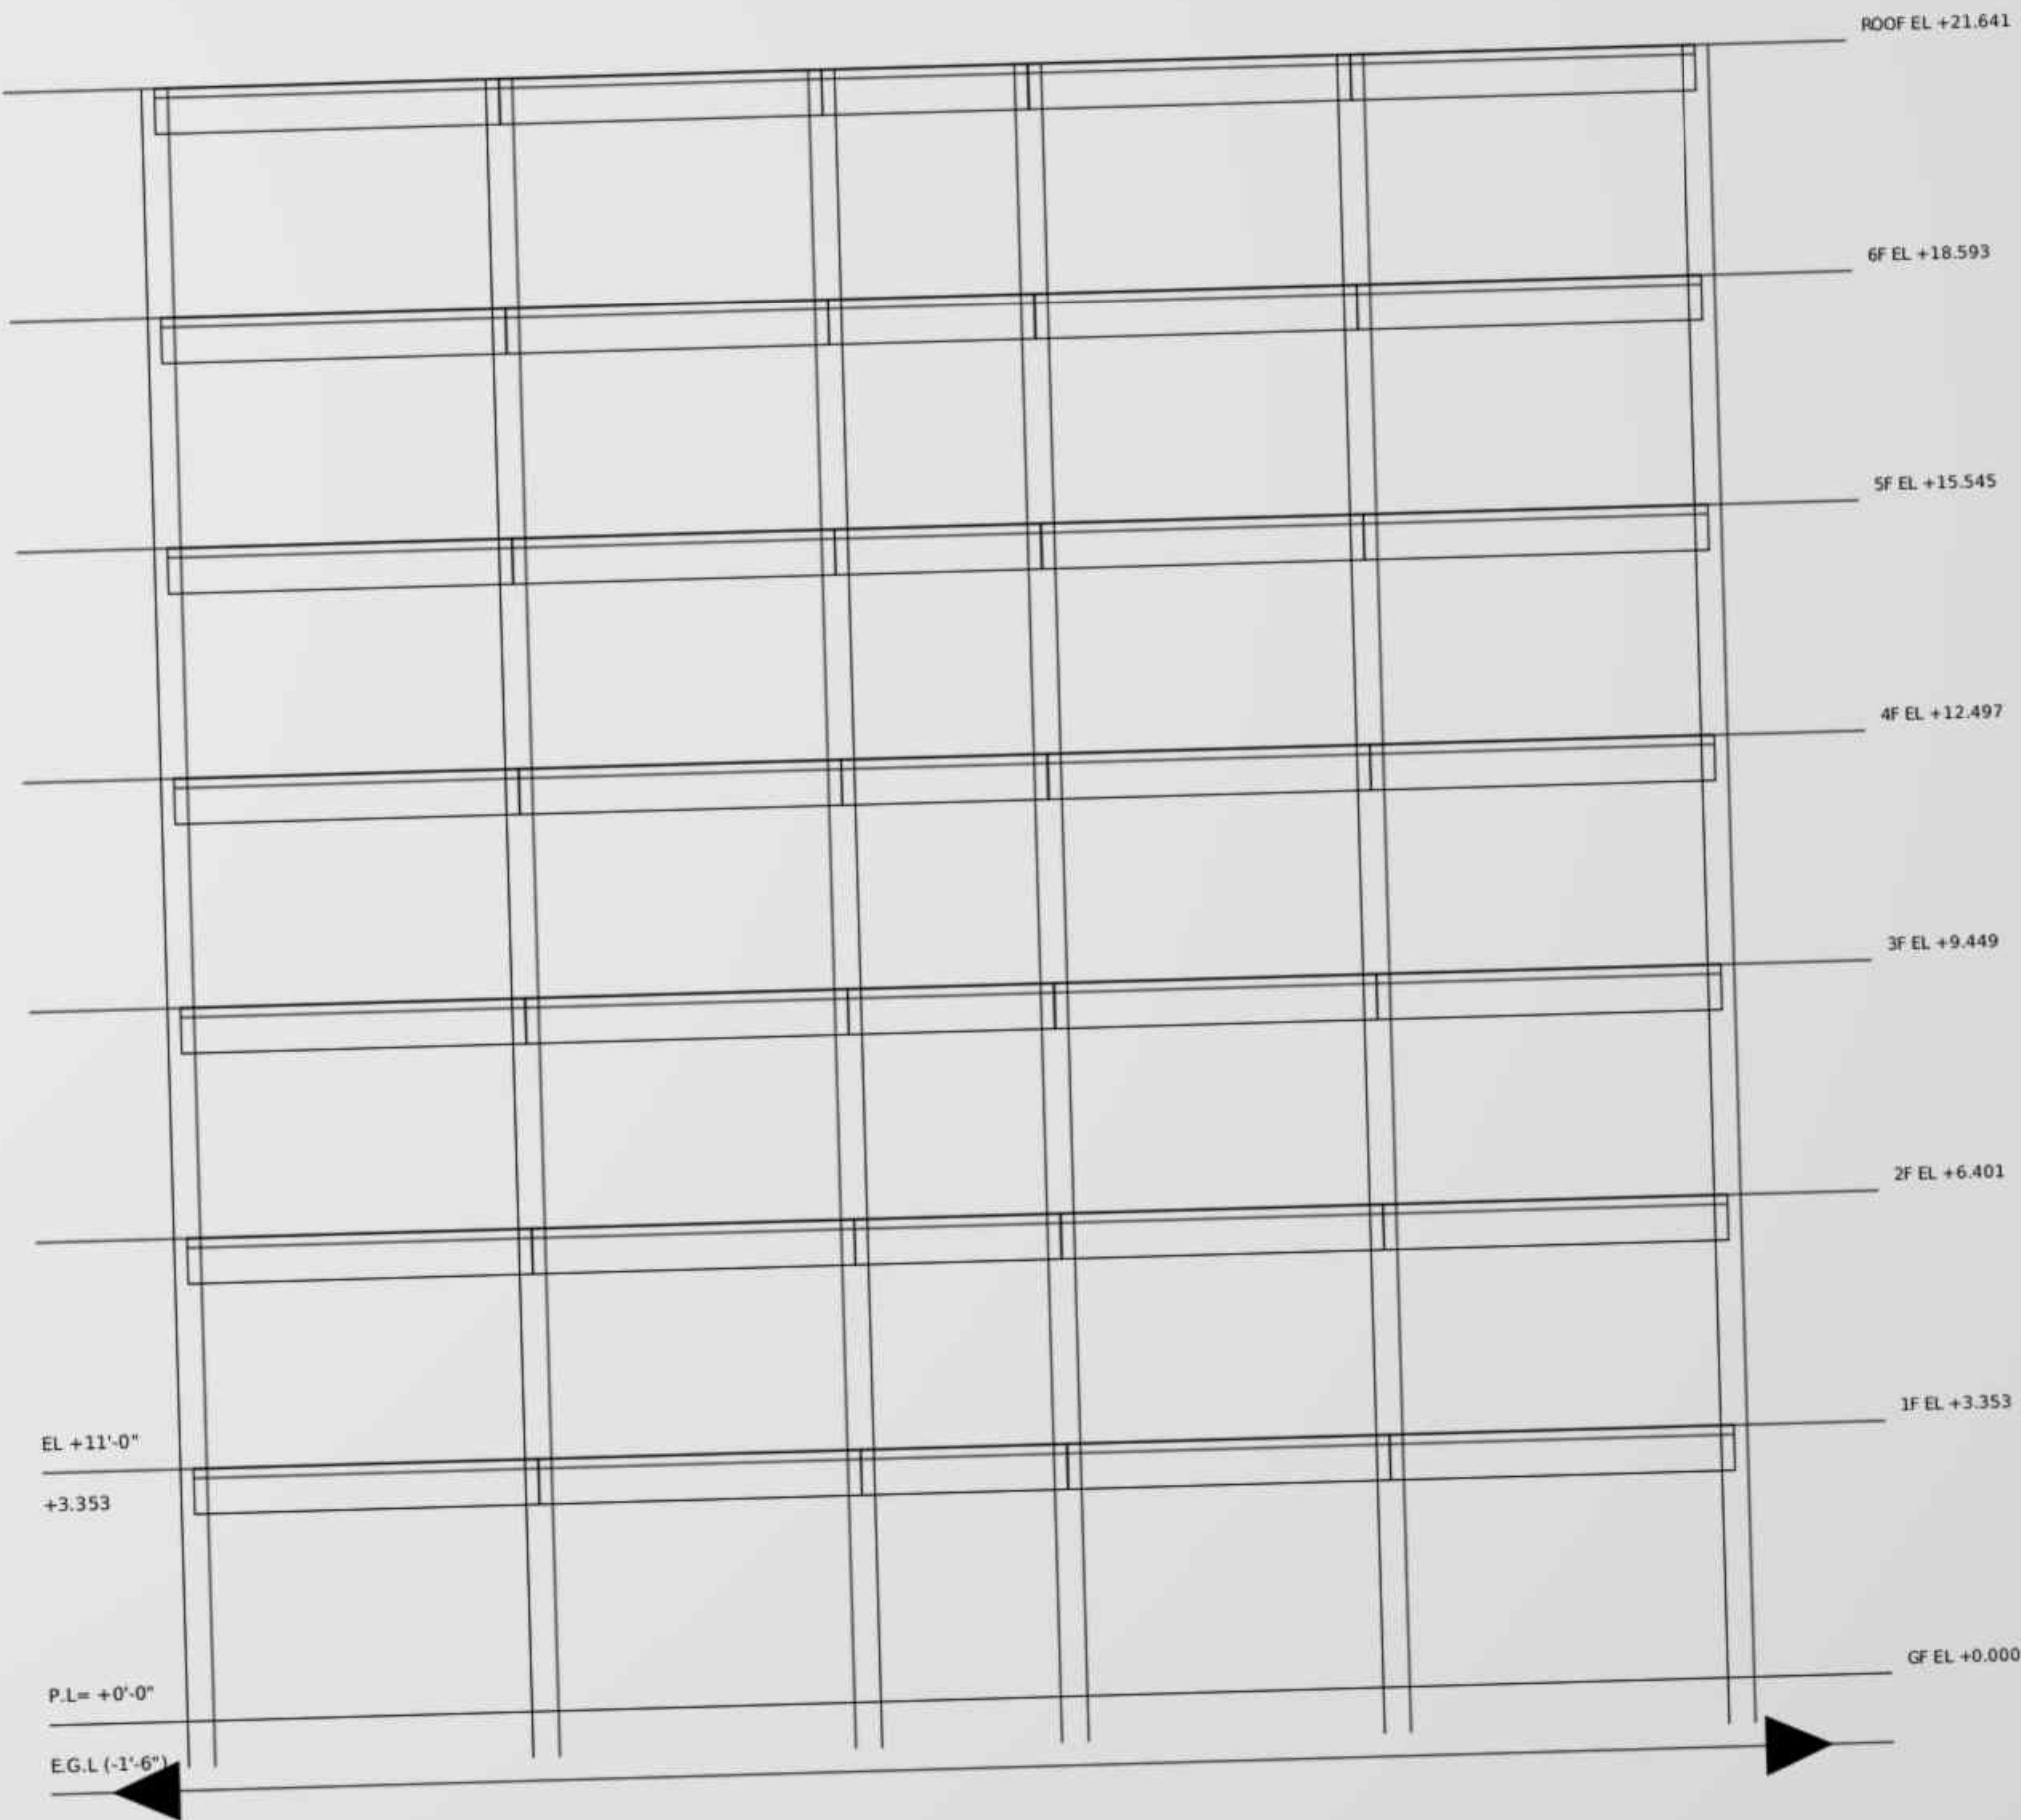

SECTION A-A

MEGHNA STRUCTURAL CONSULTANT
S LTD.
HOUSE 12, ROAD 5, BLOCK B, BANANI, DHAKA-1213
TEL +880 2 5555 0000

CLIENT
M'S. PADMA HOMES LTD.

PROJECT
PROPOSED G+6 STORIED RESIDENTI
AL BUILDING

SITE
PLOT 23, ROAD 7, BLOCK C, BASH
URDHARA R/A, DHAKA

SHEET TITLE
LINTEL & SUNSHADE SCHEDULE, BU
ILDING SECTION

DESIGNED	DRAWN	CHECKED	APPROVED
S.R.	M.H.	A.K.	T.I.

RAJUK REF.	RAJUK/BAP/2026/0417
JOB NO.	MSC-2026-041
DATE	12-08-2026
SCALE	1:100
SHEET NO.	REV.
S-25	B

REVISIONS

REV	DATE	DESCRIPTION
A	05-07-2026	ISSUED FOR RAJUK APPROVAL
B	12-08-2026	CS 3RD-4TH BARS REVISION, HOUSE FO

ALL DIMENSIONS IN mm U.N.O.
DO NOT SCALE THIS DRAWING

BAR BENDING SCHEDULE (SAMPLE)

BS 8666 CUTTING LENGTHS; SEE bbs.golden.json

MEMBER	BAR MARK	SHAPE	DIA	A / B / C (mm)	CUT LENGTH	NOS	MASS (kg)
PC3	PC3-bx	21	16Ø	A=192.000/B=1850.000/C=192.000	2175	15	51.396
PC3	PC3-by	21	16Ø	A=192.000/B=1850.000/C=192.000	2175	15	51.396
PC3	PC3-tx	21	12Ø	A=144.000/B=1850.000/C=144.000	2100	10	18.559
PC3	PC3-ty	21	12Ø	A=144.000/B=1850.000/C=144.000	2100	10	18.559
PC3	PC3-s	00	12Ø	A=7400.000	7400	3	19.714
2B7	B7-b	00	16Ø	A=5417.200	5425	3	25.661
2B7	B7-bx	00	16Ø	A=1908.600	1925	2	6.027
2B7	B7-t	00	16Ø	A=5897.200	5900	2	18.623
2B7	B7-tx1	00	20Ø	A=2336.800	2350	2	11.525
2B7	B7-s	51	10Ø	A=200.000/B=400.000/C=200.000/D=400.000/E=100.000/F=100.000	4000	38	26.426
S3	S3-bx	21	10Ø	A=120.000/B=2703.200/C=120.000	2925	17	30.402
S3	S3-cx	CRK	10Ø	A=2703.200/B=35.700/C=35.700	2700	16	26.558
S3	S3-tx	11	10Ø	A=1371.600/B=120.000	1475	66	59.829
S3	S3-by	21	10Ø	A=120.000/B=4836.800/C=120.000	5050	10	31.027
S3	S3-cy	CRK	10Ø	A=4836.800/B=35.700/C=35.700	4850	9	26.768
S3	S3-ty	11	10Ø	A=2438.400/B=120.000	2550	38	59.419

GRAND TOTAL (KG) 169458.751

(THE ROW SUMS ARE THE TRUTH; THIS TOTAL IS THE TYPIST'S)

MEGHNA STRUCTURAL CONSULTANT
S LTD.
HOUSE 12, ROAD 5, BLOCK B, BANANI, DHAKA-1213
TEL +880 2 5555 0000

CLIENT
M/S. PADMA HOMES LTD.

PROJECT
PROPOSED G+6 STORIED RESIDENTIAL BUILDING

SITE
PLOT 23, ROAD 7, BLOCK C, BASH
UNDHARA R/A, DHAKA

SHEET TITLE
BAR BENDING SCHEDULE (SAMPLE:
PC3, 2B7, SLAB S3)

DESIGNED
S.R.

DRAWN
M.H.

CHECKED
A.K.

APPROVED
T.I.

RAJUK REF. RAJUK/BAP/2026/0417

JOB NO. MSC-2026-041

DATE 12-08-2026

SCALE N.T.S.

SHEET NO.
S-26

REV.
B

REVISIONS

REV	DATE	DESCRIPTION
A	05-07-2026	ISSUED FOR RAJUK APPROVAL
B	12-08-2026	ON 3RD-4TH BARS REVISED; ISSUED FOR

ALL DIMENSIONS IN mm U.N.O.
DO NOT SCALE THIS DRAWING